




TELESCOPIC GATE – ELEVATION

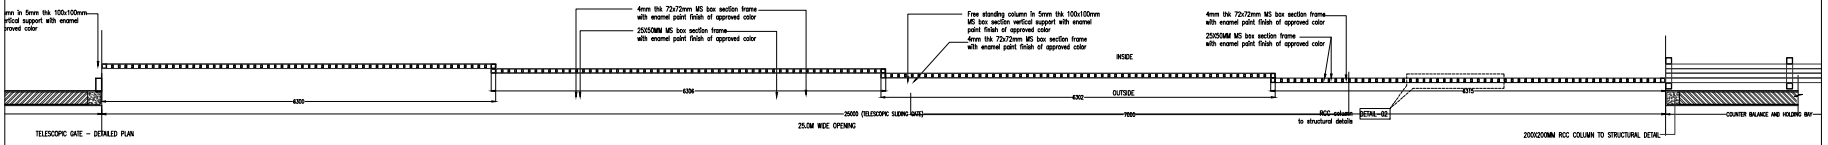


TELESCOPIC GATE – DETAILED PLAN

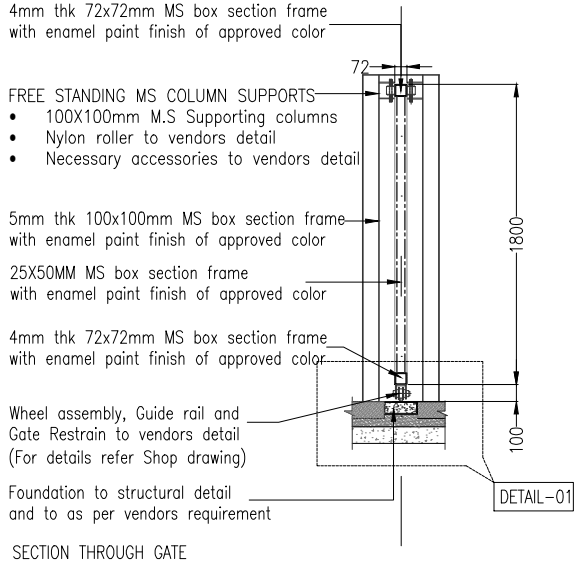


SECTION THROUGH GATE

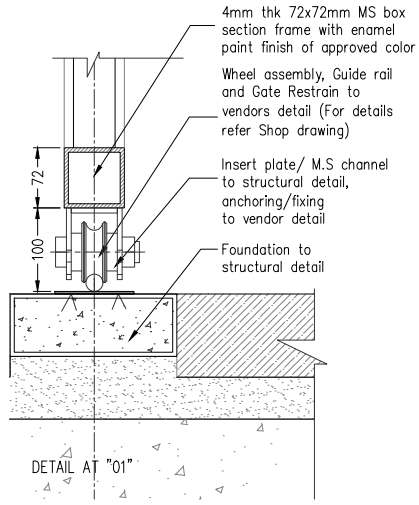

DETAIL AT "01"

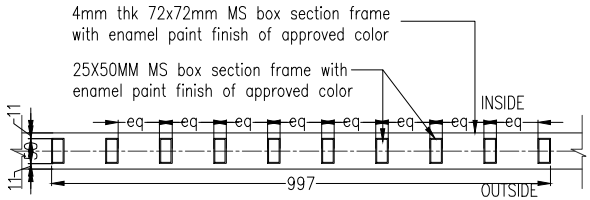

DETAIL AT "02"

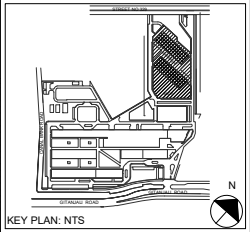

NOTE :
- ALL DIMENSIONS ARE IN MILLIMETERS - THIS DRAWING IS A COPYRIGHT AND PROPERTY OF THE RSP DESIGN CONSULTANTS (I) PVT LTD, IS NOT TO BE PRODUCED, COPIED, HANDED OVER TO THIRD PARTY OR USED FOR ANY OTHER PURPOSE OTHER THAN FOR WHICH IT IS INTENDED.
- ALL DIMENSIONS SHALL BE VERIFIED ON SITE PRIOR TO START OF WORK ANY DISCREPANCY SHALL BE BROUGHT TO THE NOTICE OF THE RSP DESIGN CONSULTANTS (I) PVT LTD
- THIS PROJECT MANAGER/CONTRACTOR MUST CHECK ALL DIMENSIONS AND DETAILS AND BE RESPONSIBLE FOR THE SAME. ANY DISCREPANCY SHALL BE BROUGHT TO THE NOTICE OF RSP DESIGN CONSULTANTS (I) PVT LTD
- THIS DIMENSIONS IS TO BE READ AND NOT SCALED
- DRAWING SHALL BE READ IN CONJUNCTION WITH ALL RELEVANT BUILDING SERVICES WORKING DRAWINGS AND ANY DISCREPANCY NOTICED SHALL BE BROUGHT TO THE ATTENTION OF THE CONSULTANTS WITHIN 7 WORKING DAYS OF RECEIPT OF THIS DRAWINGS, BUT ALWAYS PRIOR TO PROCUREMENT AND/OR EXECUTION OF WORKS
- DRAWING APPROVAL IS FOR THE CONFORMITY WITH OUTLINE DESIGN INTENT ONLY AND DOES NOT RELIEVE THE PROJECT MANAGERS / CONTRACTORS / SUB-CONTRACTORS OF THEIR RESPONSIBILITY FOR THE ACCURACY, INTEGRATION AND FITNESS FOR PURPOSE OF DESIGN
- PROJECT MANAGERS OF THE CONTRACTOR TO REVERT BACK WITHIN 7 WORKING DAYS OF RECEIPT OF THIS DRAWINGS ON COORDINATION AND BUILDABILITY ISSUES, IF OTHERWISE IT WOULD BE DEEMED THAT THEY HAVE UNDERSTOOD AND ACCEPTED THE DRAWING / DESIGN AND OWN FULL RESPONSIBILITY FOR THE WORKS CARRIED OUT ACCORDINGLY.

PROJECT ID: 20097	ORIENTATION :

PROJECT TITLE : SANCHAYITA PARK

PROPOSED OFFICE BUILDING FOR M/S. TATA CONSULTANCY SERVICES LIMITED.

CLIENT :
TATA CONSULTANCY SERVICES LIMITED
ITITIOS SEZ, Plot- IIF / 3, Action Area - 2, New Town, Rajarhat, Kolkata – 700135, West Bengal, India, Ph.- 033 66538781/Buzz- 4398781

PROJECT CONSULTANTS :
RSP DESIGN CONSULTANTS (INDIA) PVT LTD
RSP HOUSE, # 30, MUSEUM ROAD, BANGALORE - 560001 TEL: 25596868 FAX: 25596818

STRUCTURAL CONSULTANTS:
S.P.A. CONSULTANTS
34 ISWARCHAN DUTTA ROAD, KOLKATA - 700020, INDIA. TEL: 033-24855449 /24757614 24855448

MEP CONSULTANTS :
GRUNE DESIGNS
603, Lodha Supremus, Saki Vihar Road, Powai, Andheri (East), Mumbai – 400072 TEL: 25596868 FAX : 25596818

PROJECT MANAGEMENT CONSULTANTS :
TATA CONSULTING ENGINEERS LIMITED


SUBJECT OF DRAWING :
TELESCOPIC GATE DETAILS AT MAIN ENTRY/EXIT

FILE NAME :


SCALE : AS MENT	DATE : 20 JUL 2021
DEALT : NB	CHECKED : RA

DRAWING NO: L-GF-4300 | REV NO: 00


A1 : 841MM X 594 MM

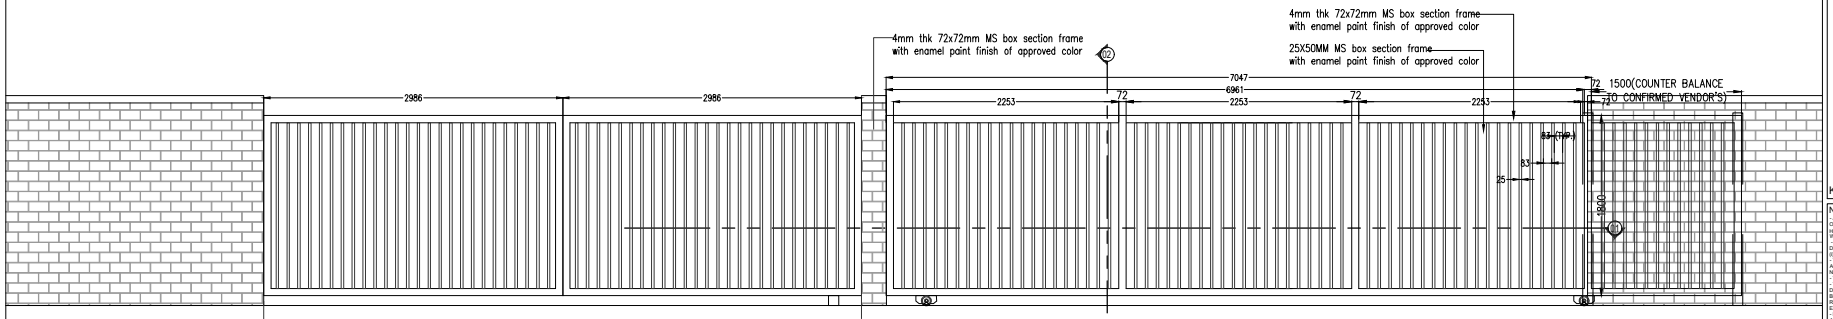


EXIT GATE DETAILED ELEVATION

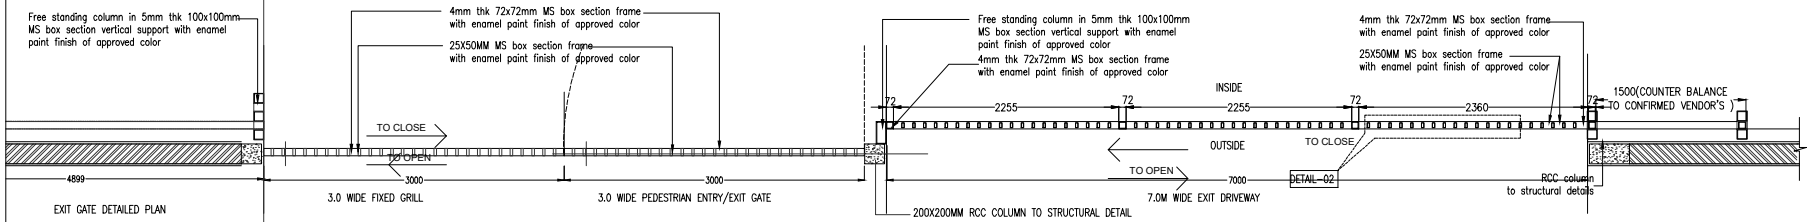


EXIT GATE DETAILED PLAN

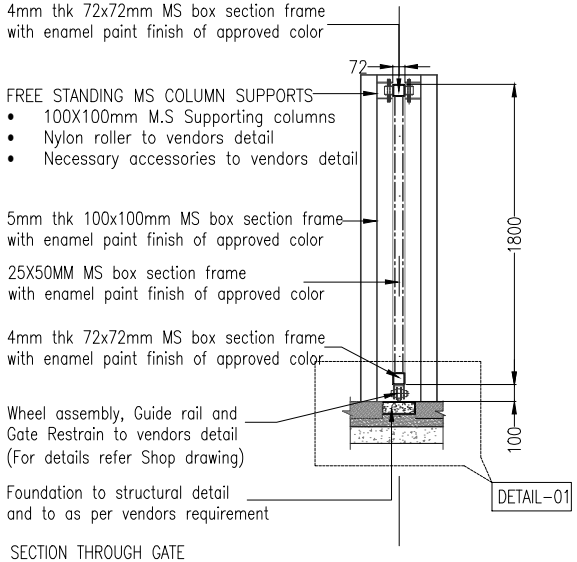


SECTION THROUGH GATE

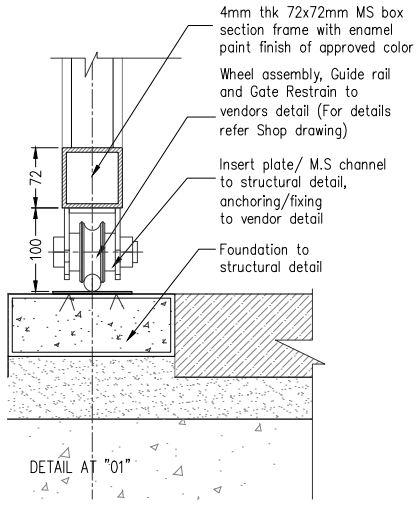

DETAIL AT "01"

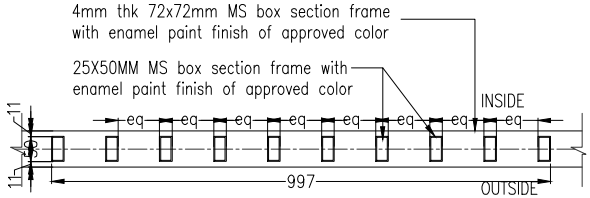

DETAIL AT "02"

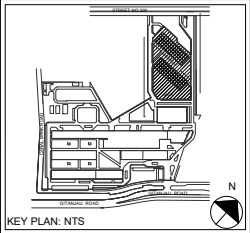

KEY PLAN: NTS

NOTE :
- ALL DIMENSIONS ARE IN MILLIMETERS - THIS DRAWING IS A COPYRIGHT AND PROPERTY OF THIS RSP DESIGN CONSULTANTS (I) PVT. LTD. IS NOT TO BE PRODUCED, COPIED, HANDED OVER TO THIRD PARTY OR USED FOR ANY OTHER PURPOSE OTHER THAN FOR WHICH IT IS INTENDED.
- ALL DIMENSIONS SHALL BE VERIFIED ON SITE PRIOR TO START OF WORK ANY DISCREPANCY SHALL BE BROUGHT TO THE NOTICE OF THE RSP DESIGN CONSULTANTS (I) PVT LTD
- THIS PROJECT MANAGER/CONTRACTOR MUST CHECK ALL DIMENSIONS AND DETAILS AND BE RESPONSIBLE FOR THE SAME. ANY DISCREPANCY SHALL BE BROUGHT TO THE NOTICE OF RSP DESIGN CONSULTANTS (I) PVT LTD
- THIS DIMENSIONS IS TO BE READ AND NOT SCALED
- DESIGN & WORKING DETAILS SHALL BE IN CONFORMITY WITH ALL RELEVANT BUILDING BYELAWS. WHERE SHALL ARISE ANY CONTRADICTION AND DISCREPANCY NOTICED SHALL BE BROUGHT TO THE ATTENTION OF THE CONSULTANTS WITHIN 7 WORKING DAYS OF RECEIPT OF THIS DRAWINGS, BUT ALWAYS PRIOR TO PROCUREMENT AND/OR EXECUTION OF WORKS
- DRAWING APPROVAL IS FOR THE CONFORMITY WITH OUTLINE DESIGN INTENT ONLY AND DOES NOT RELIEVE THE PROJECT MANAGERS / CONTRACTORS / SUB-CONTRACTORS OF THEIR RESPONSIBILITY FOR THE ACCURACY, INTEGRATION AND FITNESS FOR PURPOSE OF DESIGN
- PROJECT MANAGERS OF THE CONTRACTOR TO REVERT BACK WITHIN 7 WORKING DAYS OF RECEIPT OF THIS DRAWINGS ON COORDINATION AND BUILDABILITY ISSUES, IF OTHERWISE IT WOULD BE DEEMED THAT THEY HAVE UNDERSTOOD AND ACCEPTED THE DRAWING / DESIGN AND OWN FULL RESPONSIBILITY FOR THE WORKS CARRIED OUT ACCORDINGLY.

PROJECT ID: 20097

ORIENTATION :

PROJECT TITLE : SANCHAYITA PARK

PROPOSED OFFICE BUILDING FOR M/S. TATA CONSULTANCY SERVICES LIMITED.

CLIENT :
TATA CONSULTANCY SERVICES LIMITED
ITITIDS SEZ, Plot- IIF / 3, Action Area - II, New Town, Rajarhat, Kolkata – 700156, West Bengal, India, Ph.- 033 66538781/Buzz- 4366781

PROJECT CONSULTANTS :
RSP DESIGN CONSULTANTS (INDIA) PVT LTD
RSP HOUSE, # 30, MUSEUM ROAD, BANGALORE - 560001 TEL: 25596868 FAX: 25596818

STRUCTURAL CONSULTANTS:
S.P.A. CONSULTANTS
34 ISABELDHAN DUTTA ROAD, KOLKATA - 700020, INDIA. TEL: 033-24855449 /24757614 24855448

MEP CONSULTANTS :
GRUNE DESIGNS
603, Lodha Supremus, Saki Vihar Road, Powai, Andheri (East), Mumbai – 400072 TEL: 25599868 FAX : 25599818

PROJECT MANAGEMENT CONSULTANTS :
TATA CONSULTING ENGINEERS LIMITED


SUBJECT OF DRAWING :
GATE DETAILS AT EXIT AREA & PEDESTRIAN ENTRY/EXIT

FILE NAME :


SCALE : 1:600	DATE : 20 JUL 2021
DEALT : NB	CHECKED : RA

DRAWING NO: L-GF-4400 | REV NO: 00


A1 : 841MM X 594 MM

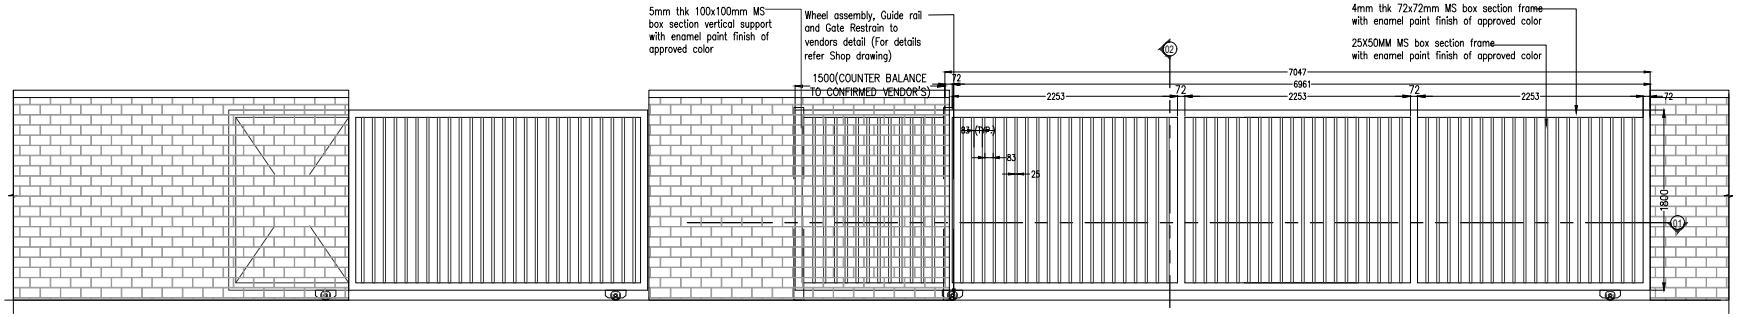


EXIT GATE DETAILED ELEVATION

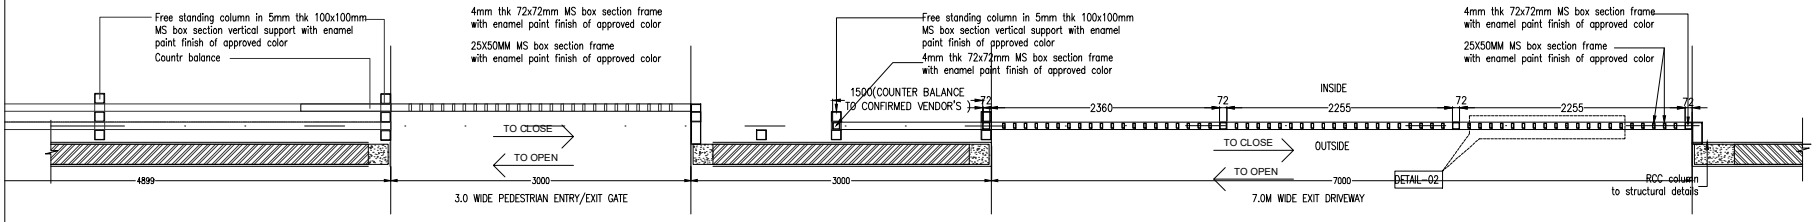


EXIT GATE DETAILED PLAN

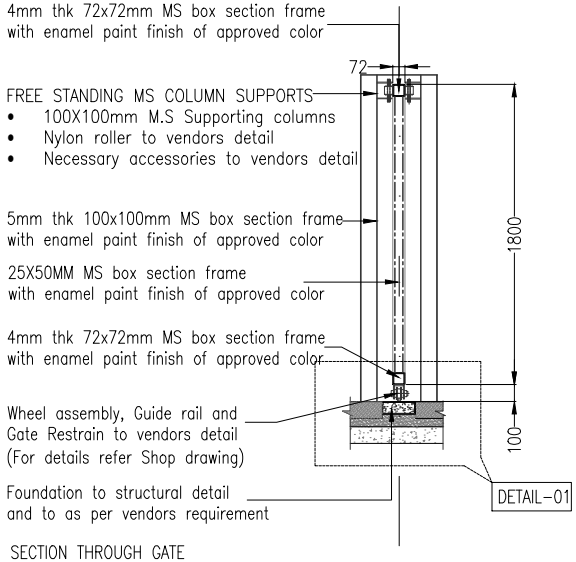


SECTION THROUGH GATE

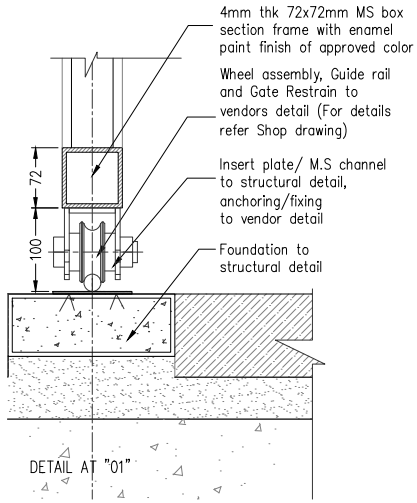

DETAIL AT "01"

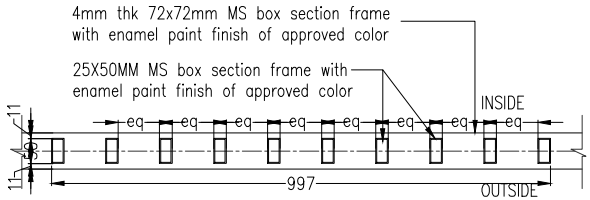

DETAIL AT "02"

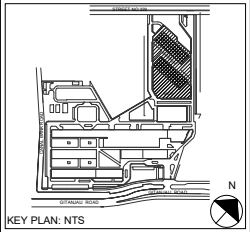

KEY PLAN: NTS

NOTE :
- ALL DIMENSIONS ARE IN MILLIMETERS - THIS DRAWING IS A COPYRIGHT AND PROPERTY OF THE RSP DESIGN CONSULTANTS (I) PVT. LTD, IS NOT TO BE PRODUCED, COPIED, HANDED OVER TO THIRD PARTY OR USED FOR ANY OTHER PURPOSE OTHER THAN FOR WHICH IT IS INTENDED.
- ALL DIMENSIONS SHALL BE VERIFIED ON SITE PRIOR TO START OF WORK ANY DISCREPANCY SHALL BE BROUGHT TO THE NOTICE OF THE RSP DESIGN CONSULTANTS (I) PVT LTD
- THIS PROJECT MANAGER/CONTRACTOR MUST CHECK ALL DIMENSIONS AND DETAILS AND BE RESPONSIBLE FOR THE SAME. ANY DISCREPANCY SHALL BE BROUGHT TO THE NOTICE OF RSP DESIGN CONSULTANTS (I) PVT LTD
- THIS DIMENSIONS IS TO BE READ AND NOT SCALED
- THIS DRAWING SHALL BE READ IN CONJUNCTION WITH ALL RELEVANT BUILDING SERVICES DRAWINGS AND SPECIFICATIONS AND ANY DISCREPANCY NOTICED SHALL BE BROUGHT TO THE ATTENTION OF THE CONSULTANTS WITHIN 7 WORKING DAYS OF RECEIPT OF THIS DRAWINGS, BUT ALWAYS PRIOR TO PROCUREMENT AND/OR EXECUTION OF WORKS
- DRAWING APPROVAL IS FOR THE CONFORMITY WITH OUTLINE DESIGN INTENT ONLY AND DOES NOT RELIEVE THE PROJECT MANAGERS / CONTRACTORS / SUB-CONTRACTORS OF THEIR RESPONSIBILITY FOR THE ACCURACY, INTEGRATION AND FITNESS FOR PURPOSE OF DESIGN
- PROJECT MANAGERS OF THE CONTRACTOR TO REVERT BACK WITHIN 7 WORKING DAYS OF RECEIPT OF THIS DRAWINGS ON COORDINATION AND BUILDABILITY ISSUES, IF OTHERWISE IT WOULD BE DEEMED THAT THEY HAVE UNDERSTOOD AND ACCEPTED THE DRAWING / DESIGN AND OWN FULL RESPONSIBILITY FOR THE WORKS CARRIED OUT ACCORDINGLY.

PROJECT ID: 20097	ORIENTATION :

PROJECT TITLE : SANCHAYITA PARK

PROPOSED OFFICE BUILDING FOR M/S. TATA CONSULTANCY SERVICES LIMITED.

CLIENT :
TATA CONSULTANCY SERVICES LIMITED
ITITES SEZ, Plot- IP / 3, Action Area - II, New Town, Rajarhat, Kolkata – 700156, West Bengal, India, Ph.- 033 66538781/Buzz- 4398781

PROJECT CONSULTANTS :
RSP DESIGN CONSULTANTS (INDIA) PVT LTD
RSP HOUSE, # 30, MUSEUM ROAD, BANGALORE - 560001 TEL: 25596868 FAX: 25596818

STRUCTURAL CONSULTANTS:
S.P.A. CONSULTANTS
34 ISABENCHAN DUTTA ROAD, KOLKATA - 700020, INDIA. TEL: 033-24855449 /24757614 24855448

MEP CONSULTANTS :
GRUNE DESIGNS
603, Lodha Supremus, Saki Vihar Road, Powai, Andheri (East), Mumbai – 400072 TEL: 25599868 FAX : 25599818

PROJECT MANAGEMENT CONSULTANTS :
TATA CONSULTING ENGINEERS LIMITED

SUBJECT OF DRAWING :
MAIN EXIT GATE DETAIL

FILE NAME :

SCALE : 1:600	DATE : 20 JUL 2021
DEALT : NB	CHECKED : RA

DRAWING NO: L-GF-4500 | REV NO: 00

A1 : 841MM X 594 MM