

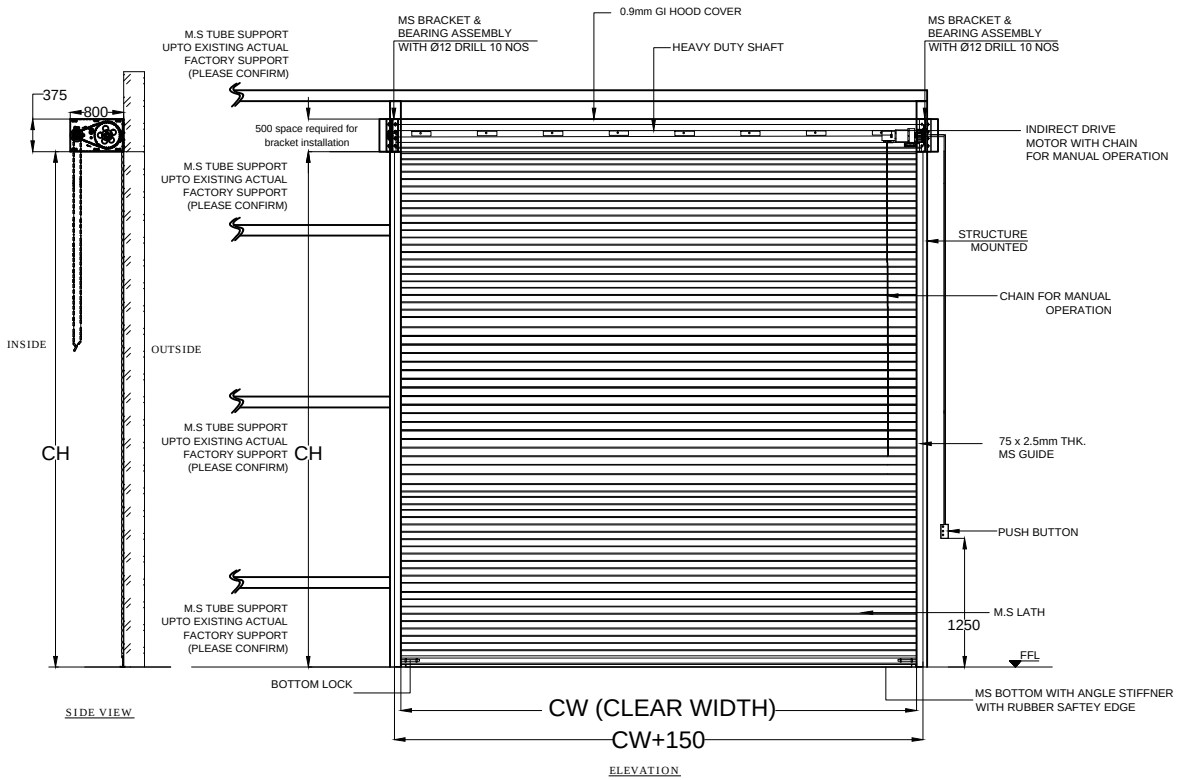



SIDE VIEW

ELEVATION

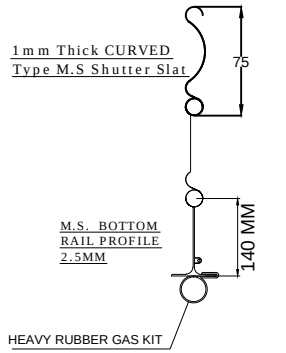

M.S. BOTTOM RAIL PROFILE 2.5MM

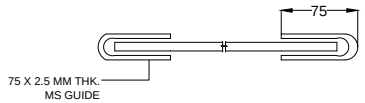

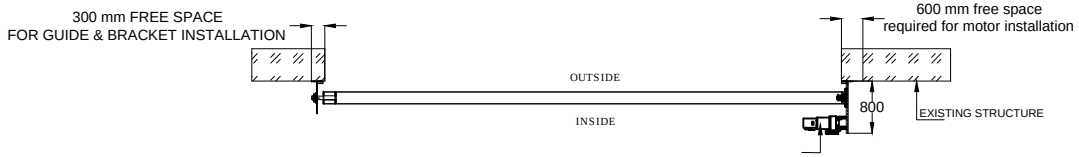

PLAN

TOLERANCE - ±5mm

REV NO	DATE	DRAWN	REMARK
R01	13.03.20	P.A	1. STRUCTURE DESIGN CHANGE

This drawing & design is the property of NIHVA TECHNOLOGIES. Not to be sold or copied to any other concern.

NOTE-
1. ALL CIVIL WORK & M.S STRUCTURE WILL BE CLIENT'S SCOPE.

S.NO	RAL CODE	COLOR	CLEAR WIDTH	CLEAR HEIGHT	QTY.	MOUNTING
01	RAL 9002 STD	WHITE GRAY	2500mm	2500mm	1 NO	STRUCTURE

TITLE
MOTORISED ROLLING SHUTTER

NIHVA TECHNOLOGIES PVT. LTD.
Website:- www.nihva.com
NIHVA TECHNOLOGIES PVT. LTD. PUNE
Tel : 020 66304033
Email:- info@nihva.com

	NAME	SIGN	DATE
DRAWN	P.A		12.02.2020
CHECK	G.J		12.02.2020
APPRD.			

CLIENT - MARS
PROJECT -
SITE LOCATION - KHED CITY
If any queries contact : design@nihva.com
DWG. NO. : NIHVA/19-20/0213/R01
REV- R01
ALL DIMENSION ARE IN mm
SCALE: NTS
WT:
SHEET: 01 OF 01