



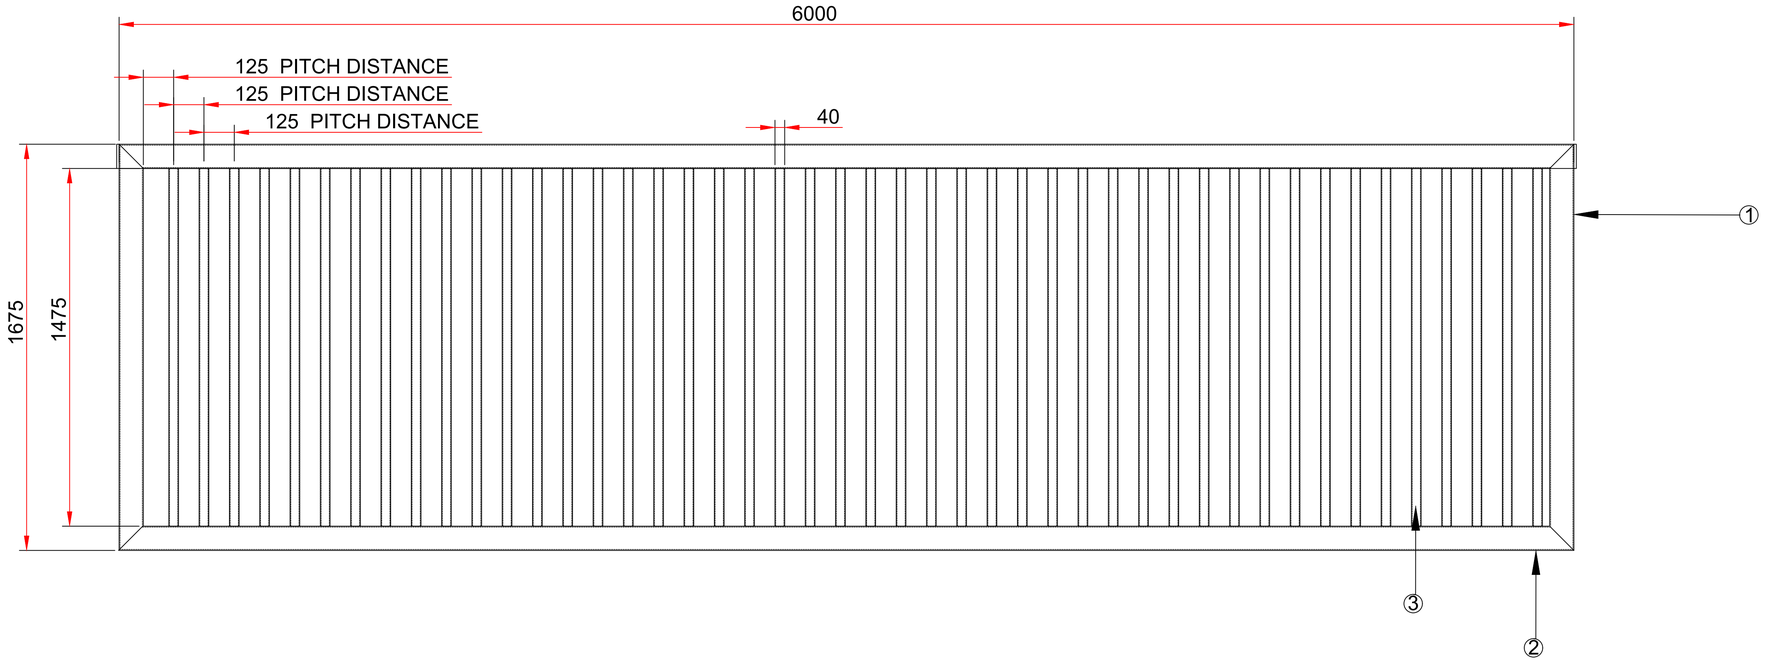

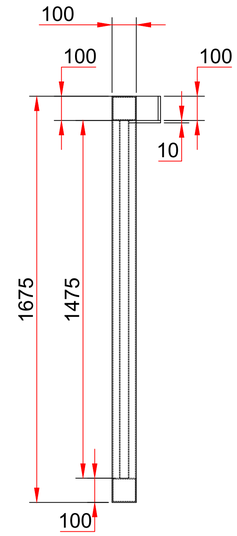

Note:-
1.All Dimension are in MM
2.Kindly Maintain the Given dimension

BOM FOR SINGLE LEAF

SL NO.	DESCRIPTION	SPECIFICATION	QTY
1	MS SQ. TUBE	100X100X5X1675 L	4 NOS
2	MS SQ. TUBE	100X100X5X6000 L	4 NOS
3	MS SQ. TUBE	40X40X3.2X1475 L	96 NOS
4	MS FLAT	100 X 10 X 180 L	4 NOS
5	MS FLAT	100 X 10 X 128 L	16 NOS
6	MS FLAT	100 X 10 X 6000 L	2 NOS
7			

Rev No.	Revision	Date	Revised By

QTY- 02 Nos

This drawing & design is the property of NIHVA TECHNOLOGIES. Not to be sold or copied to any other concern.

TITLE:- MASTER LEAF
TELE. SL. GATE

NIHVA TECHNOLOGIES PVT. LTD.

NIHVA TECHNOLOGIES PVT. LTD. PUNE
Tel : 020 66304033
Email:- info@nihva.com
Website:- www.nihva.com

	NAME	DATE	SIGN
DRAWN	MAHESH S.	12/08/2022	
CHECK	MAHESH S.	12/08/2022	
APPRD.	AMIT K.	12/08/2022	

CLIENT - NAVNEET EDUCATION LTD.
LOCATION - PALGHAR
PRODUCT - 3L-TELE. SL. GATE -16 MTR | QTY-00
If any queries contact : design@nihva.com | DWG NO:- NIHVA/22-23/0061 | REV-00
ALL DIMENSION ARE IN mm | SCALE: NTS | SCALE:-- 1:1 | SHEET: 01 OF 01