





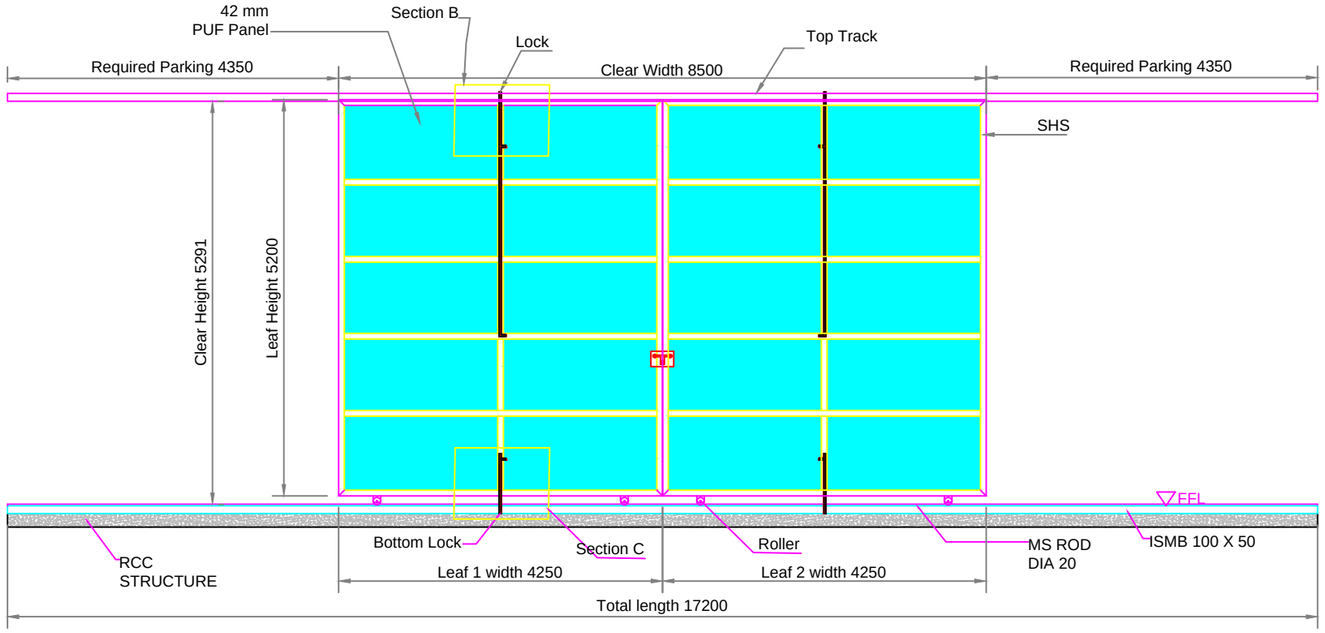

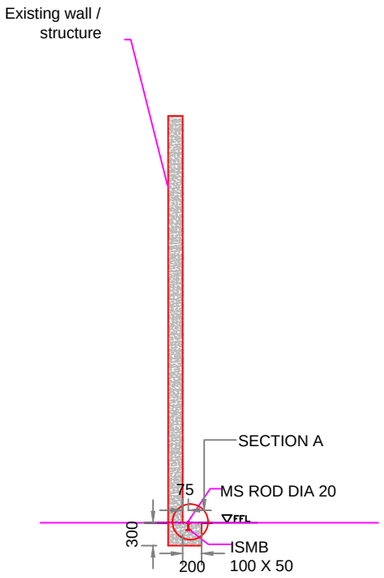

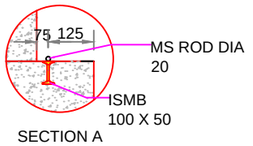

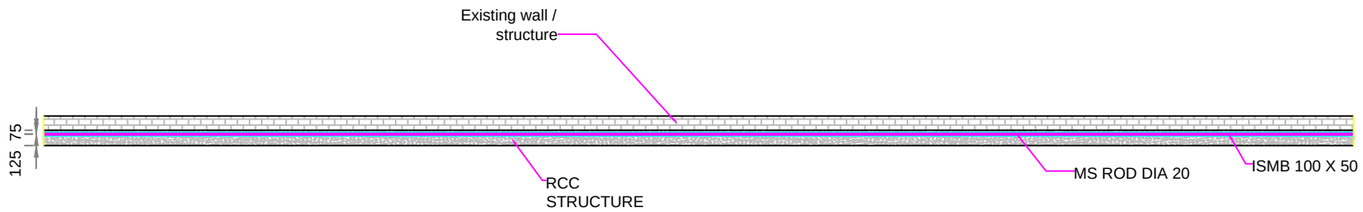

Technical Specs of Sliding Door

1. Parking length required - 4350mm on both sides
2. Bottom Rail - Bright bar Ø20mm
3. ISMB 100 X 50 positioned in the foundation.

Note-

1. All dimension are in mm.
2. All civil work is under client scope.

CLEAR WIDTH(DW)	CLEAR HEIGHT(DH)	QTY
8500mm	5200mm	15 NO

This drawing & design is the property of NIHVA TECHNOLOGIES. Not to be sold or copied to any other concern.

TITLE	SLIDING DOOR WITH FOUNDATION		
	NAME	SIGN	DATE
DRAWN	G.P.		11.11.21
CHECK	A.K.		11.11.21
If any queries contact : design@nihva.com			
ALL DIMENSION ARE IN mm			

NIHVA TECHNOLOGIES PVT. LTD.
NIHVA TECHNOLOGIES PVT. LTD. PUNE
Tel : 020 66304033
Email:- info@nihva.com
Website:- www.nihva.com

CLIENT :- Lestech Engineering India Pvt. Ltd.

PROJECT :- POSCO

LOCATION :- Mangaon

DWG. NO. :- NIHVA/21-22/0262 | REV:- R00

SCALE:NTS | WT: | SHEET:02 OF 02