
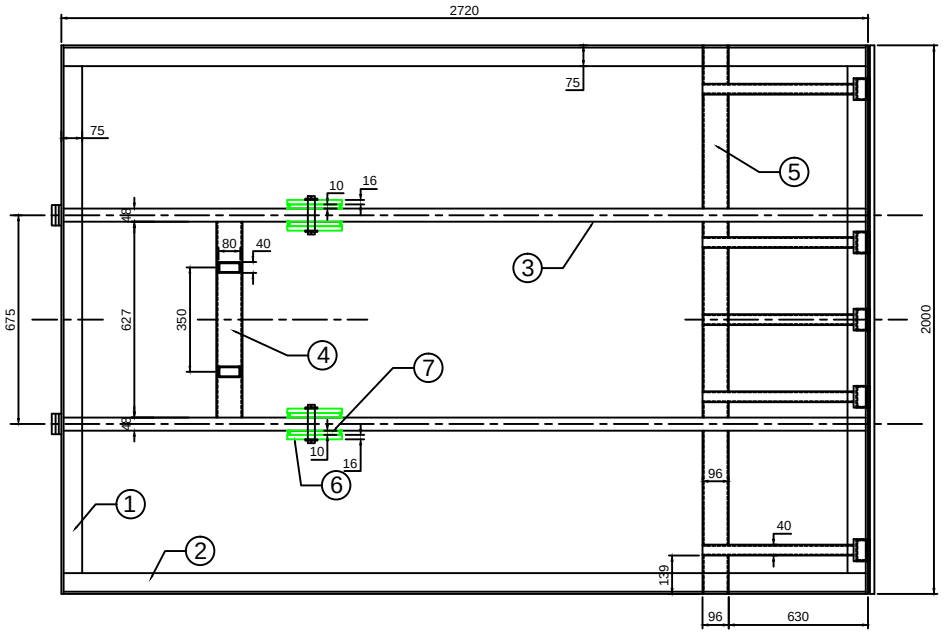


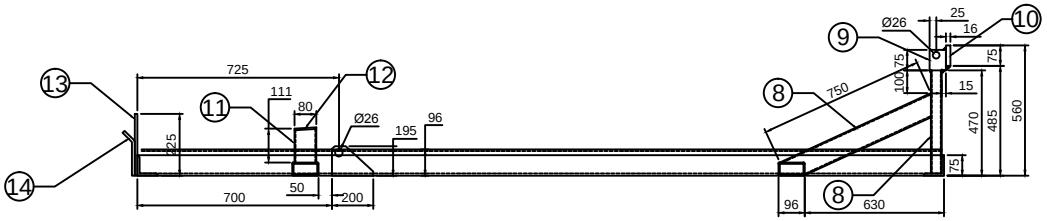

NOTE:~ MTL : MS

PART NO.	PART NAME	DESCRIPTION	QTY
1.	ISA	75 X 75 X 8 X 2000L (NOTCH)	2 NOS
2.	ISA	75 X 75 X 8 X 2704L	2 NOS
3.	R.TUBE	96 X 48 X 4.8 THK X 2704L (NOTCH)	2 NOS
4.	R.TUBE	96 X 48 X 4.8 THK X 627L	2 NOS
5.	R.TUBE	96 X 48 X 4.8 THK X 630L	2 NOS
6.	PROFILE	200 X 16 THK X 195L	4 NOS
7.	FLAT	75 X 10 X 150L PACKING	4 NOS
8.	R.TUBE	80 X 40 X 4 THK X 750L (NOTCH)	5 NOS
9.	SOLID	75 X 60 X 80L	5 NOS
10.	FLAT	75 X 16 X 2000L	1 NOS
11.	R.TUBE	80 X 40 X 4 THK X 128L	2 NOS
12.	FLAT	40 X 5 X 80L	2 NOS
13.	FLAT	75 X 10 X 225L	2 NOS
14.	FLAT	75 X 10 X 200L	2 NOS
15.			
16.			

This drawing & design is the property of NIHVA TECHNOLOGIES. Not to be sold or copied to any other concern.

TITLE

BASE FRAME ASSLY

NIHVA TECHNOLOGIES PVT. LTD.

NIHVA TECHNOLOGIES PVT. LTD. PUNE
Tel : 020 66304033
Email:- info@nihva.com
Website:- www.nihva.com

	NAME	SIGN	DATE
DRAWN	PRADEEP		05.09.2018
CHECK	PRADEEP		05.09.2018
APPRD.	PRADEEP		05.09.2018

If any queries contact : design@nihva.com

ALL DIMENSION ARE IN mm

CLIENT -

PROJECT - NDL 385 & 386

SITE LOCATION -

DWG. NO. : NIHVA/18-19/MFG/NDL385&386/005

SCALE: NTS | WT: | REV- 00