


DWG.NO: ----

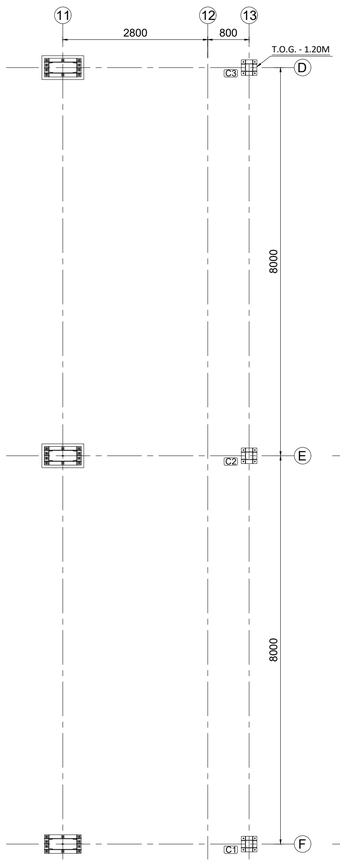


PLAN FOR BASE PLATE

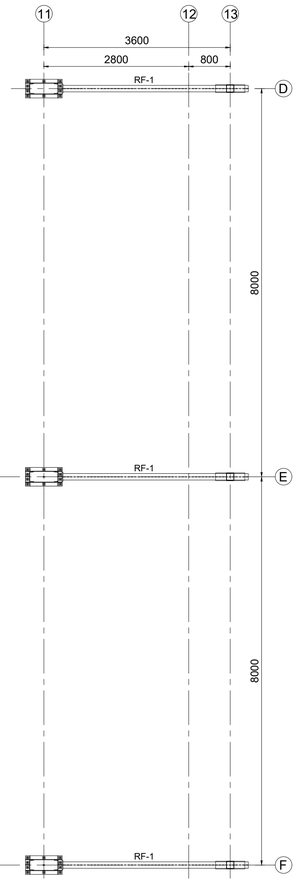


PLAN FOR RAFTER (EL+ 2.40m) LEVEL

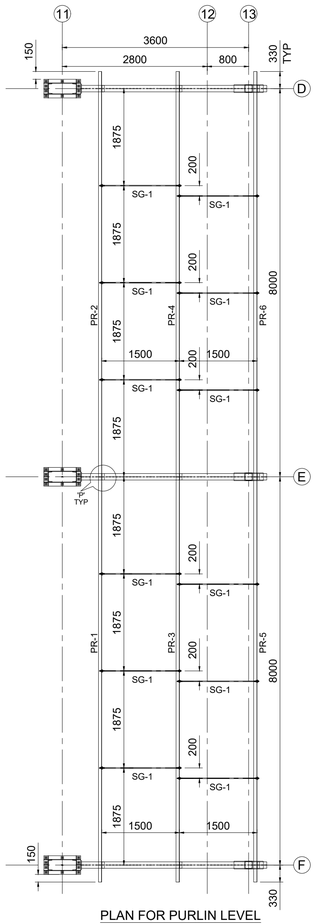


PLAN FOR PURLIN LEVEL

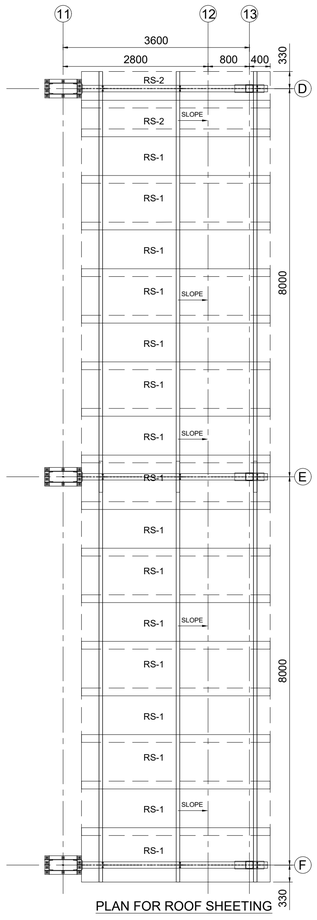


PLAN FOR ROOF SHEETING

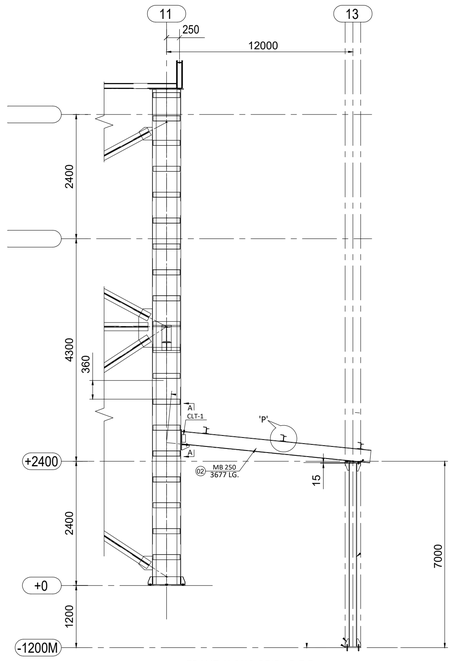


FRAME ALONG GRID - D,E,F

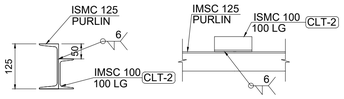


'C' PURLIN(ISMC 125) PURLIN CLEAT DETAILS
TYP. DETAIL AT 'P'

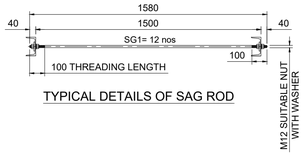


TYPICAL DETAILS OF SAG ROD

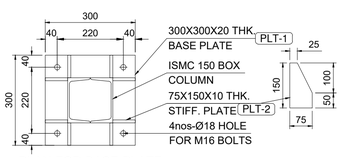

PLAN FOR BASE PLATE
(FOR COL. C1 TO C3)

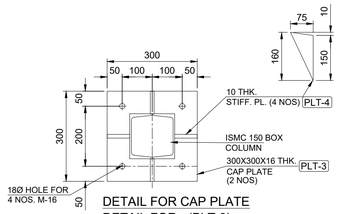

DETAIL FOR CAP PLATE
DETAIL FOR - (PLT-3)

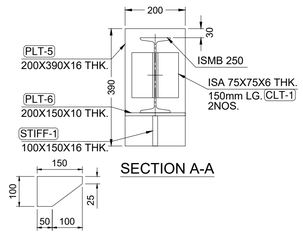



SECTION A-A

LENGTH	
WIDTH	RS


SHEET QTY.			
ERECN. MKD.	SUPPLY WIDTH	LENGTH	QTY.
RS1	1050	3700	16
RS2	705	3700	2

RS=COLOURE COATED ROOF SHEET
0.5mm THK.

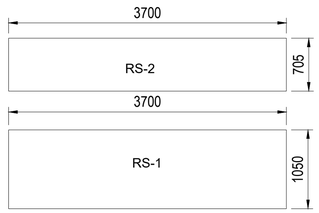


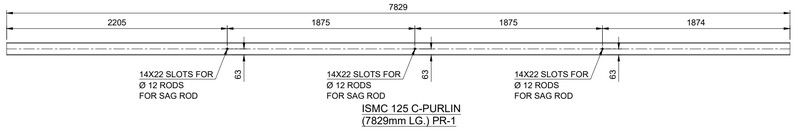


ISMC 125 C-PURLIN
(7829mm LG.) PR-1

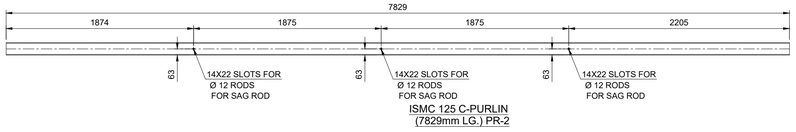


ISMC 125 C-PURLIN
(7829mm LG.) PR-2

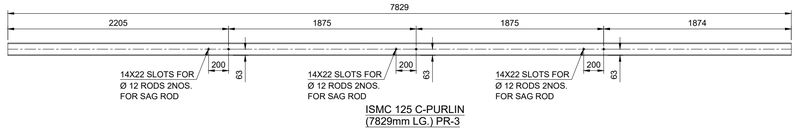


ISMC 125 C-PURLIN
(7829mm LG.) PR-3

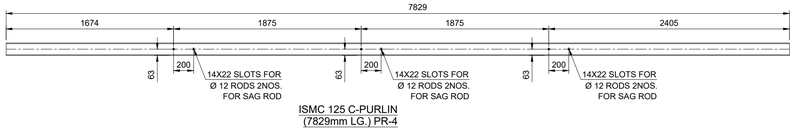

ISMC 125 C-PURLIN
(7829mm LG.) PR-4

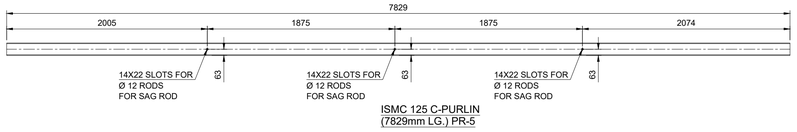

ISMC 125 C-PURLIN
(7829mm LG.) PR-5

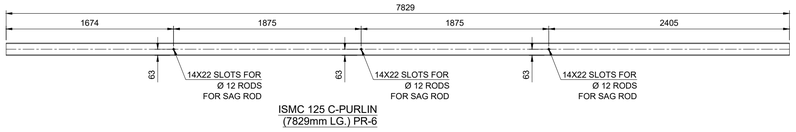

ISMC 125 C-PURLIN
(7829mm LG.) PR-6

GENERAL NOTES :-

1. ALL DIMENSIONS ARE IN MM & LEVEL ARE IN METER.
2. ALL STRUCTURAL STEEL AS PER IS:2062.
3. PROVIDE WELDING AS PER IS:816.
4. PROVIDE MIN. 6MM WELD WITH MIN. WELD LENGTH OF 150MM.
5. USE ELECTRODS AS PER IS:814 (PT.-I).
6. FILLET/ BUTT WELD SHALL BE OF 6MM SIZE AND SHALL BE CONTINUOUS.
7. FABRICATION AND ERECTION SHALL BE AS PER IS:800 AND IS:803.
8. WELD SHALL BE GROUND SMOOTH.
9. ALL GUSSET PLATES SHALL BE MIN. 10 THK.
10. ALL M.S. BLACK BOLTS AND NUTS SHALL CONFORM TO IS:1363(PT. 1 TO 3).
11. STRUCTURE SHALL BE APPLIED WITH ONE COAT OF RED OXIDE ZINC CROMATE PRIMER AFTER FABRICATION FOLLOWED ONE MORE COAT BEFORE ERECTION. FINALLY APPLY 2 COATS OF SYNTHETIC ENAMAL OF APPROVED QUALITY.

REV.NO.	DESCRIPTION.	DATE	DRAWN.	CHKD.	APPD.
R0	ISSUED FOR EXECUTION	17.09.2022	CDD	RRK	HAB

DWG.TITLE :- FABRICATION DRAWING FOR LEAN HED

PROJECT	
CLIENT	VEDANTA
NIHVA	NIHVA TECHNOLOGIES PVT LTD. PLOT NO 187, 1ST FLOOR, G BLOCK, THERMAX CHOWK, PIMPRI CHINCWAD, MH

DRAWN : CDD	CHECKED : RRK	SCALE: 1:50
APPROVED : HAB	-	DATE: 31.05.2023
DWG.NO: ---	(SH-1OF1)	REV. - R0 SIZE. - A1

A1 [841X594]