




GROUND FLOOR ISOMETRIC VIEW

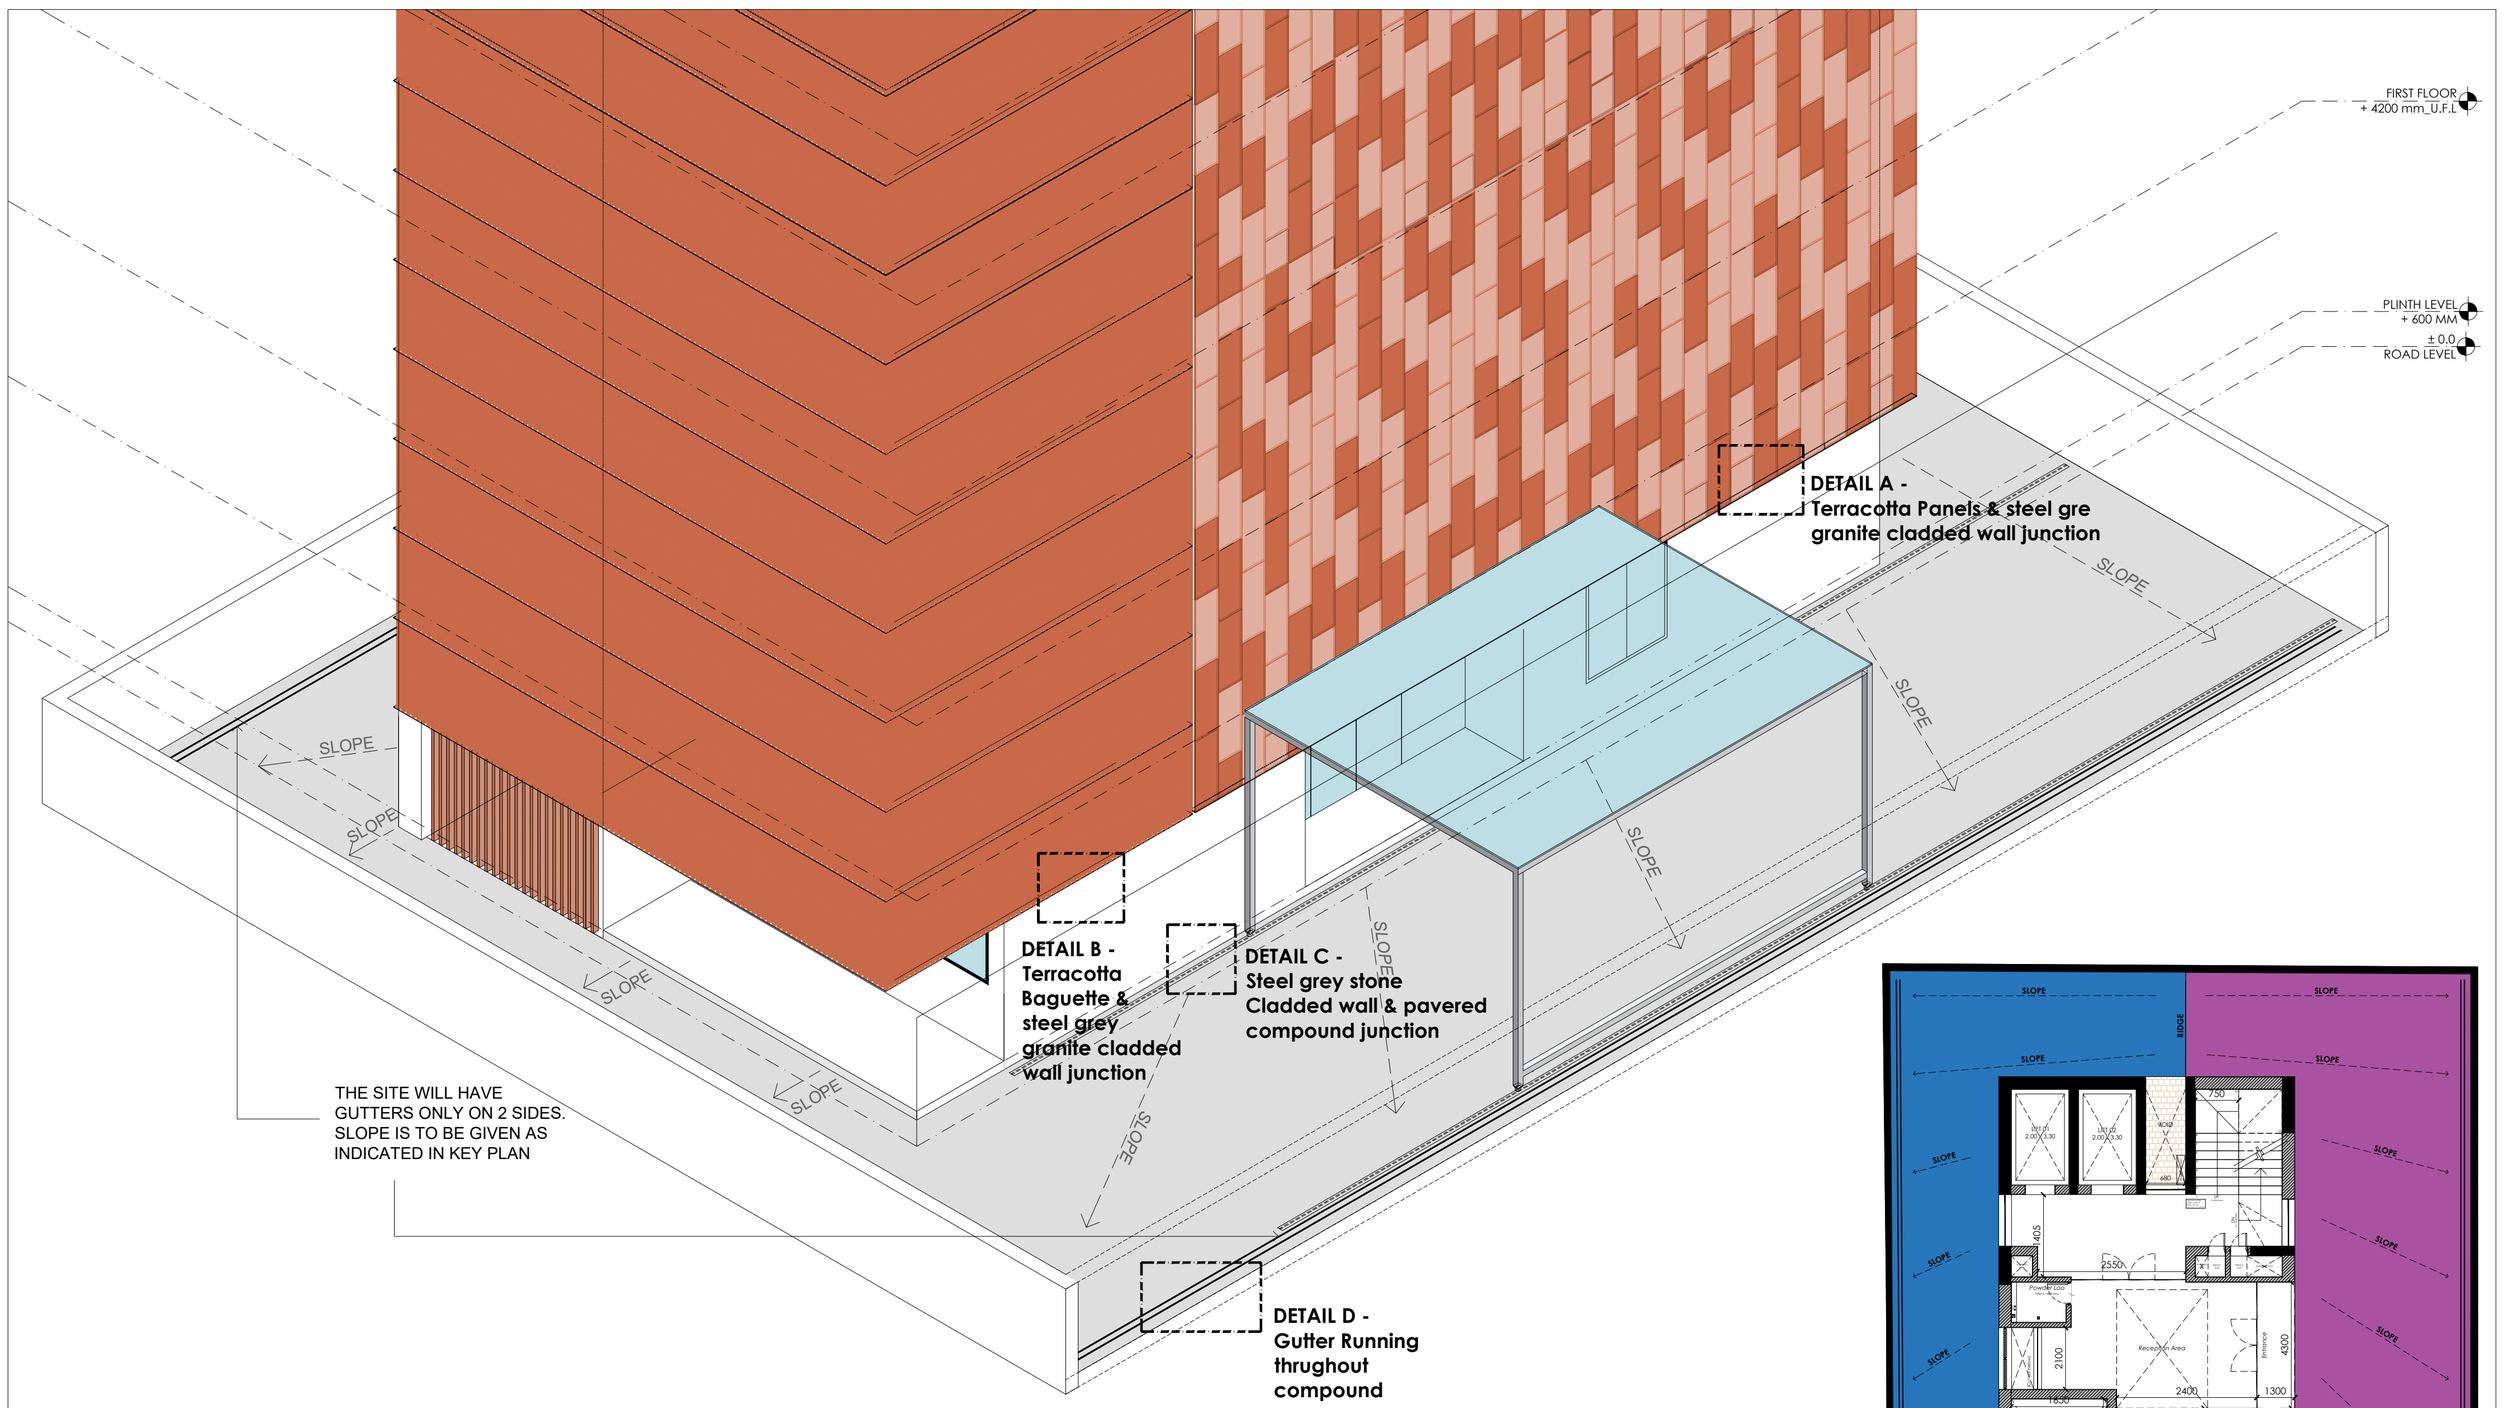


GROUND FLOOR KEY PLAN INDICATING SLOPE

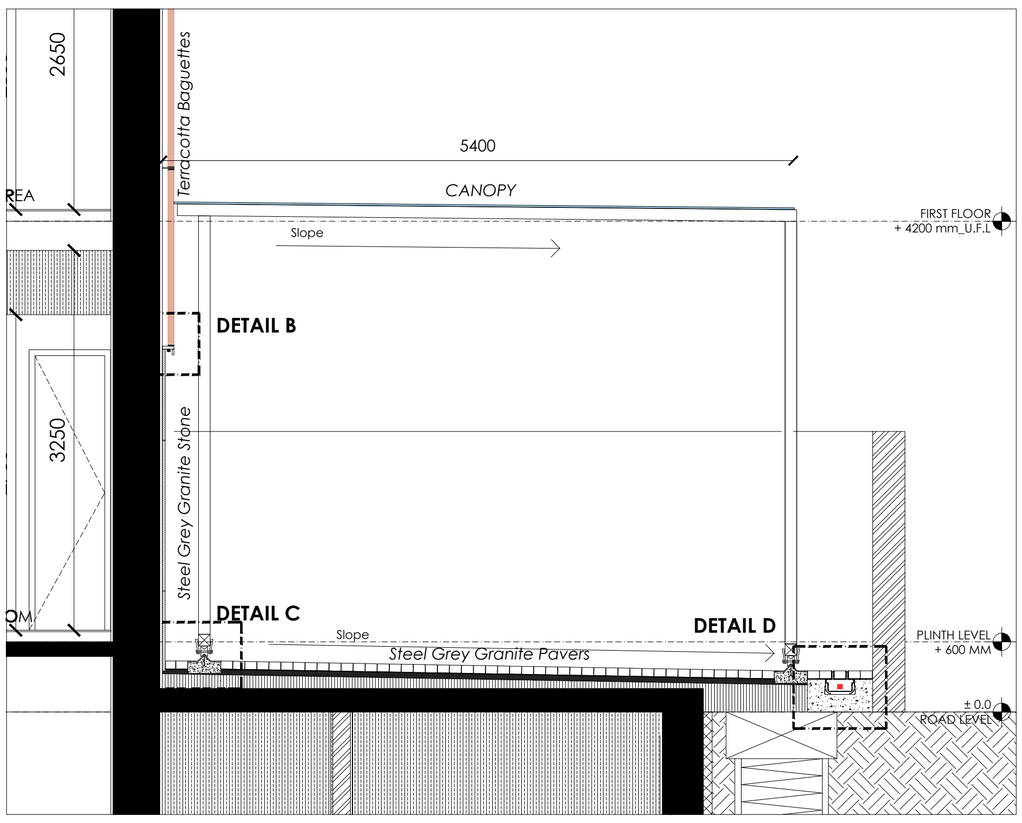


SECTION A-A'

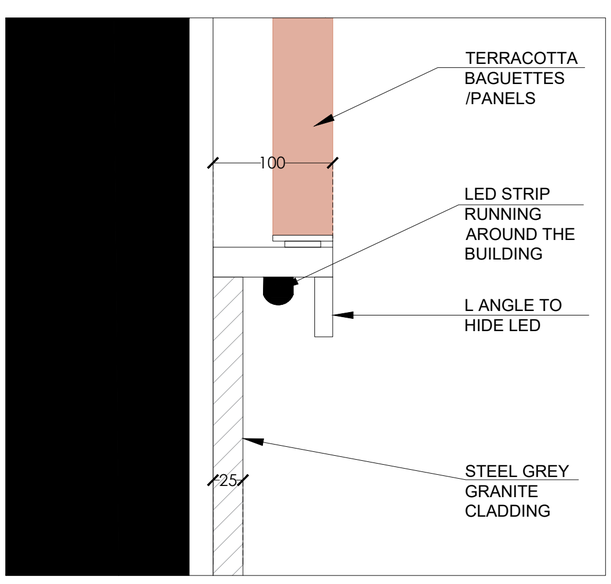


DETAIL AT 'B' (need to modify this detail as per the site condition)

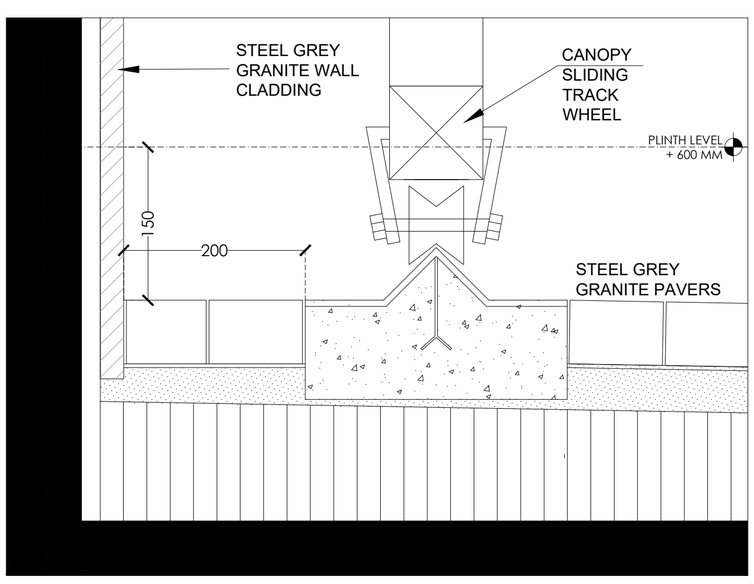

DETAIL AT 'C'

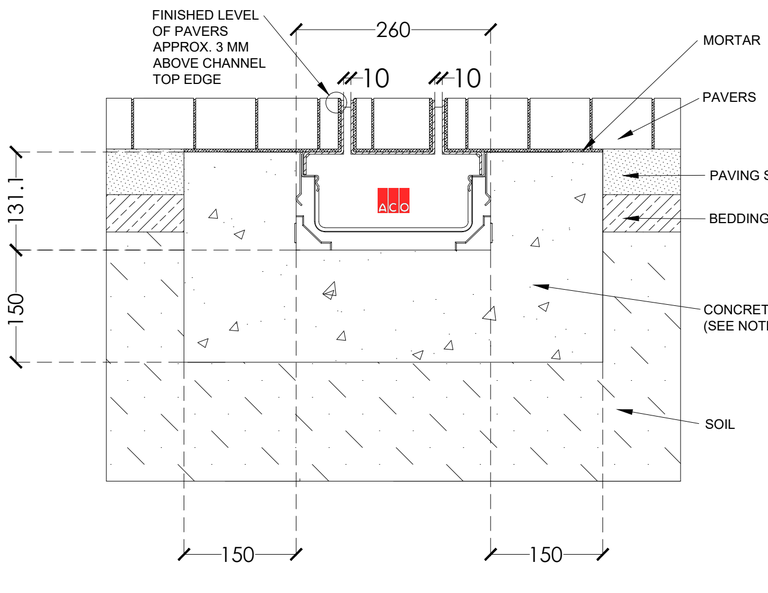

DETAIL D (OPTION 1) - ACO GUTTER TWINSLOT 200 WITH H200KS CHANNEL- 8,000KG WHEEL LOAD

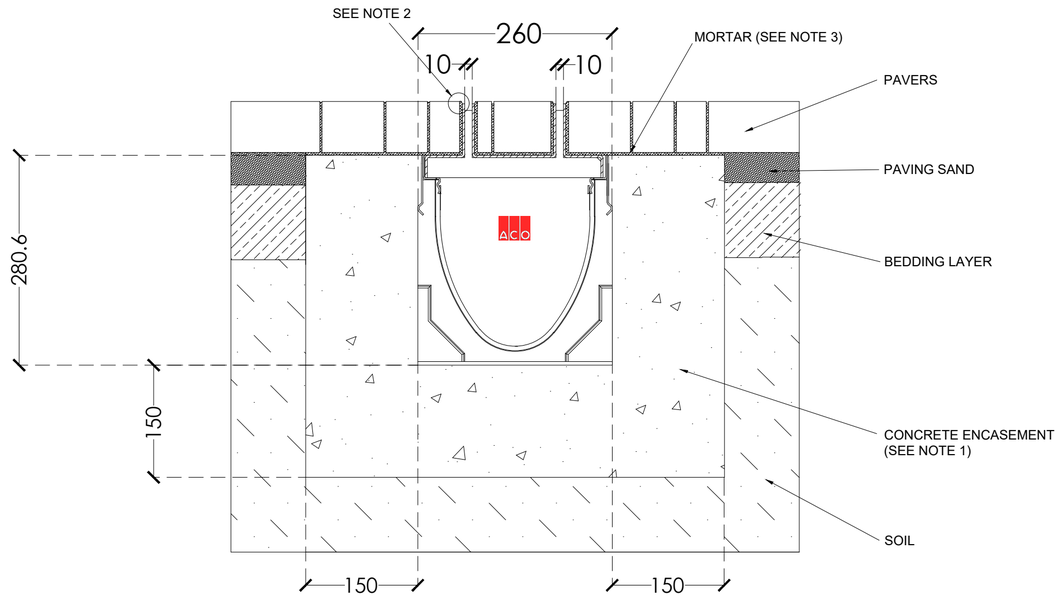

DETAIL D (OPTION 2) - ACO GUTTER TWINSLOT 200 WITH KS200 CHANNEL- 8,000KG WHEEL LOAD

LOCATION	DRAWING NO.
Matunga, Mumbai	

REVISIONS

Sr. no.	Date	Description
R0	14-11-2022	---

NOTE :

1. **Do not scale the drawings. For any discrepancy in the measurements, please refer to the Architect.**
2. **For all the structural details, kindly refer to structural consultant's details and drawings**
3. **Existing Road Level (E.R.L) is considered as ± 0.0 lvl. All reference here are considered from this level.**

LEGEND

Project Title : ***Terra Tower_House for Society Tea***

Drawing Title : ***GROUND FLOOR GUTTER AND LIGHT DETAILS***

Drawing No : ---

Drawing Status : For reference

Revision number : R0

Scale : 1: 100 (A1 size)

Date : 14.11.2021

Drawn By : Madhura K.

Checked By : Aishwarya K.

SPASM DESIGN
ARCHITECTS