




DRAWING

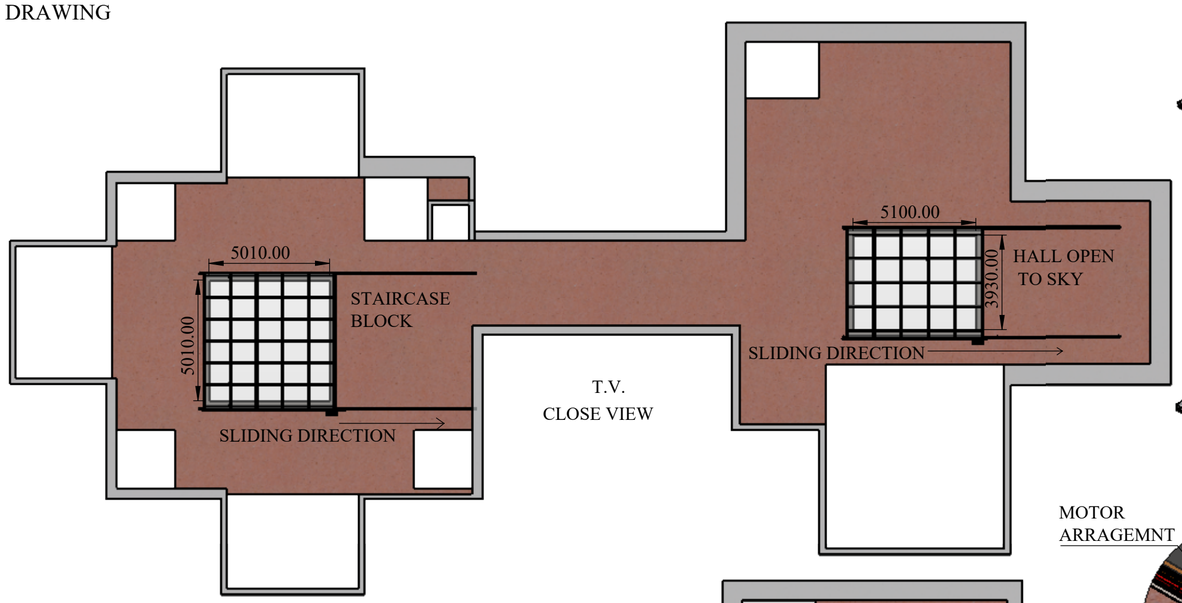

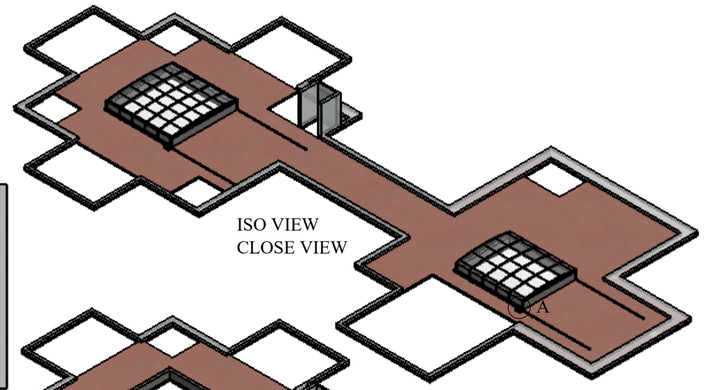


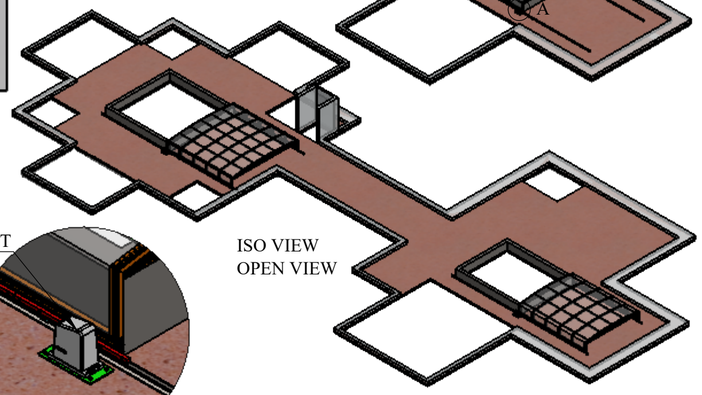

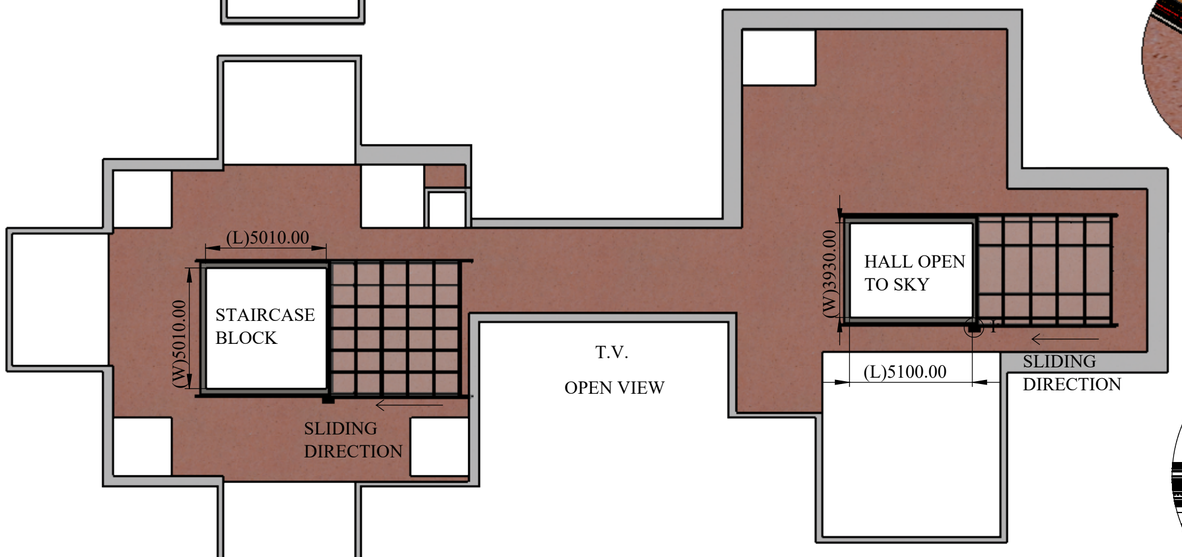


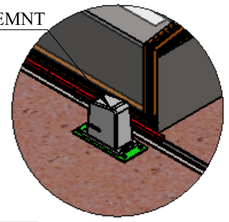


DETAIL A
SCALE 1 : 27

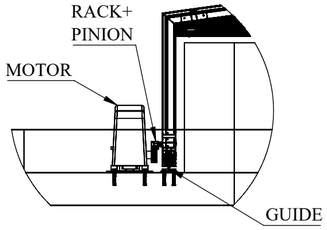


DETAIL B
SCALE 1 : 20

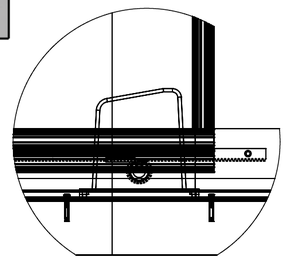


DETAIL C
SCALE 1 : 12

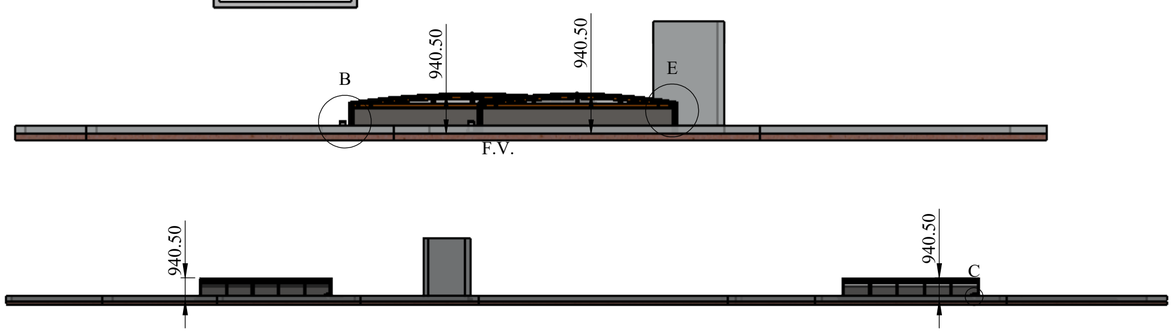

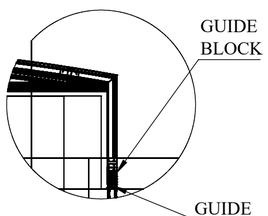

DETAIL E
SCALE 1 : 28

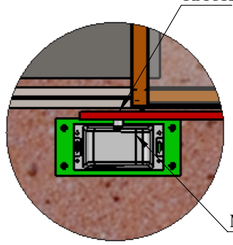

DETAIL I
SCALE 1 : 16

MOTOR ARRAGEMENT

REV DESCRIPTION	DATE	REV NO
	29-10-2026	REV 00
1.		

NOTE :
GA DRAWING

SPECIAL INSTRUCTION'S :

This drawing & design is the property of NIHVA TECHONOLOGIES PVT. LTD. Not to be sold or copied to any other concern

TITLE - ROOF AUTOMATION


DWG NO - NTPL-

NIHVA TECHNOLOGIES PVT.LTD.PUNE
Website - www.nihva.com

	NAME	SIGNATURE	DATE
DRAWN	V.W.		29-10-2026
CHK'D	S.P.		30-10-2026
APPV'D	V.T.		30-10-2026

PRODUCT - MOTORISED C SHAPE RETRACTABLE ROOF
CLIENT NAME - JAYANT DAVE.
SITE LOCATION - BHUGAON, PUNE.
MATRIAL -
QTY - 1
If any queries contact - info@nihva.com
PROJECTION METHOD:
SCALE :
ALL DIMENSION ARE IN mm
A2


DRAWING

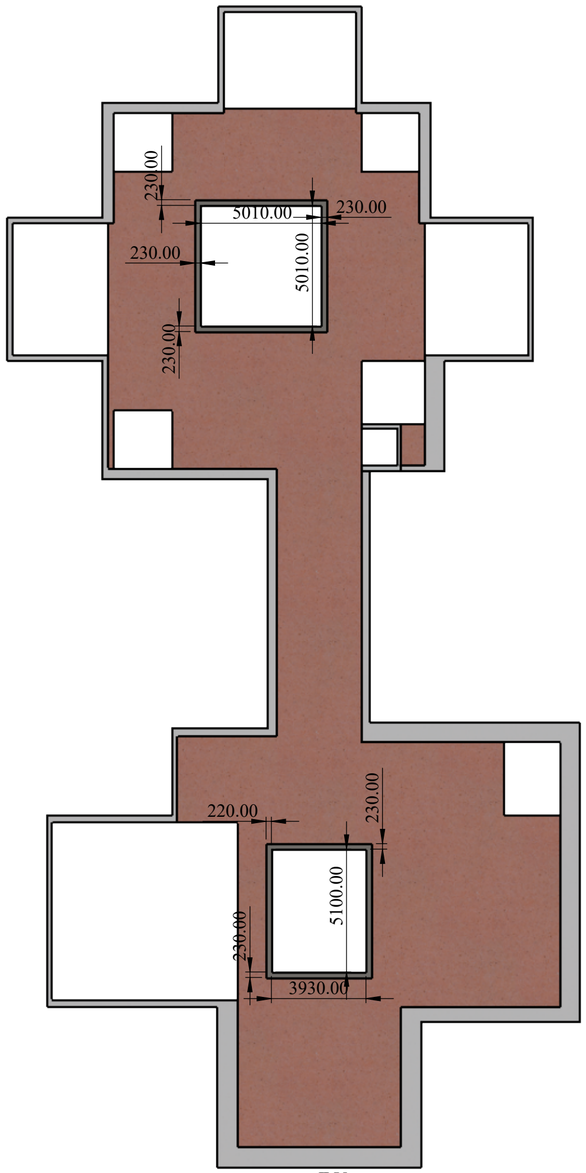

T.V.



F.V.

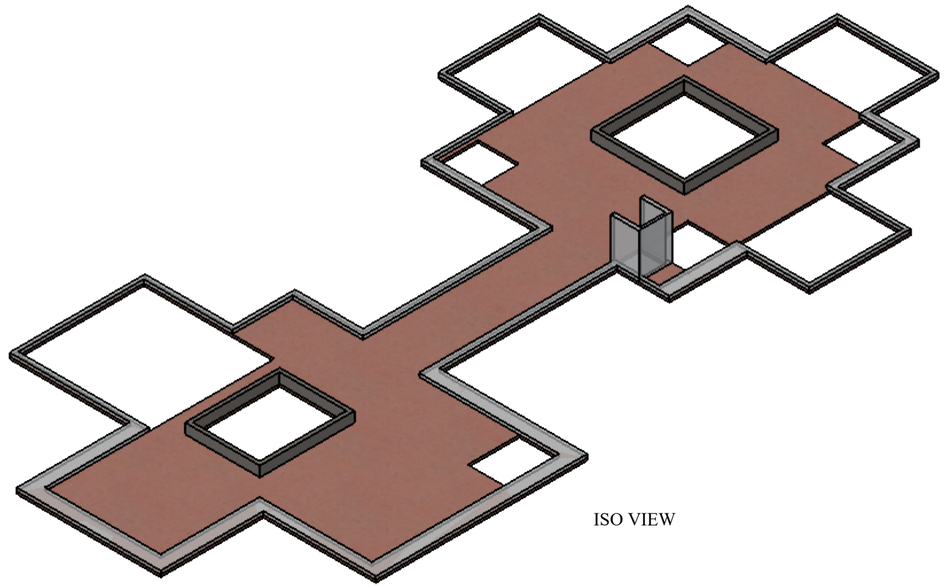

ISO VIEW



S.V.

REV DESCRIPTION	DATE	REV NO
	29-10-2026	REV 00
1.		

NOTE :

CIVIL DRAWING
BASE STRUCTURE IN CLIENT SCOPE

SPECIAL INSTRUCTION'S :

This drawing & design is the property of NIHVA TECHONOLOGIES PVT. LTD. Not to be sold or copied to any other concern

TITLE - ROOF AUTOMATION

DWG NO - NTPL-

NIHVA TECHNOLOGIES PVT.LTD.PUNE
Website - www.nihva.com

	NAME	SIGNATURE	DATE
DRAWN	V.W.		29-10-2026
CHK'D	S.P.		30-10-2026
APPV'D	V.T.		30-10-2026

PRODUCT - MOTORISED C SHAPE RETRACTABLE ROOF
CLIENT NAME - JAYANT DAVE.
SITE LOCATION - BHUGAON, PUNE.
MATRIAL - QTY - 1
If any queries contact - info@nihva.com
PROJECTION METHOD:
SCALE :
ALL DIMENSION ARE IN mm A2
SHEET 2 OF 2