



SECTION 02
SCALE 1:40


SECTION 01
SCALE 1:40

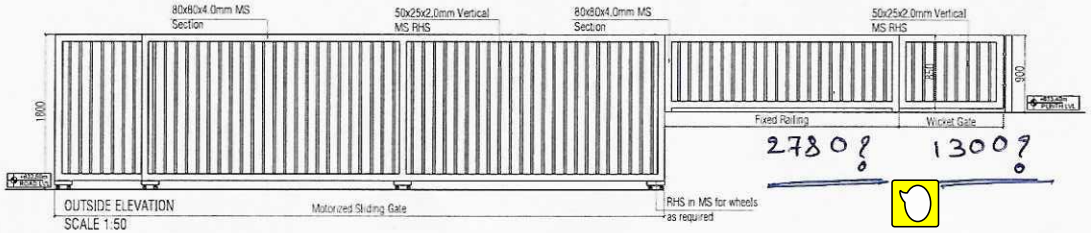

OUTSIDE ELEVATION
SCALE 1:50

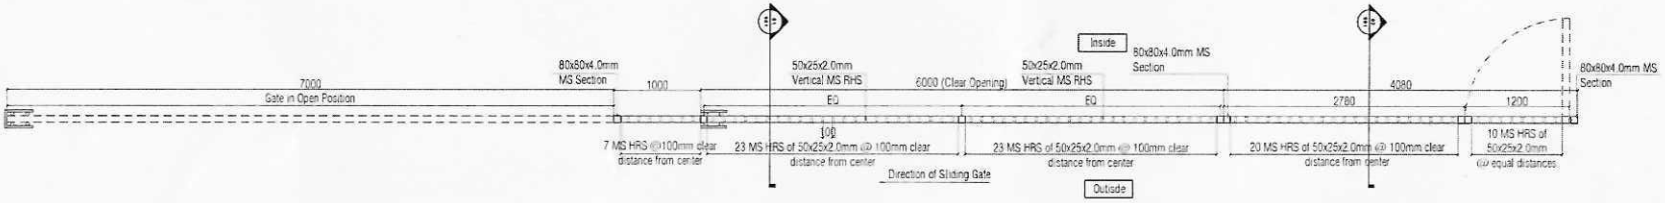


ENTRY 1- GATE 1
PLAN
SCALE 1:40

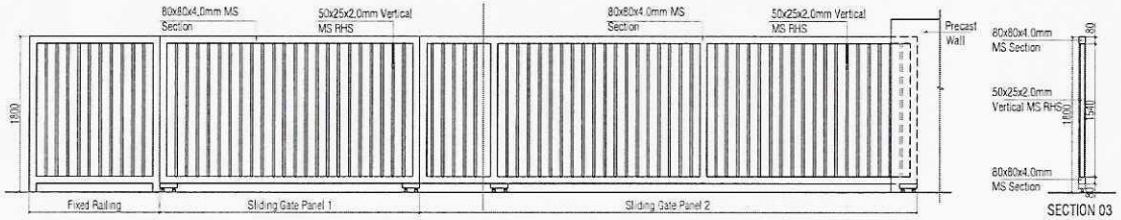


OUTSIDE ELEVATION
SCALE 1:40

SECTION 03
SCALE 1:40

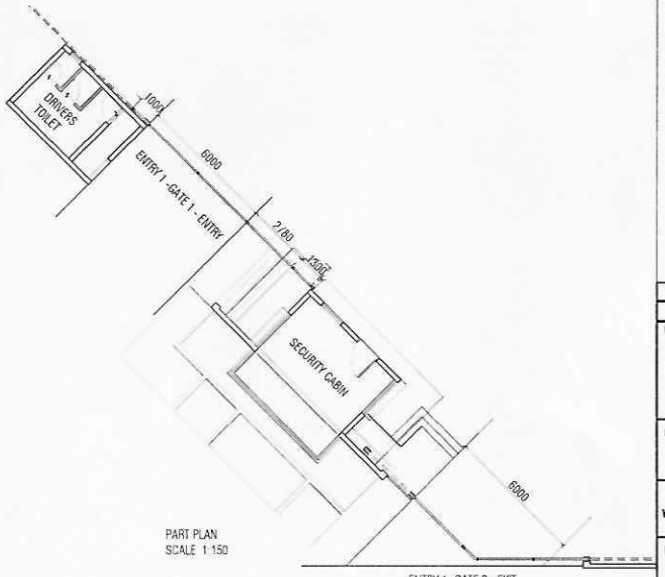

PART PLAN
SCALE 1:150

ENTRY 1 -GATE 2 - EXIT

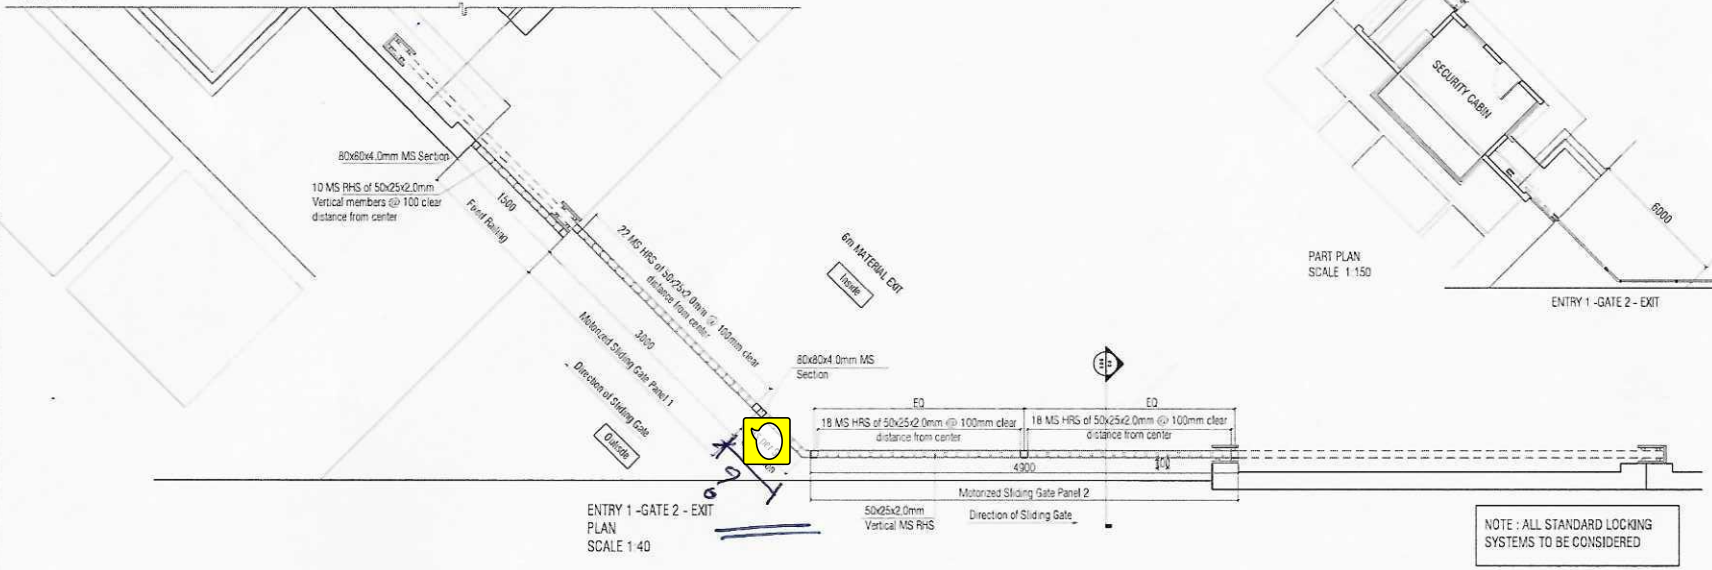


ENTRY 1 -GATE 2 - EXIT
PLAN
SCALE 1:40

NOTE : ALL STANDARD LOCKING SYSTEMS TO BE CONSIDERED

MASTER PLAN- GATE -1 and 2

NOTES :

1. ALL DIMENSIONS ARE IN MM UNLESS OTHERWISE MENTIONED
2. ONLY WRITTEN DIMENSIONS SHALL BE FOLLOWED
3. DIMENSIONS SHALL BE CHECKED AND CORRELATED WITH STRUCTURAL DRAWINGS
4. LARGER SCALED DRAWINGS SUPERSEDE SMALLER SCALED DRAWINGS
5. ANY DISCREPANCY IN THE DRAWING SHALL BE IMMEDIATELY BROUGHT TO THE NOTICE OF THE ARCHITECT
6. NO WORK ON SITE SHALL PROCEED WITHOUT THE APPROVAL OF **FOURTH DIMENSION ARCHITECTS PVT. LTD**
7. THIS DRAWING IS THE SOLE PROPERTY OF **FOURTH DIMENSION ARCHITECTS PVT. LTD** AND IS NOT TO BE REPRODUCED OR COPIED IN PART OR WHOLE IN ANY FORM AND ON COMPLETION OF PROJECT SHALL BE RETURNED TO ARCHITECS
8. THIS DRAWING CONTAINS COPYRIGHT MATERIAL AND TRADE SECRET INFORMATION BELONGING TO **FOURTH DIMENSION ARCHITECTS PVT LTD** AND ITS CLIENT AS NOTED ABOVE
9. ANY UNAUTHORIZED USE DISCLOSURE DISSEMINATION OR DUPLICATION OF ANY OF THE INFORMATION CONTAINED HEREIN MAY RESULT IN LIABILITY UNDER APPLICABLE LAW.

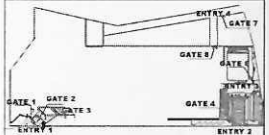

KEY PLAN

NO	REVISION	DATE

LEGEND :

PROJECT :
PROPOSED PLANT FOR WILO MATHER & PLATT Pumps Pvt. Ltd. LIMITED, AT CHORDIA INDUSTRIAL PARK, SHIRWAL, SATARA.

CLIENT :
WILO MATHER & PLATT Pumps Pvt. Ltd.

FOURTH DIMENSION ARCHITECTS PVT. LTD.
ARCHITECTS PLANNERS INTERIOR LANDSCAPE DESIGNERS & LEGAL CONSULTANTS
FD House Lane no 8, Opposite Axis Bank, Prabhat Road, Deccan Gymkhana, Pune-411 004. Ph. +91-20-41 000 999. Fax. +91-20-41 000 888

SIGN AND SEAL :

TITLE : ENTRY 1 - GATE 1 AND 2 DETAILS

DRAWING STATUS :	GOOD FOR CONSTRUCTION
DATE	11/03/2022
SCALE	1:40 @ A2
JOB NO.	W-IND-0320
DRAWN BY	SANSKRUTI S.
CHECK BY	KAVITA
DRAWING NO :	**SG-A-901**
REVISION NO :	R0

NORTH
N