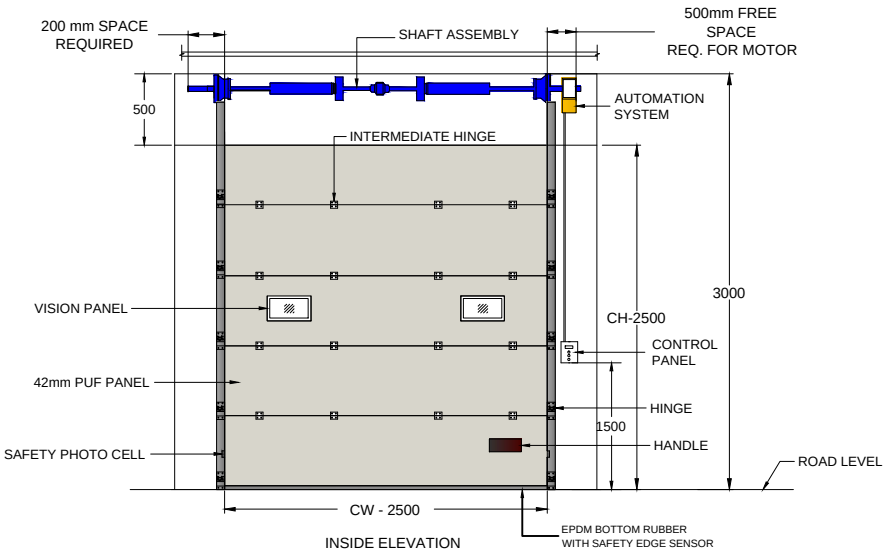

INSIDE ELEVATION

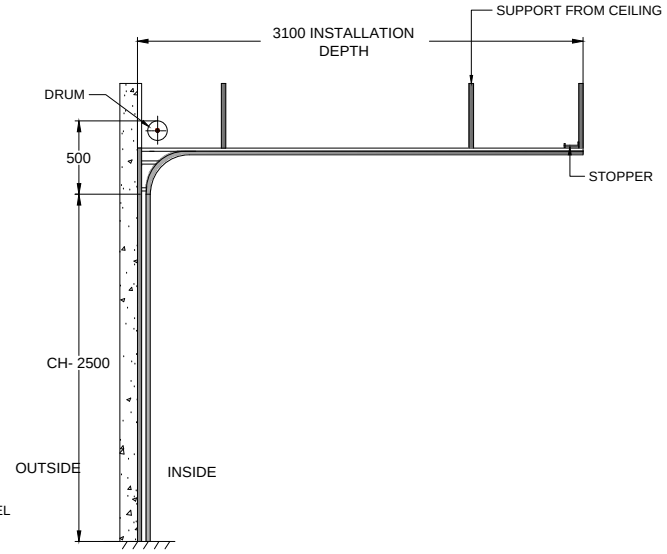

SIDE VIEW

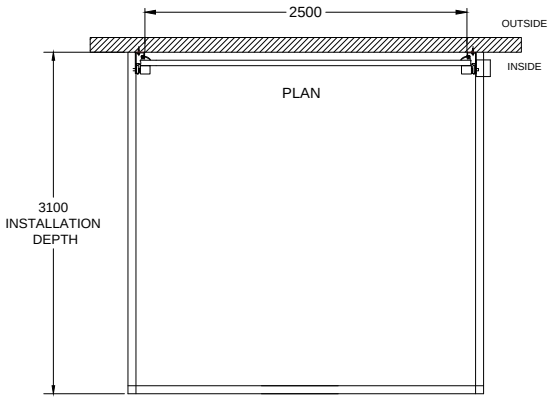

PLAN

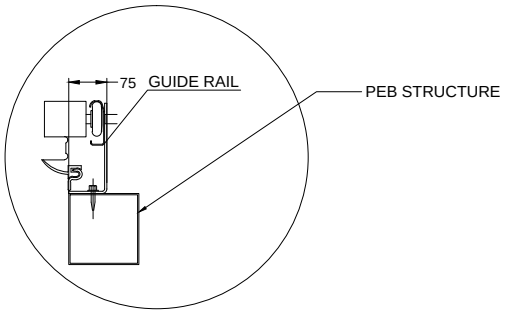

TRACK DETAILS

DIMENSION :

CLEAR WIDTH	CLEAR HEIGHT	QUANTITY
2500 mm	2500 mm	02 NOS

TECHNICAL DATA :

COMPONENTS	MATERIALS	SPECIFICATIONS
DOOR PANELS	GI & PUF	42mm CFC- FREE POLYURETHANE WITH 0.5mm THK, GI PRECOATED PANELS.
DOOR HINGE	———	HEAVY DUTY HINGES FOR INTERLOCKING OF PANELS
SHAFT ASSEMBLY	STD.	TORSIONAL SPRING WITH SHAFT & BEARING PLATES
FINISH		GREY WHITE RAL 9002

ACCESSORIES-

IMPORTANT NOTES:

1.SINGLE PHASE POWER SUPPLY REQUIRED AT DOOR LOCATION.
2.ALL CIVIL WORK SHALL BE CLIENT'S SCOPE.

D:\NIHVA LOGO.png

NIHVA TECHNOLOGIES PVT. LTD. PUNE
Email:- info@nihva.com
Website:- www.nihva.com

TITLE:

SECTIONAL DOOR SL (MOTORIZED)

CLIENT'S APPROVAL :

CLIENT - GLENMARK

PROJECT -GLENMARK

SITE LOCATION - GOA.

DWG. NO. : NIHVA/17-18/0300		REV- 0
SCALE: NTS	WT:	SHEET:1 OF 1
DRAWN BY: SURAJ		DATE: 05-12-2017
CHECK BY: OMKAR		DATE: 05-12-2017
APPROVED BY: SHEKHAR		DATE: 05-12-2017

If any queries contact : design@nihva.com

NOTE: ALL DIMENSIONS ARE IN mm

THIS DRAWING & DESIGNING IS THE PROPERTY OF NIHVA TECHNOLOGIES. NOT TO BE SOLD OR COPIED TO ANY OTHER CONCERN.