
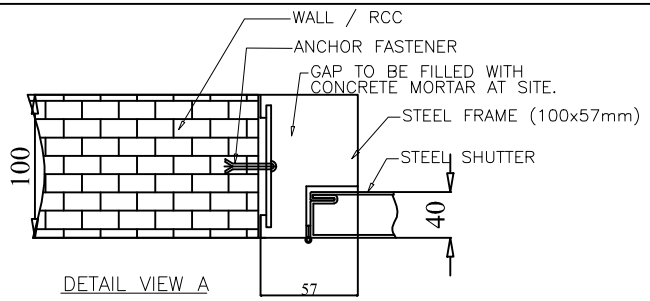


DETAIL VIEW A

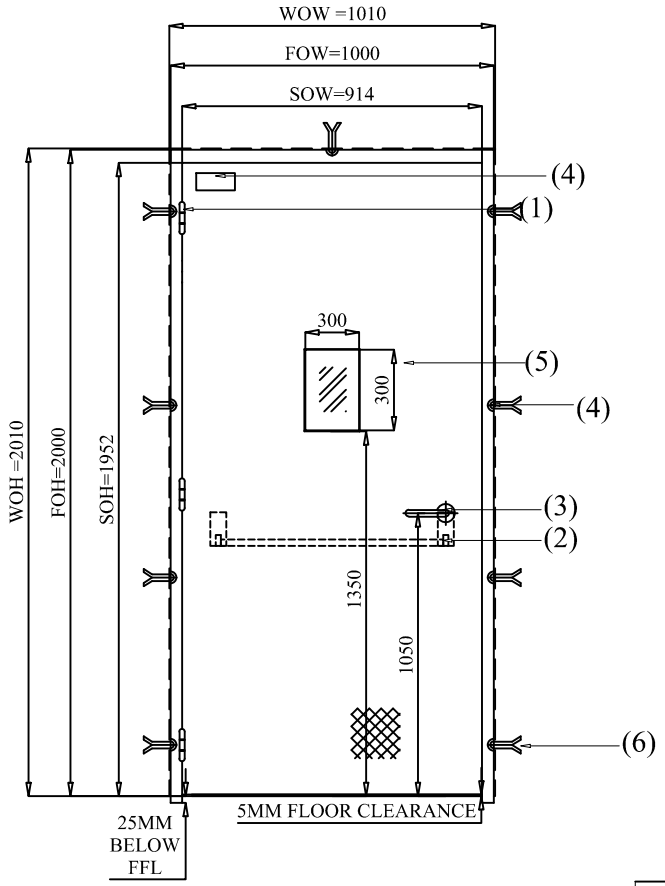


NOTES:–
ALL DIMENSIONS ARE IN MM.

NOTES:–
ALL DIMENSIONS ARE IN MM.

A. ABBREVIATION
Wall Opening Width : WOW
Wall Opening Height : WOH
Frame Opening Height : FOH
Frame Opening Width : FOW
Shutter Opening Height : SOH
Shutter Opening Width : SOW

Door Opening Style - (D)
Left Hand Outside Opening

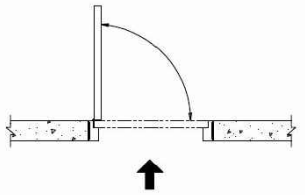

MATERIAL OF CONSTRUCTION

FRAME : G.I. 1.20mm Sheet
SHUTTER : G.I. 0.80mm Sheet
THICKNESS : 40MM
FRAME PROFILE : 100 x 57Mm (Single Ribet)

INFILL MATERIAL : MINERAL WOOL
DENSITY 48kg/cm3

PAINT: AS PER AS APPROVED RAL SHADE POWDER COATED (DFT 80 Microns min)

SCHEDULE OF HARDWARE

1) S.S. Ball Bearing Hinges - 3 NOS (GEZE Make) .
2) Panic Bar for Single Leaf door YALE MAKE - 1 NO
3) External Trim Bar (Panic latch) YALE MAKE -1 Nos
4) Heavy Duty Door Closer GEZE MAKE -1 Nos
5) Vision Panel with Non Fire Rated Glass of Size: 300 x 300MM Clear Glass (6MM) float glass.
6) Anchor Fastener - 8 x 80MM.

PLEASE NOTE : Wall Openings to be maintained at site

SR. NO	WALL OPENING WIDTH	WALL OPENING HEIGHT	QTY	RAL
01	1000	2000	03	9002

TOLERANCE - ±02mm

REV NO	DATE	DRAWN	REMARK
R01	08.01.2020	P.A	DOOR FRAME CHANGE & OPENING STYLE ADD

This drawing & design is the property of NIHVA TECHNOLOGIES. Not to be sold or copied to any other concern.

TITLE: SINGLE LEAF STEEL DOOR

	NAME	SIGN	DATE
DRAWN	P.A		08.01.2020
CHECK	G.J		08.01.2020
APPRD.			

NIHVA TECHNOLOGIES PVT. LTD.
NIHVA TECHNOLOGIES PVT. LTD. PUNE
Tel : 020 66304033
Email:- info@nihva.com
Website:- www.nihva.com

CLIENT - SYNERGY
PROJECT - EMBASSY
SITE LOCATION - CHAKAN, PUNE.
If any queries contact : design@nihva.com
DWG. NO. : NIHVA/19-20/0187/R01 REV- R01
ALL DIMENSION ARE IN mm
SCALE: NTS WT: SHEET: 01 OF 01