

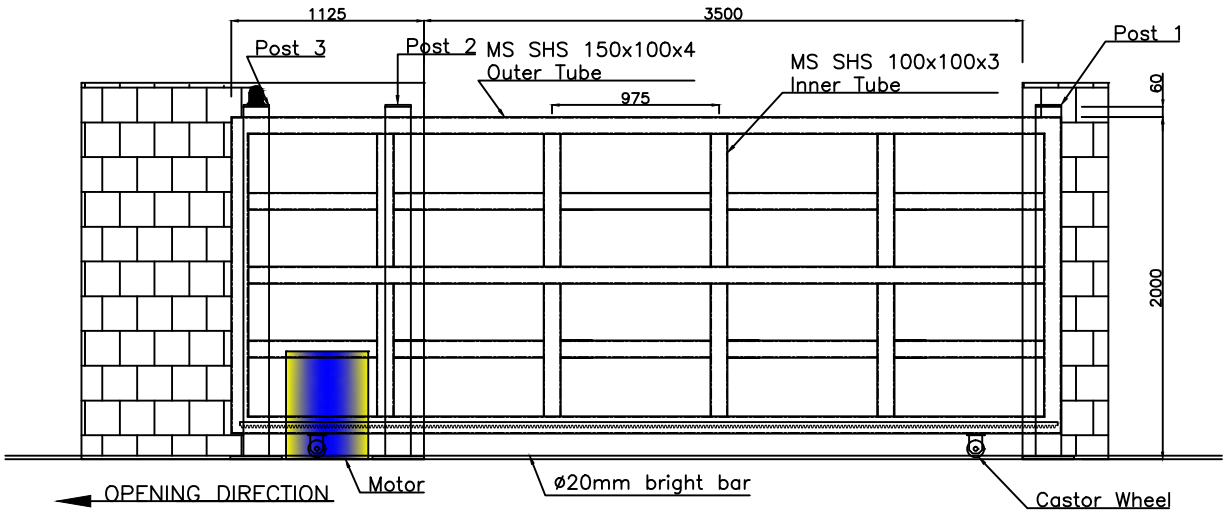



ELEVATION VIEW

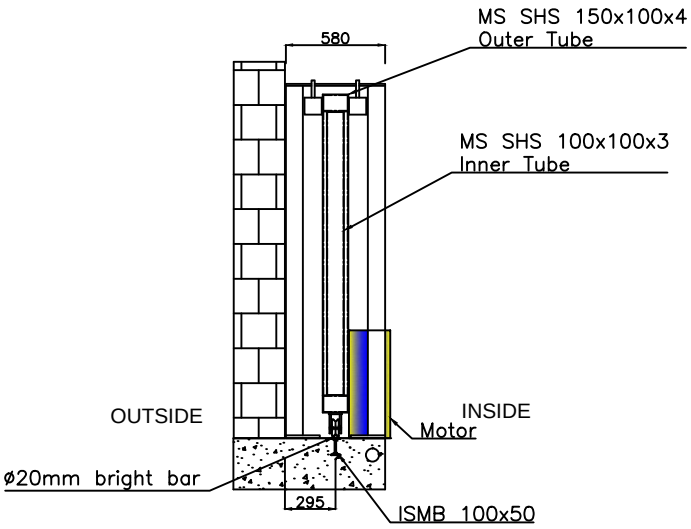


SIDE VIEW

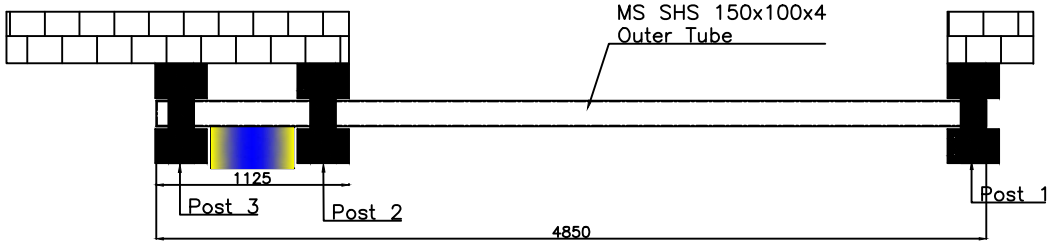


PLAN

## Technical Specs of Motorized Sliding Gate


1. Opening length - 3500mm
2. Gate Height - 2000mm
3. Parking length required - 4850mm
4. Outer tube size - MS SHS 150x100x4mm
5. Inner tube size - MS SHS 100x100x3mm
6. Bottom Rail - Bright bar Ø20mm
7. Post size - MS SHS 150x100x4mm
8. Total leaf weight ≈ kg
9. Safety feature - Photocell and flashing light
10. Operation - Push button from side

Note-


1. All dimension are in mm.
2. All civil work is under client scope.
3. 3" PVC pipe in the foundation to be provided by client.
4. Power supply single phase 230v, 50hz.
5. Cable for power supply 2.5 sqmm 3 core
6. Cable for photocell - 1.5 sqmm 4 core

This drawing & design is the property of NIHVA TECHNOLOGIES. Not to be sold or copied to any other concern.

| TITLE | | | | |
|---|---|---|---|---|
| SLIDING GATE | | | | NIHVA TECHNOLOGIES PVT. LTD. PUNE<br>Tel : 020 66304033<br>Email:- info@nihva.com<br>Website:- www.nihva.com |
| | NAME | SIGN | DATE | |
| DRAWN | G.P. | | 10.08.21 | CLIENT -HAIMAVATHY PROPERTIES PVT. LTD. |
| CHECK | A.K. | | 10.08.21 | LOCATION - MUMBAI |
| APPRD. | V.T. | | 10.08.21 | PRODUCT - SLIDING GATE 3500 X 2000 |
| If any queries contact : design@nihva.com | | | | NIHVA\20-21\0191 / REV- 0 |
| ALL DIMENSION ARE IN mm | | | | SCALE: NTS / SHEET: 01 OF 02 |

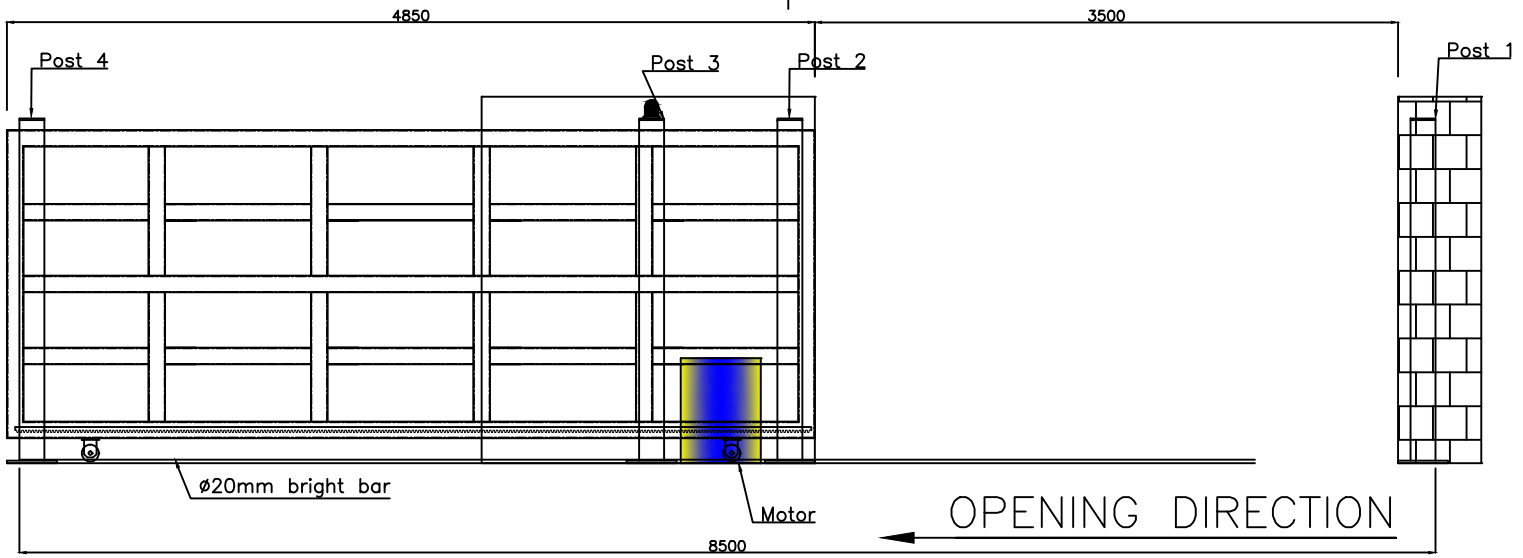


# STACKED GATE ELEVATION

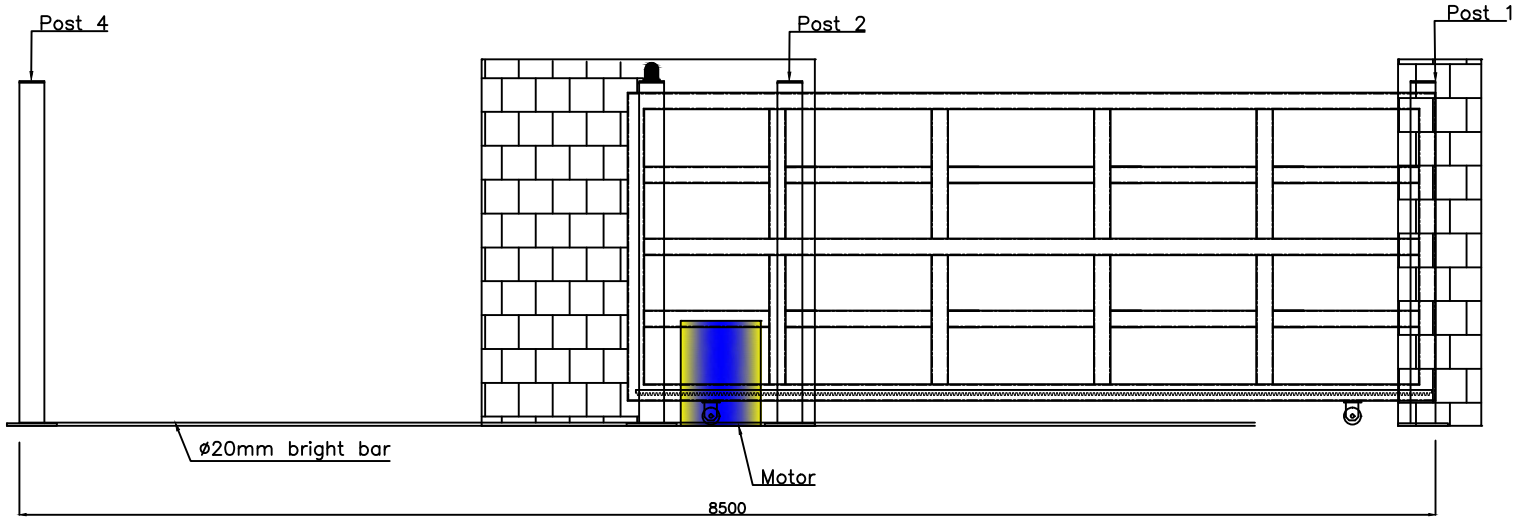


# CLOSED GATE ELEVATION

This drawing & design is the property of NIHVA TECHNOLOGIES. Not to be sold or copied to any other concern.

| TITLE | | | | |
|---|---|---|---|---|
| SLIDING GATE | | | | NIHVA TECHNOLOGIES PVT. LTD. PUNE<br>Tel : 020 66304033<br>Email:- info@nihva.com<br>Website:- www.nihva.com |
| | NAME | SIGN | DATE | |
| DRAWN | G.P. | | 10.08.21 | CLIENT -HAIMAVATHY PROPERTIES PVT. LTD. |
| CHECK | A.K. | | 10.08.21 | LOCATION - MUMBAI |
| APPRD. | V.T. | | 10.08.21 | PRODUCT - SLIDING GATE 3500 X 2000 |
| If any queries contact : design@nihva.com | | | | NIHVA\20-21\0191 REV- 0 |
| ALL DIMENSION ARE IN mm | | | | SCALE: NTS SHEET: 02 OF 02 |