

PROPOSED PLAN LAYOUT

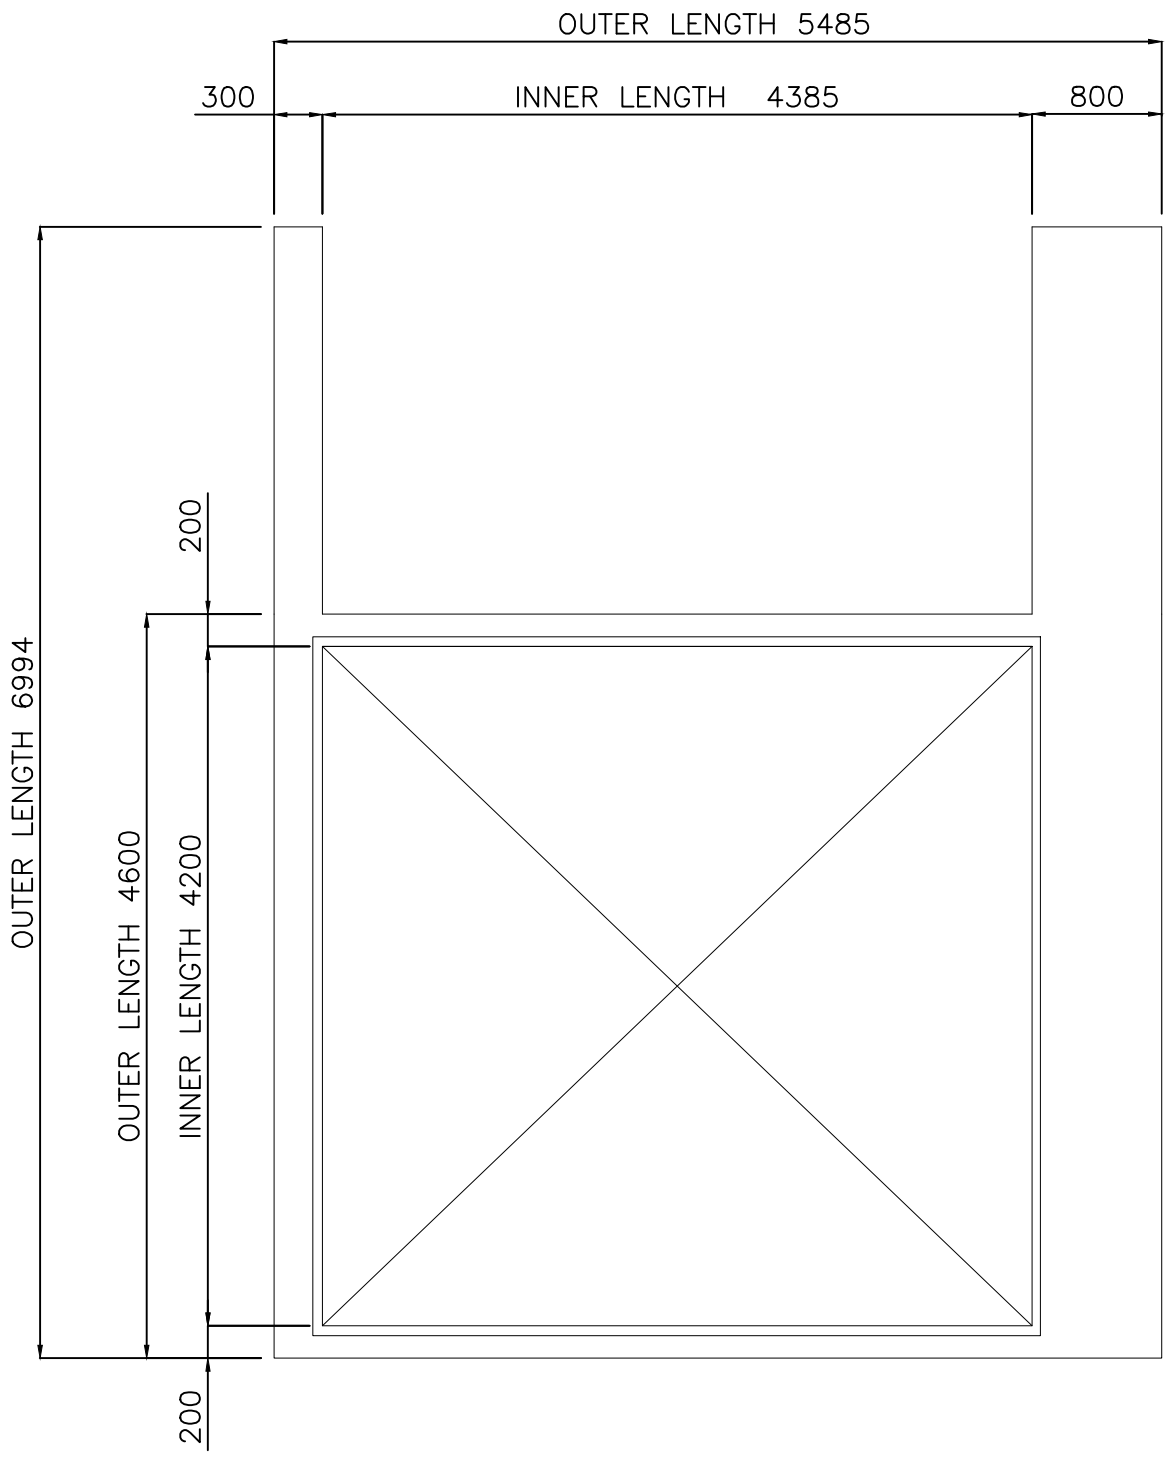

PROPOSED PLAN

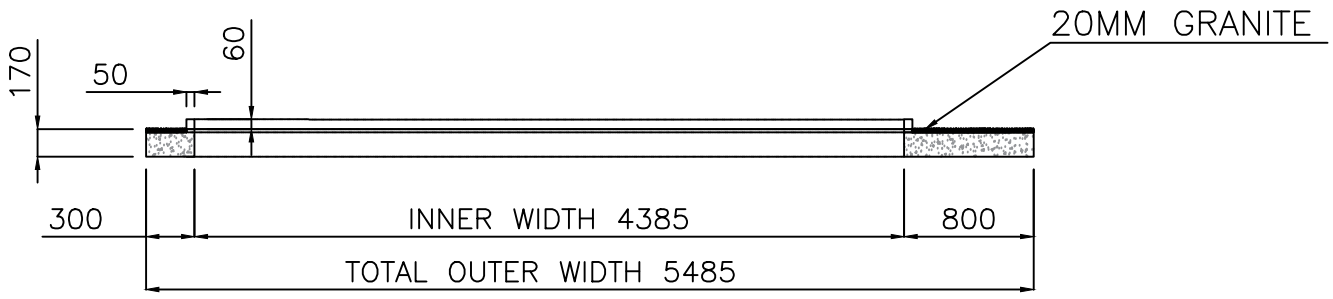

SECTION VIEW

1. THE STRUCTURE AROUND THE CUT OUT SHOULD BE OF CONCRETE FOR PROPER FASTENING OF ROOF.
2. TOP SURFACE SHOULD BE OF GRANITE 20MM FOR SMOOTH FUNCTIONING OF ROOF.
3. ROOF EXTENSION IS SHOWN FOR ONLY REFERENCE. IT CAN BE MODIFIED AS PER THE WORK UNDERTAKEN.
4. GRADIENT OF 80MM NEED TO BE PROVIDED ALONG THE OUTER LENGTH TO AVOID WATER STAGNANCY IN GUIDE RAIL.
5. AL PROFILE - POWDER COATED
6. GASKET - EPDM
7. MOTOR - ITALIAN/GERMAN MAKE
8. ELECTRICAL REQUIREMENT - .
9. ALL DIMENSION IN MM.
10. ALL CIVIL WORK IS IN CLIENT SCOPE

This drawing & design is the property of NIHVA TECHNOLOGIES. Not to be sold or copied to any other concern.

TITLE: PROPOSED PLAN LAYOUT (IN CLIENT SCOPE)	NAME	SIGN	DATE	NIHVA TECHNOLOGIES PVT. LTD.	
DRAWN	D.V.		01.03.23	CLIENT - MAXIMA	
CHECK	P.M.		01.03.23	LOCATION - MUMBAI_IN	
APPRD.	V.T.		01.03.23	PRODUCT - RETRACTABLE ROOF	
If any queries contact : supportautomation@nihva.com				NIHVA\22-23\02XX	REV- 3
ALL DIMENSION ARE IN mm				SCALE: NTS	SHEET: 01 OF 01