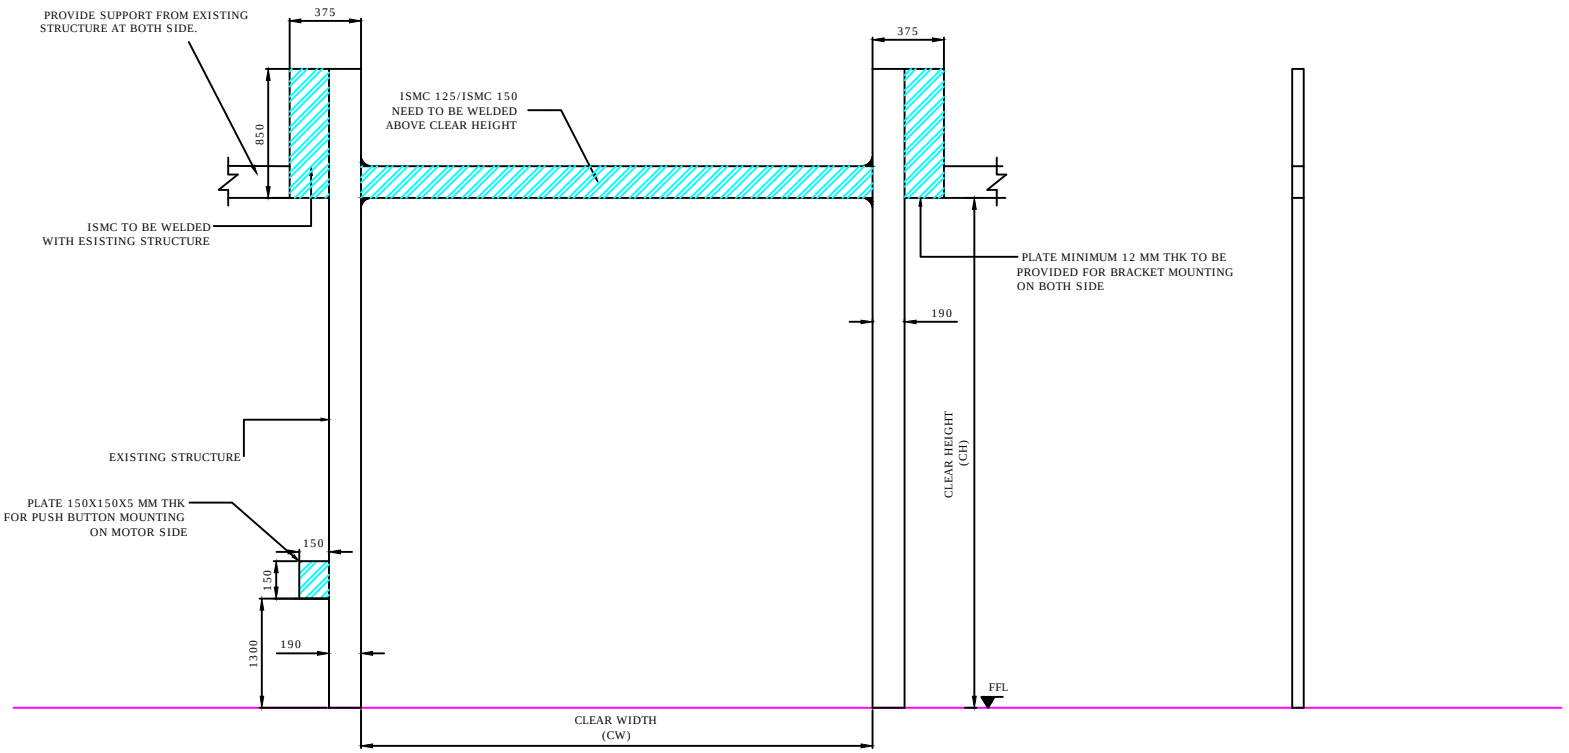

STRUCTURE

SR NO	CLEAR WIDTH (CW)	CLEAR HEIGHT (CH)	QTY	LOCATION
4	6070	7700	1	F-19
3	6070	7700	1	B-19
2	6070	7700	1	F-1
1	6070	7700	1	B-1

NOTES-
(1) MS STRUCTURE , FITTING & ALL CIVIL WORK IS IN CLIENT SCOPE.
(2) SHUTTER WILL BE ONLY INSTALLED AFTER READINESS OF STRUCTURE AS PER DRAWING PROVIDED.

This drawing & design is the property of NIHVA TECHNOLOGIES. Not to be sold or copied to any other concern.

TITLE- MS STRUCTURE FOR 6000 X 8000

	NAME	SIGN	DATE
DRAWN	SIDDHESHWAR		8.12.2020
CHECK			
APPRD.			

If any queries contact : projectsupport@nihva.com

ALL DIMENSION ARE IN mm

NIHVA TECHNOLOGIES PVT. LTD.
NIHVA TECHNOLOGIES PVT. LTD. PUNE
Tel : 020 66304033
Email:- info@nihva.com
Website:- www.nihva.com

CLIENT - GS PEB & CIVIL WORKS PVT LTD
PROJECT - SANY HEAVY INDUSTRY INDIA PVT LTD
SITE LOCATION - PUNE
DWG. NO. : NIHVA/20-21/0102 REV- R00
SCALE: NTS WT: SHEET: