



HINGE SUPPORT PLATE

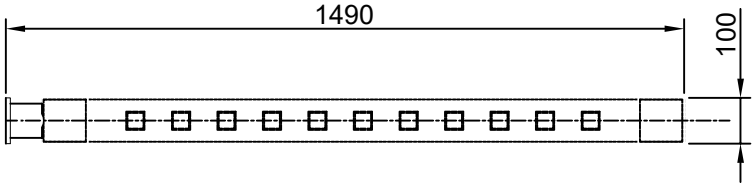

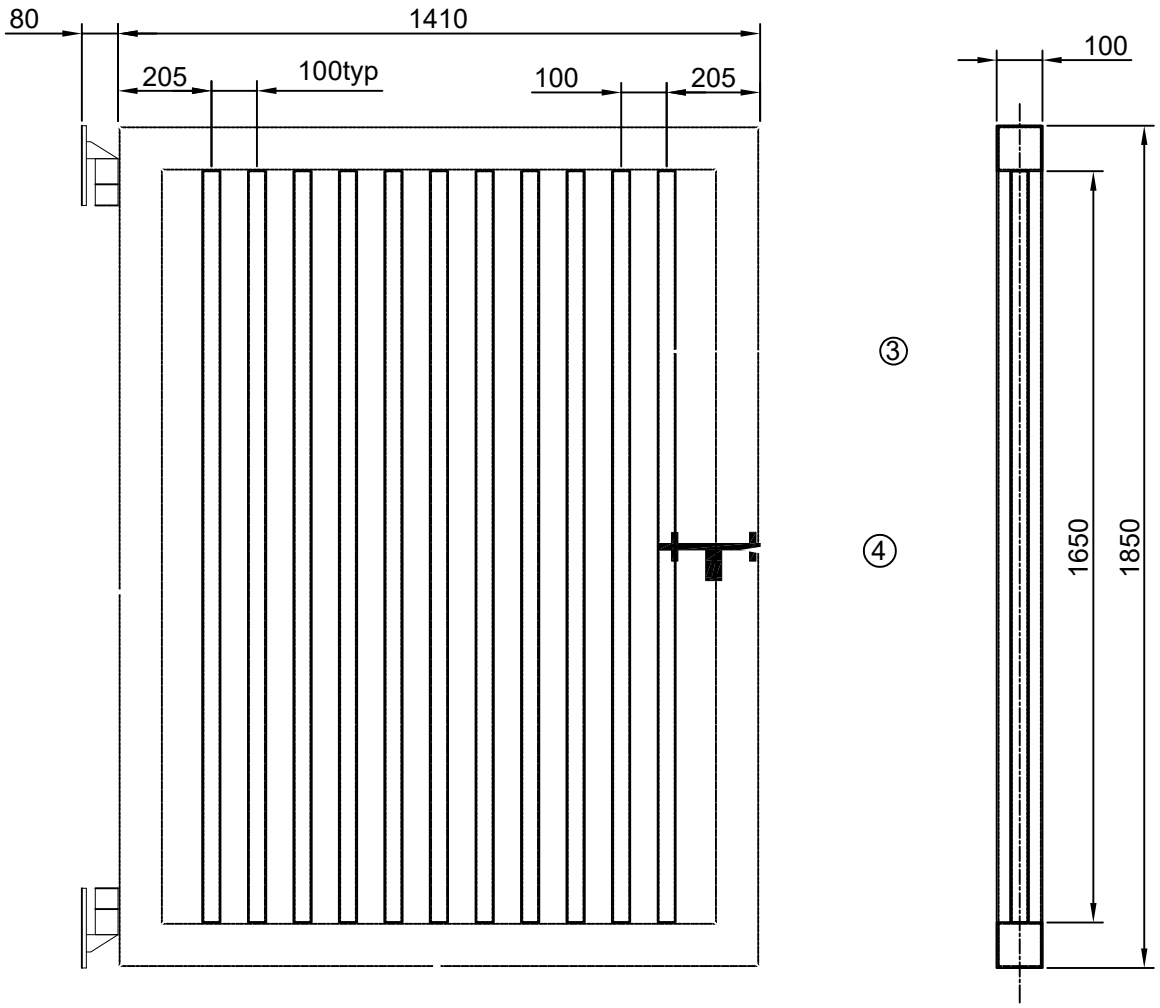

BOM FOR SINGLE POST			
SL NO.	DESCRIPTION	SPECIFICATION	QTY
1	MS SQ. TUBE	100X100X3.6X1850L	2NOS
2	MS SQ. TUBE	100X100X3.6X1410L	2NOS
3	MS SQ. TUBE	40X40X3.6X1650L	11NOS
4	LOCK	ALDROP	1NO
5	SUPPORT CHANNEL	ISMC 75 X 40, 70L	2NOS
6	HINGE	2" MANUAL HINGE	2NOS
7	HINGE SUPPORT PLATE	175X175X10THK	2NOS

This drawing & design is the property of NIHVA TECHNOLOGIES. Not to be sold or copied to any other concern.

TITLE:- WICKET GATE

NIHVA TECHNOLOGIES PVT. LTD. PUNE
Tel : 020 66304033
Email:- info@nihva.com
Website:- www.nihva.com

	NAME	DATE	SIGN
DRAWN	SUJATA.B	16/10/2021	
CHECK	G.PATIL	16/10/2021	
APPRD.	A.KURHADE	16/10/2021	

If any queries contact : design@nihva.com

ALL DIMENSION ARE IN mm

CLIENT -SCON PROJECTS

LOCATION -

PRODUCT - | QTY:-01NO

DWG NO:-NIHVA\21-22\VDR\0253 | REV- 0

SCALE: NTS | SCALE:-- 1:1 | SHEET: 01 OF 01

Rev No.	Revision	Date	Revised By