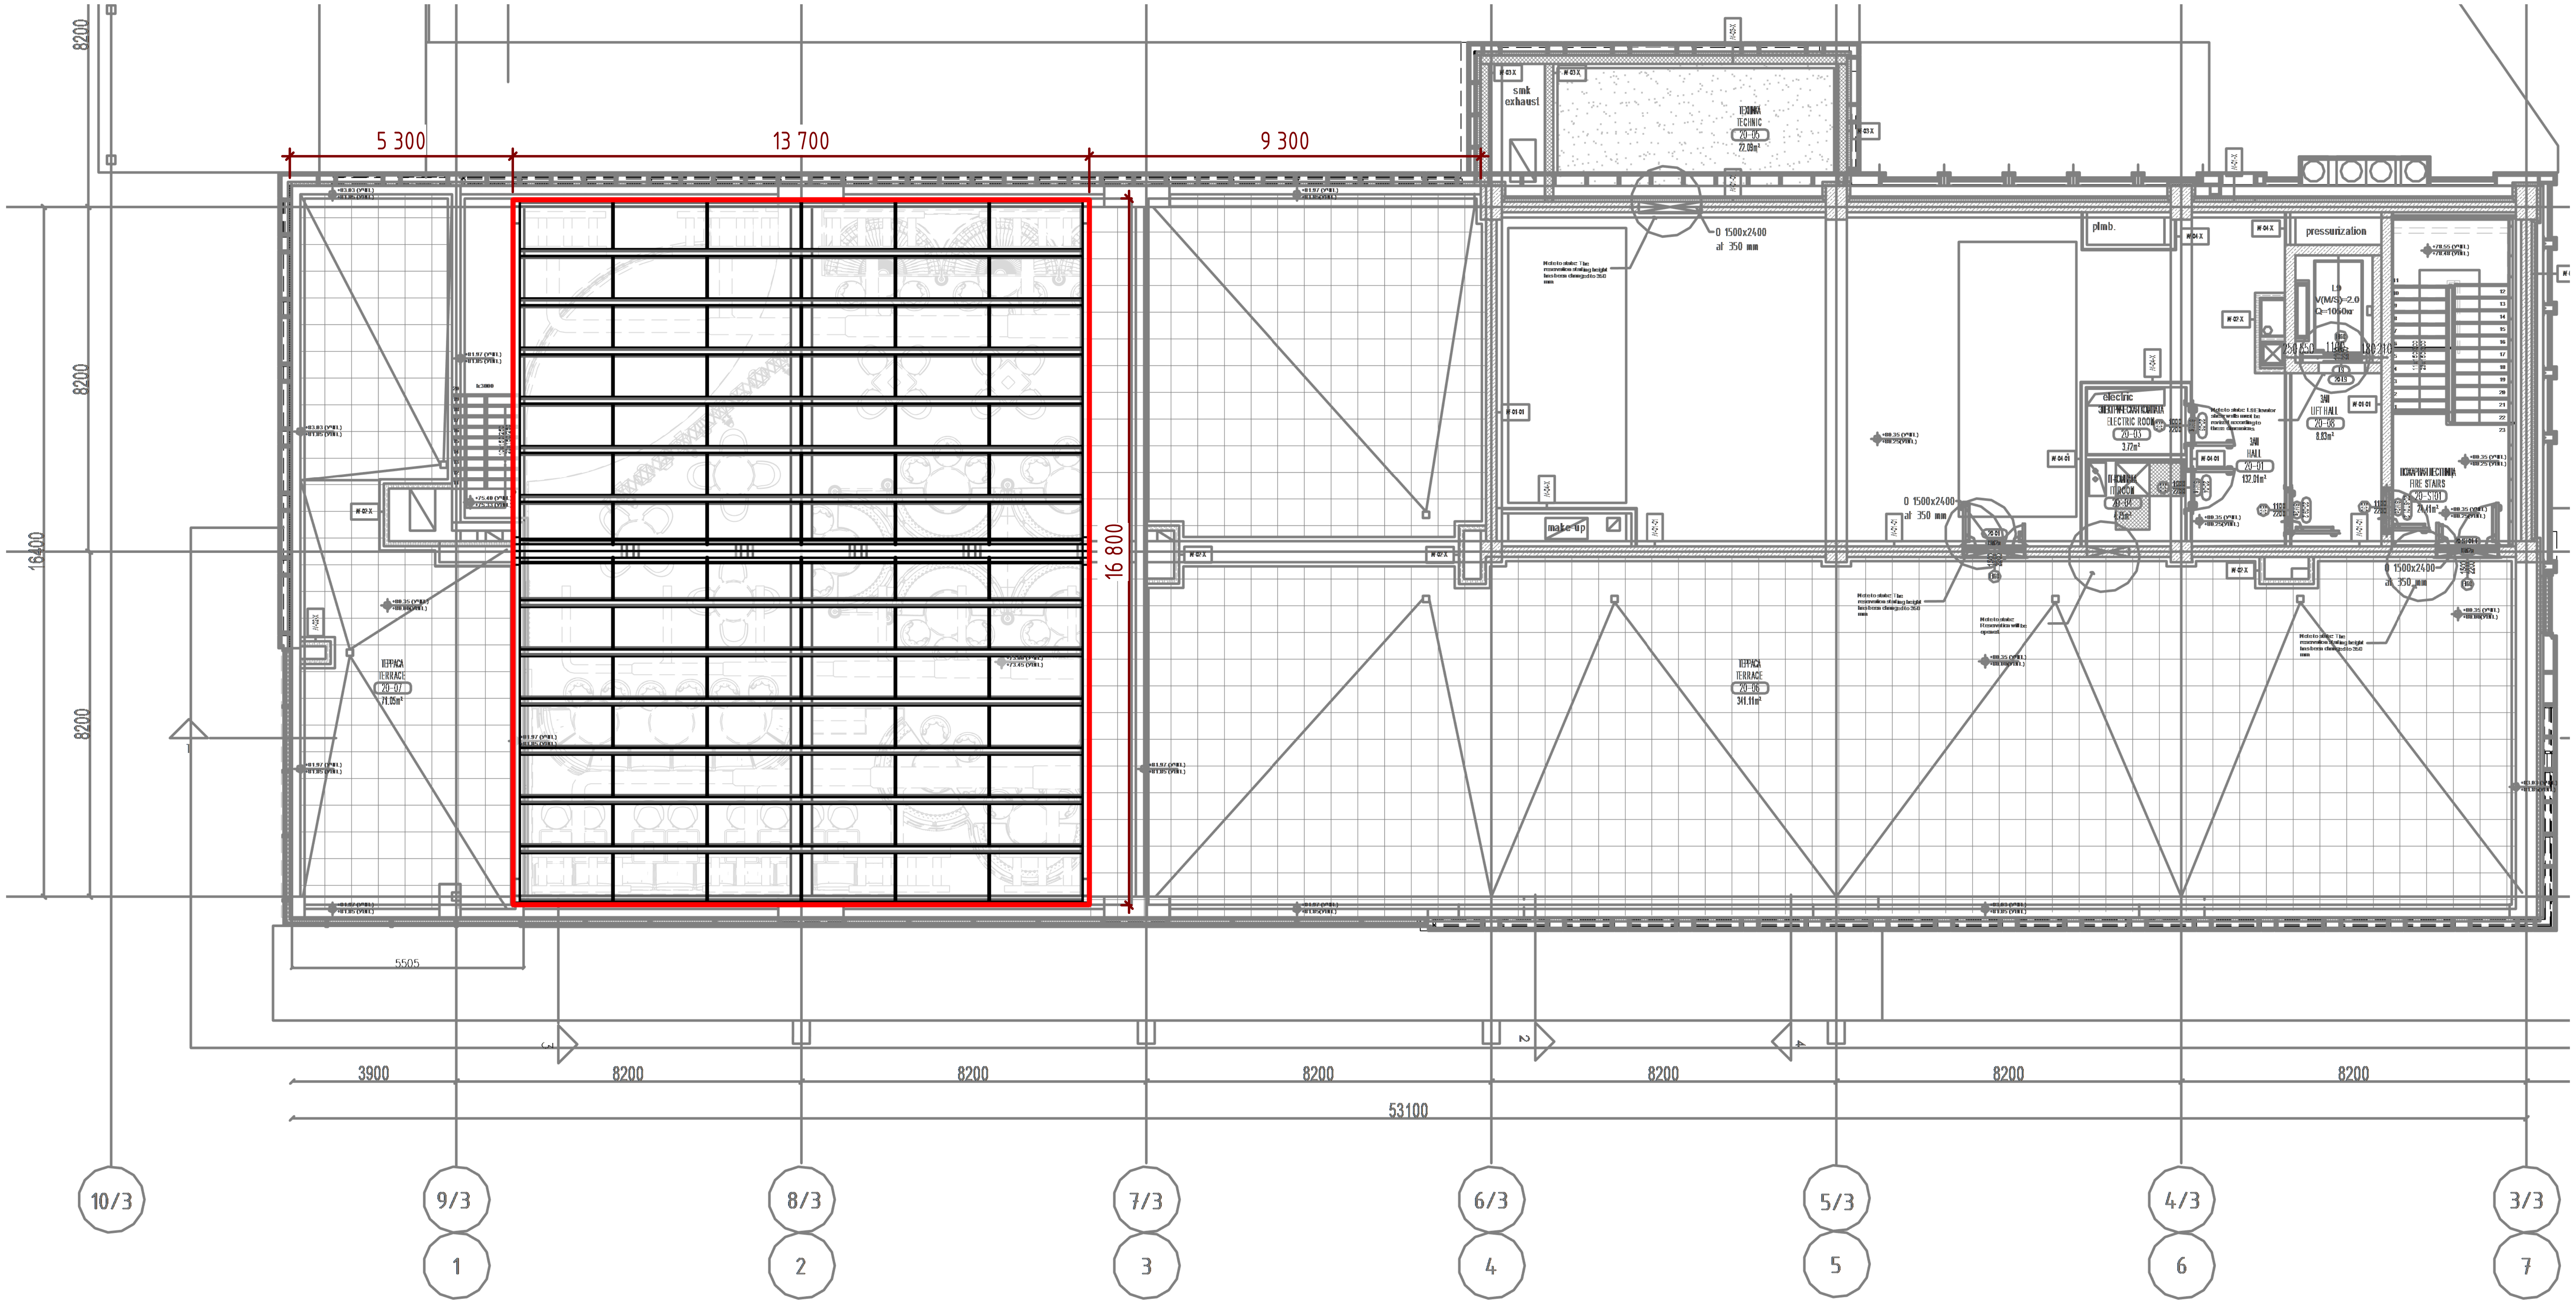
5 300
13 700
9 300
16 800
8200
8200
8200
16400
smk exhaust
ТЕХНИКА
TECHNIC
20-05
22.09m²
0 1500x2400 at 350 mm
plmb.
pressurization
make-up
electric
ELECTRIC ROOM
20-03
3.72m²
IT ROOM
20-04
L9
V(M/S)=2.0
Q=1050кг
ЗАЛ
LIFT HALL
20-08
8.63m²
ЗАЛ
HALL
20-01
132.01m²
FIRE STAIRS
20-ST01
24.41m²
ТЕРРАСА
TERRACE
20-06
341.11m²
ТЕРРАСА
TERRACE
20-07
71.05m²
5505
3900
8200
8200
8200
8200
8200
8200
53100
10/3
9/3
8/3
7/3
6/3
5/3
4/3
3/3
1
2
3
4
5
6
7

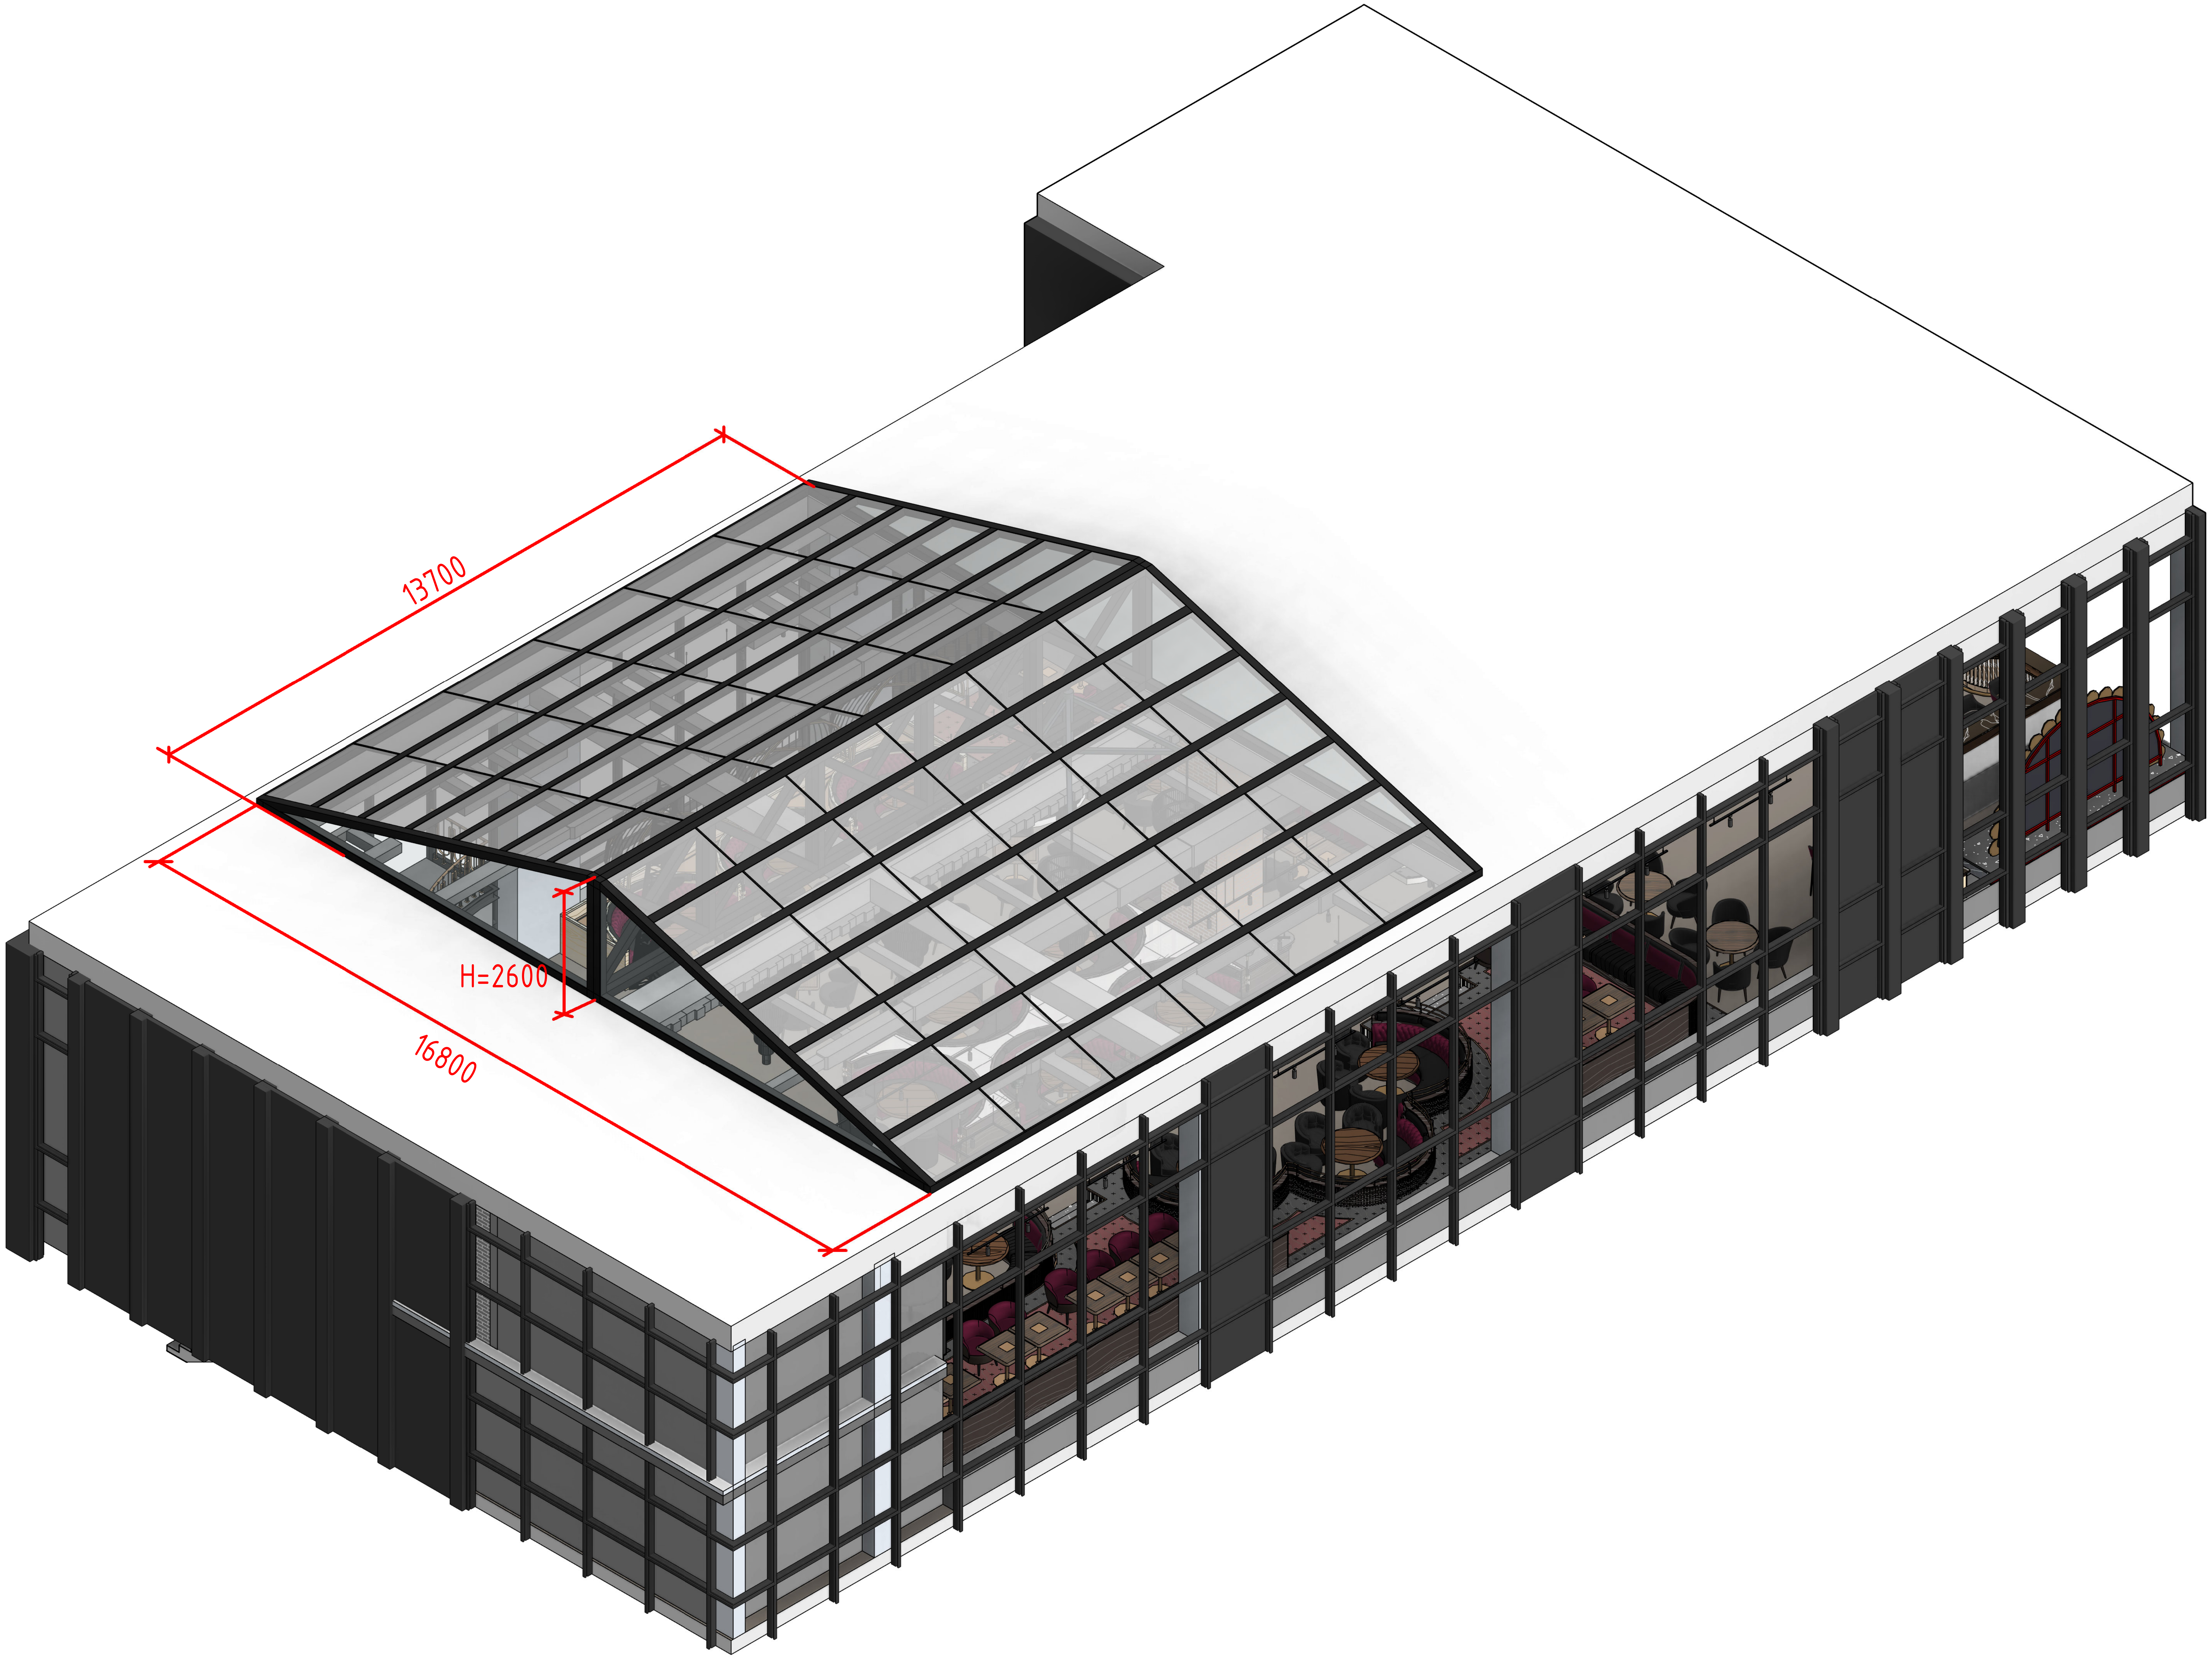
13700
H=2600
16800