

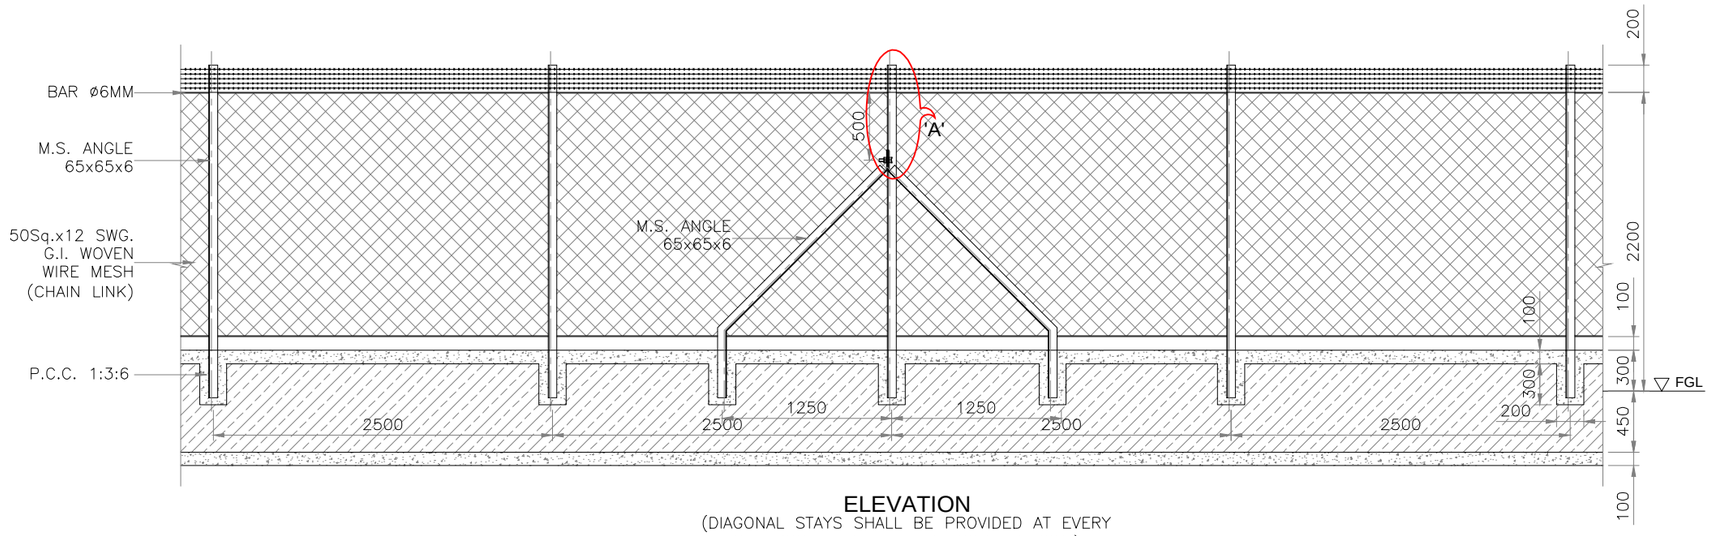


ELEVATION


(DIAGONAL STAYS SHALL BE PROVIDED AT EVERY 8TH POST AND AT EVERY CORNER POST)

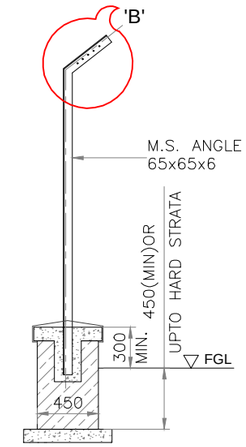


TYPICAL C/S

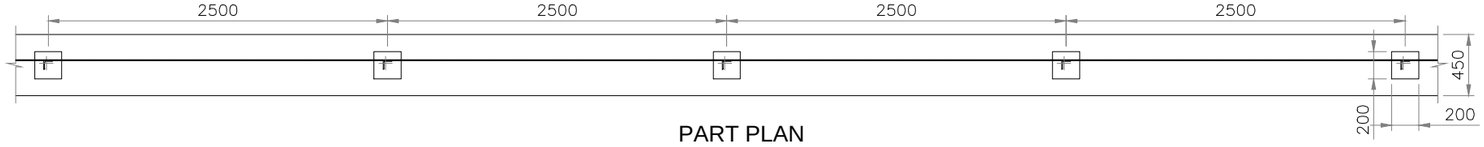


PART PLAN

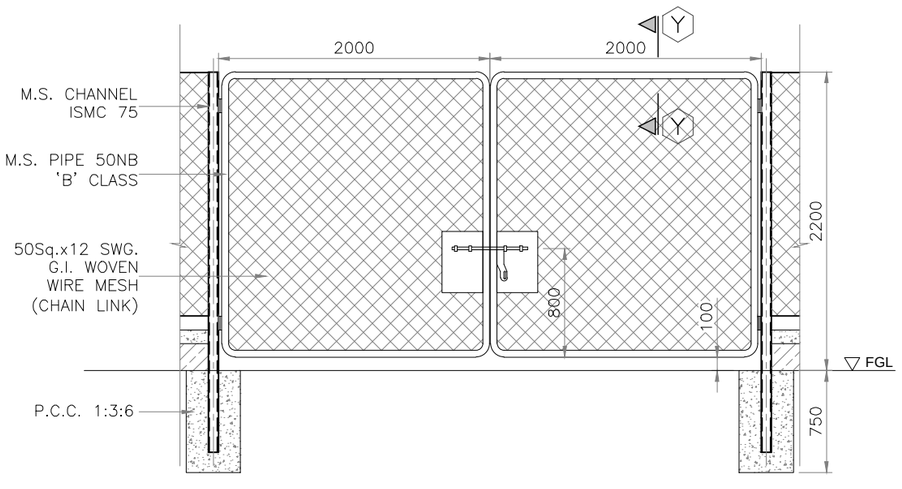


GATE ELEVATION

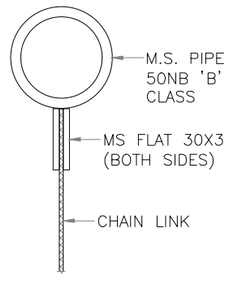

SECTION Y-Y

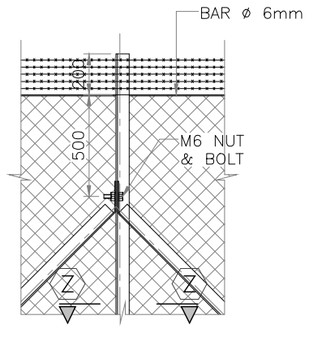

DETAILS AT 'A'

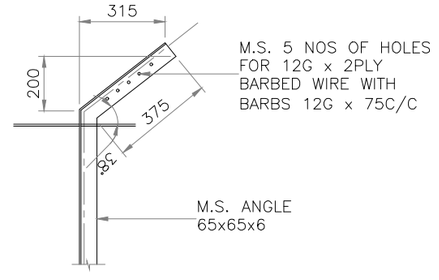

DETAILS AT 'B'



SECTION Z-Z

FOR TENDER

DATE : 07.06.2021

NOTES :

1) ALL DIMENSIONS ARE IN mm. AND LEVELS ARE IN METRES.
2) DO NOT SCALE THE DRAWING. IN CASE OF DOUBT, PLEASE ASK.

TITLE : TRANSFORMER YARD FENCING & GATE

-

DRN BY	NND	15.10.2007	REV
CHKD BY			R0
APRD BY			

Associated Engineering Consultants.
313,Siddharth Towers, 12/3B, Kothrud, Pune 411 029, Tel:2545 3863/64

DRG NO. AEC-0013

SHEET 1/1

DO NOT SCALE THE DRAWING.

IN CASE OF DOUBT, PLEASE ASK US.

CAD FILE NAME: