

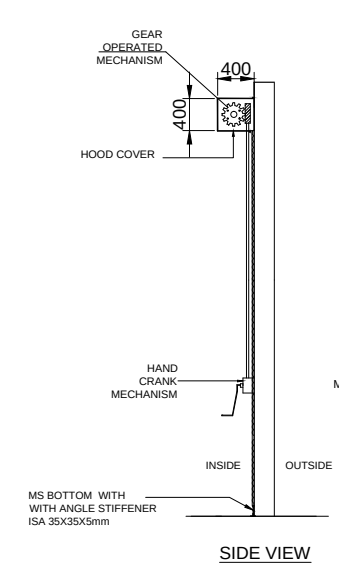



SIDE VIEW

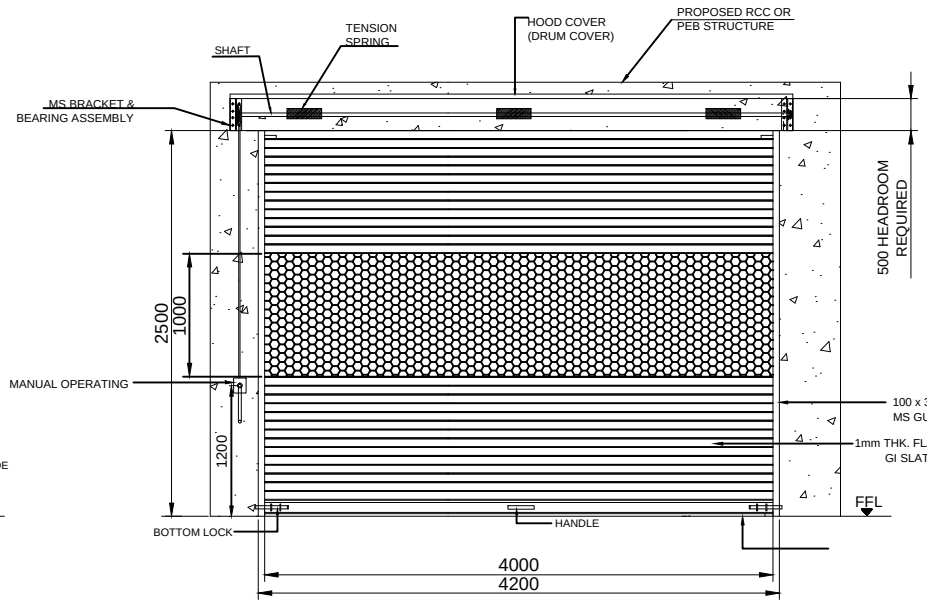


INSIDE ELEVATION

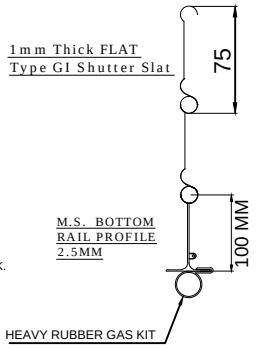


M.S. BOTTOM RAIL PROFILE 2.5MM

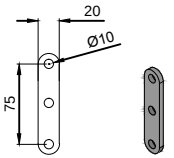


MS BOTTOM WITH ANGLE STIFFNER WITH RUBBER SAFTEY EDGE

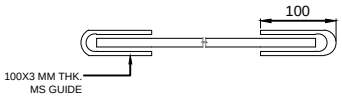

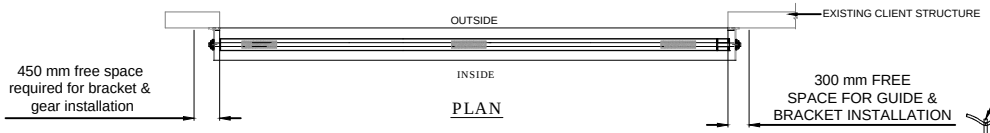

PLAN

5mm THK. LINK

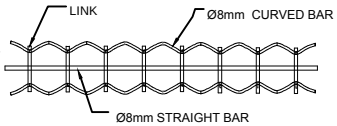

S.NO	FEATURE	EQUIPMENT DETAILS
01	SLATS MODEL	GALVANISE STEEL(GI) SLATS 1mm THK.
02	GUIDE RAIL	100 X 3mm THK MILD STEEL(MS).
03	BOTTOM RAIL	2.5mm THK MILD STEEL (M.S.).
04	HOOD COVER	0.9mm THK GALVANISE STEEL (GI).
05	RAL COLOR	RAL 9002

SR.NO.	SIZE	QUANTITY
01	4000(W)X2500(H)	03 NOS

RAL COLOR
RAL 9002 (WHITE GREY)

SHUTTER LOCATION :- R.M.U

SURAJ		R01	27/07/2018.	1.SHUTTER QTY. CHANGED 2.SHUTTER SIZE CHANGED 3.GRILL ADDED IN SHUTTER & DETAILS
DRAWN NAME	SIGN	REVISION	DATE	REVISION DETAILS

TOLERANCE - ±10mm

NOTE-
1. ALL CIVIL WORK WILL BE CLIENT'S SCOPE.

This drawing & design is the property of NIHVA TECHNOLOGIES. Not to be sold or copied to any other concern.

TITLE: GEAR OPERATED ROLLING SHUTTER

	NAME	SIGN	DATE
DRAWN	PRADEEP		26.07.2018
CHECK	SURAJ		26.07.2018
APPRD.	DANGE		26.07.2018

If any queries contact : design@nihva.com

ALL DIMENSION ARE IN mm

NIHVA TECHNOLOGIES PVT. LTD.
NIHVA TECHNOLOGIES PVT. LTD. PUNE
Tel : 020 66304033
Website:- www.nihva.com
Email:- info@nihva.com

CLIENT - SYNERGY

PROJECT-EMBASSY INDUSTRIAL PARKS PVT. LTD.

SITE LOCATION - CHAKAN

DWG. NO. : NIHVA/18-19/0088/R01 | REV- 01

SCALE: NTS | WT: | SHEET: 01 OF 01