

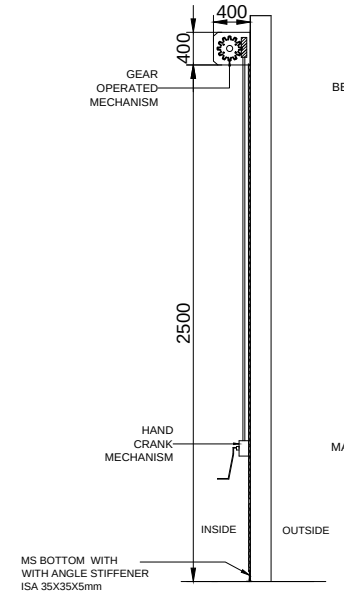



SIDE VIEW

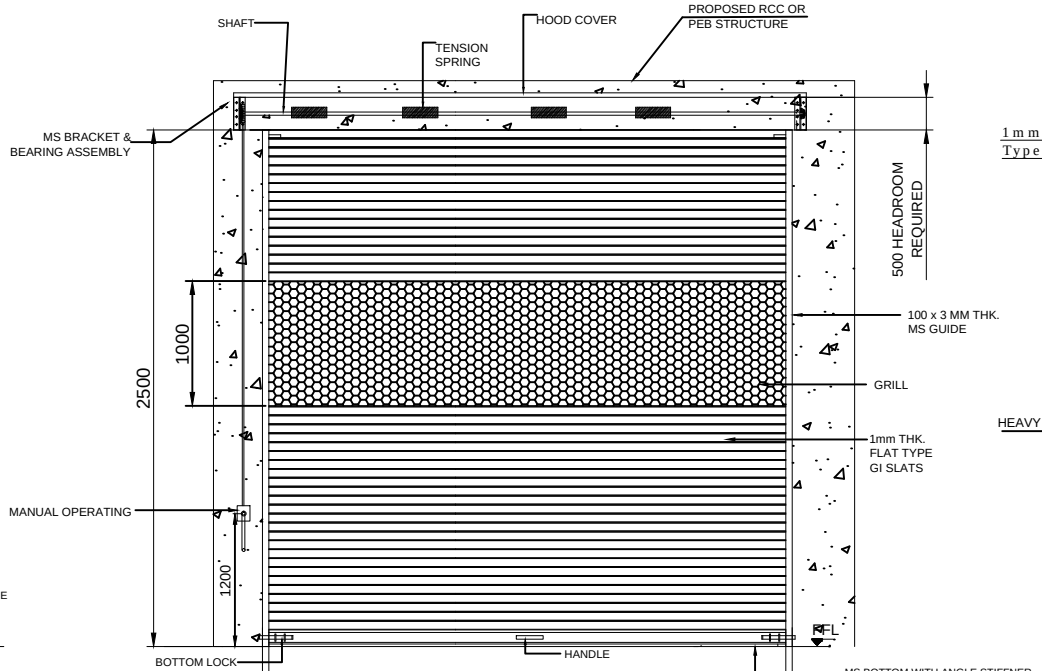


INSIDE ELEVATION

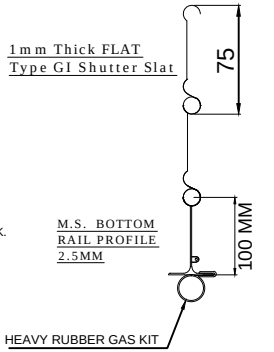


M.S. BOTTOM RAIL PROFILE 2.5MM

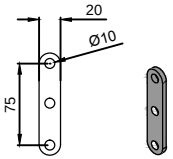


5mm THK. LINK

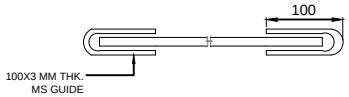

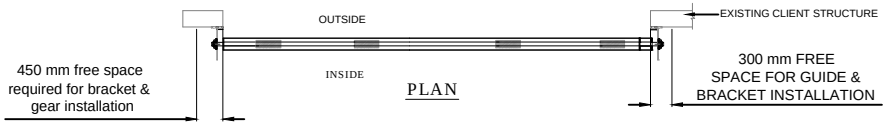

PLAN

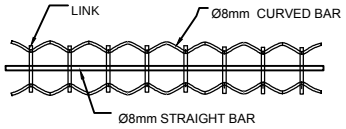

S.NO	FEATURE	EQUIPMENT DETAILS
01	SLATS MODEL	GALVANISE STEEL(GI) SLATS 1mm THK.
02	GUIDE RAIL	100 X 3mm THK MILD STEEL(MS).
03	BOTTOM RAIL	2.5mm THK MILD STEEL (M.S.).
04	HOOD COVER	0.9mm THK GALVANISE STEEL (GI).
05	RAL COLOR	RAL 9002 (OUTSIDE OF SHUTTER) RAL 7040 (INSIDE OF SHUTTER)
06	GRILL	MS GRILL

SR.NO.	RAL COLOR	
01	RAL 9002 (WHITE GREY)	OUTSIDE
02	RAL 7040 (WINDOW GREY)	INSIDE

SR.NO.	SIZE	QUANTITY
01	4000(W)X2500(H)	10

TOLERANCE - ±10mm

NOTE-
1. ALL CIVIL WORK WILL BE CLIENT'S SCOPE.

This drawing & design is the property of NIHVA TECHNOLOGIES. Not to be sold or copied to any other concern.

TITLE				
GEAR OPERATED ROLLING SHUTTER				NIHVA TECHNOLOGIES PVT. LTD. PUNE Tel : 020 66304033 Email:- info@nihva.com Website:- www.nihva.com
	NAME	SIGN	DATE	
DRAWN	PRADEEP		12-07-2018	CLIENT - SYNERGY
CHECK	R.D		12-07-2018	PROJECT-EMBASSY INDUSTRIAL PARKS PVT. LTD.
APPRD.	V.T		12-07-2018	SITE LOCATION - CHAKAN
If any queries contact : design@nihva.com				DWG. NO. : NIHVA/18-19/0084 / REV- 00
ALL DIMENSION ARE IN mm				SCALE: NTS / WT: / SHEET: 01 OF 01