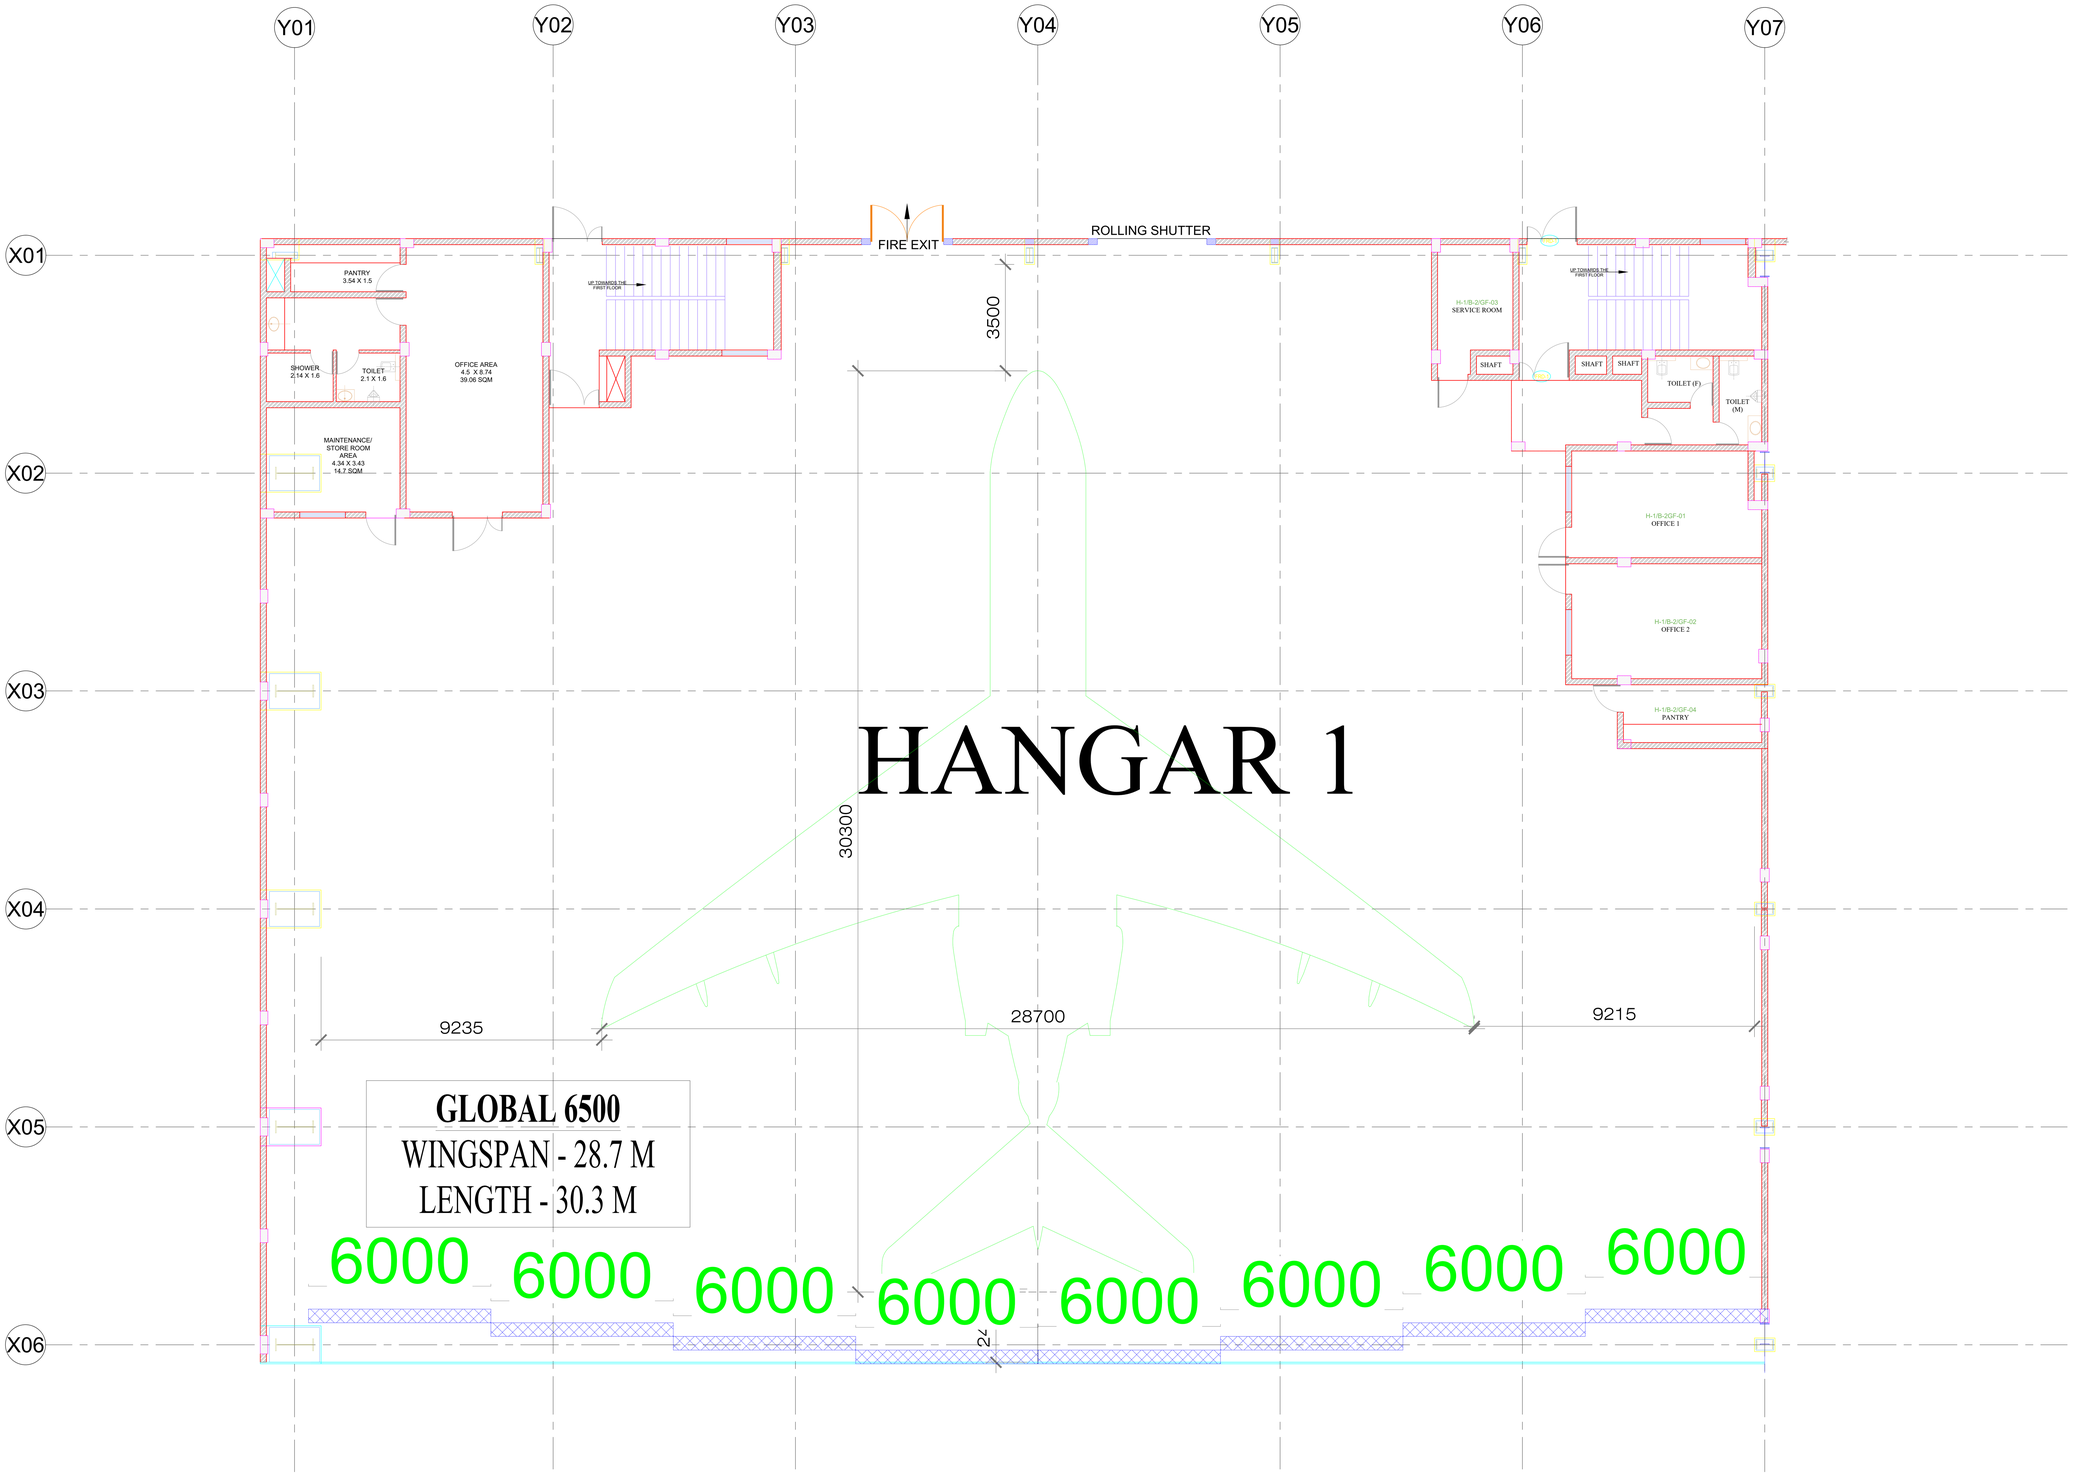


GROUND FLOOR

GENERAL NOTES

1. Do not scale the drawing.
2. All Structural Drawings should be read in conjunction with relevant Architectural Drawings.
3. Any Discrepancy or Ambiguity in drawings should be brought to the Architect's notice immediately prior to Construction at Site.
4. All Dimensions and levels are in mm unless noted otherwise.
5. All Dimensions are from unfinished to unfinished levels unless otherwise specified.
6. Any irregularities in Construction which occurs as a result of discrepancy between Architecture, Structure, MEP, other drawings, which have not been brought to the Architects notice prior to execution shall become the responsibility of the Contractor.
7. Supervision if specifically asked would be provided but responsibility regarding correct & sound Construction shall solely rest with Contractor/Builder.
8. All relevant samples to be approved by architect prior to procurement.

PROJECT TITLE

CONSTRUCTION OF GA COVERED PARKING FOR AIRCRAFTS AND ANCILLARY WORKS AT GENERAL AVIATION TERMINAL, NEW DELHI

CLIENT

DELHI INTERNATIONAL AIRPORT LIMITED (GMR)

ARCHITECTS

A.T. TECHNOLEGAL COMBINE PRIVATE LIMITED
BL-63, SECTOR-116, NOIDA (UP)
MOBILE: +91-9999717558, +91-8285110902
E-MAIL: ATTLCPL@GMAIL.COM

DRAWING TITLE

HANGAR -1
GROUND FLOOR PLAN

ATT/2022/DIAL/GACP/REF-21

FOR REFERENCE

REVISION NOTES

NO	DATE	REVISION REMARKS	SIGN

DATE	21-08-2024
SCALE	NTS
DEALT BY	GARIMA
CHECKED BY	TAPAN GOYAL

COPYRIGHT

All designs & drawings are the property of **A.T. Technolegal Combine Private Limted** and cannot be used without their written approval.