

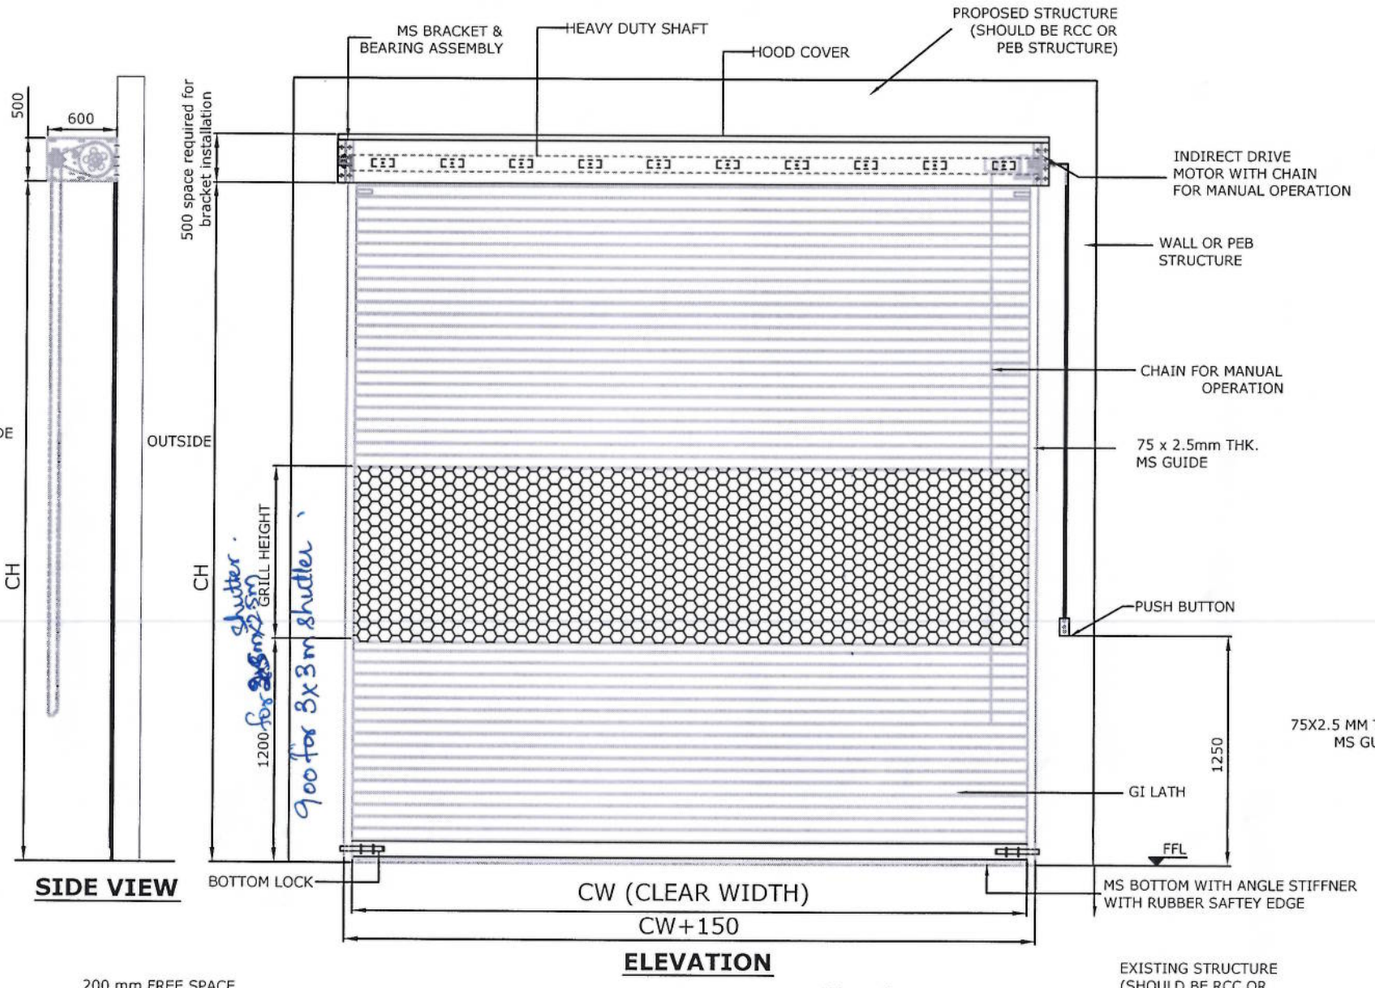


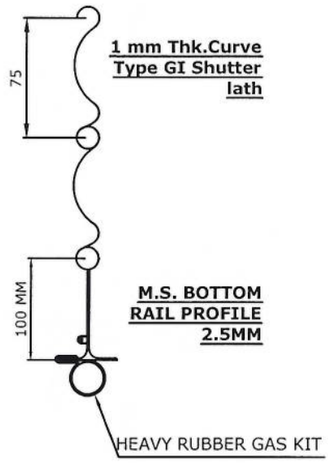

M.S. BOTTOM RAIL PROFILE 2.5MM

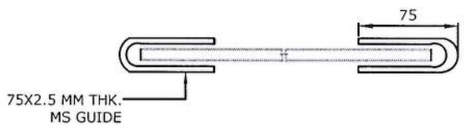

CLEAR WIDTH (CW)	CLEAR HEIGHT (CH)	QUANTITY	GRILL HEIGHT	LOCATION
3000mm	3000mm	01 NOS	750mm	FACILITIES & DTZ CONTROL ROOM
2500mm	2500mm	02 NOS	625mm	TESTING BUILDING 1.COMPRESSOR ROOM 2.WASTER WATER NEUTRALIZATION ROOM

DIMENSION :		
CLEAR WIDTH	CLEAR HEIGHT	QUANTITY
3000	3000	01 NOS
2500	2500	02 NOS

MATERIAL:

THICKNESS :

NOTE:
1. REQUIRED STRUCTURE FOR ROLLING SHUTTER WILL BE CLIENT'S SCOPE.
2. ONE COAT OF RED OXIDE PRIMER WILL BE GIVEN TO THE SHUTTER.
3. SINGLE PHASE. 3 CORE 1.5 SQ. CABLE REQUIRE AT SITE(CLIENT'S SCOPE)
4. FINAL FINISH WILL BE AS SUPPLIED EARLIER.

Colour code :- RAL..

NIHVA
NIHVA TECHNOLOGIES PVT. LTD.
NIHVA TECHNOLOGIES PVT. LTD. PUNE
Email:- info@nihva.com
Website:- www.nihva.com

TITLE:

MOTORIZED ROLLING SHUTTER

CLIENT'S APPROVAL :

CLIENT - TATA PROJECT LTD.

PROJECT -ALSTOM.

SITE LOCATION - HYDERABAD

DWG. NO. : NIHVA/17-18/0207


SCALE: NTS	WT:	SHEET:1 OF 1
DRAWN BY: SURAJ		DATE: 19-09-2017
CHECK BY : SAGAR P.		DATE: 19-09-2017
APPROVED BY :SHEKHAR		DATE: 19-09-2017

If any queries contact : projects@nihva.com


NOTE: ALL DIMENSIONS ARE IN mm

THIS DRAWING & DESIGN IS THE PROPERTY OF NIHVA TECHNOLOGIES. NOT TO BE SOLD OR COPIED TO ANY OTHER CONCERN.

Size checked and OK.
For T.P.L

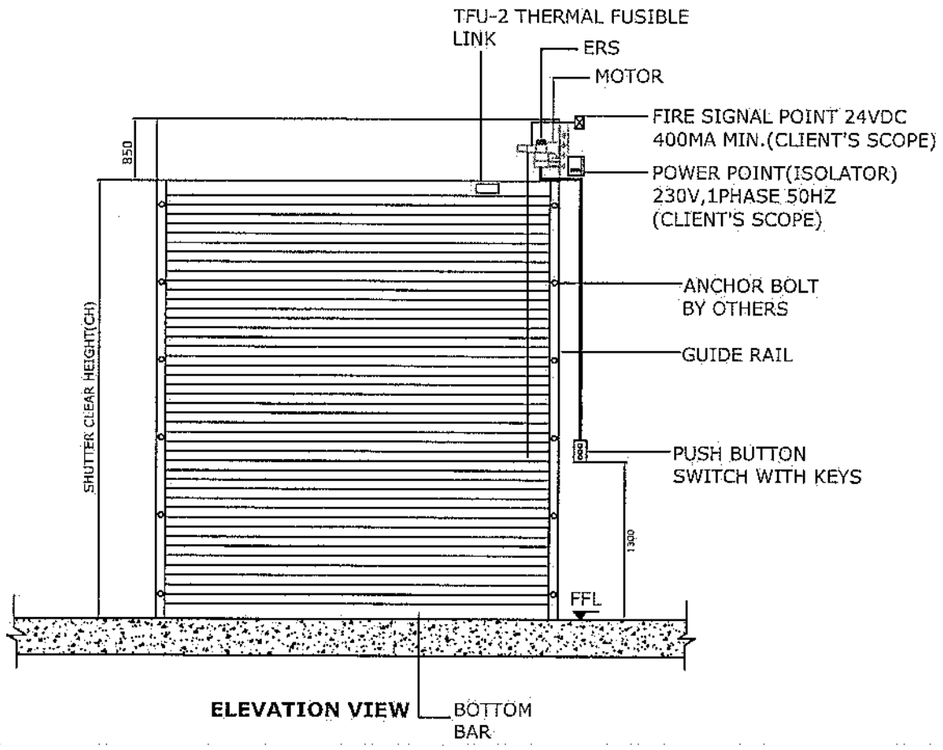

ELEVATION VIEW

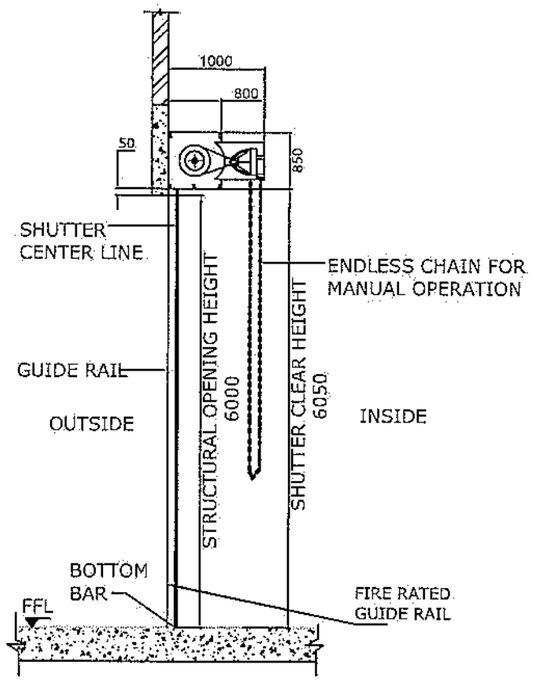


SIDE VIEW


SHUTTER TYPE	HIGH QUALITY 2HRS FIRE SHUTTERS
SHUTTER SLATS	1.0 mm GALVALUME STEEL SOLID SLATES
FINISHING OF SLATS	POWER COAT STANDARD RAL COLOUR
GUIDE RAIL	GALVANIZED ,3mm THICK
FINISHING OF GUIDE	POWDER COAT STANDARD RAL COLOUR
BOTTOM BAR	T-120
FINISHING OF B/BAR	POWDER COAT STANDARD RAL COLOUR
BOX DESIGN	MILD STEEL SECTION FRAME DESIGN
FINISHING OF BOX	POWDER COAT STANDARD RAL COLOUR
BOX COVER PLATE	0.8mm ZINCALUME STEEL SHEET
FINISHING OF COVER	POWDER COAT STANDARD RAL COLOUR
OPERATION	MOTORIZE WITH MANUAL OVERRIDE CHAIN
MOTOR POWER SOURCE	230 VOLTS,1 PHASE,50HZ
FIRE MODE	THERMAL FUSIBLE LINK WILL AUTO CLOSE BY GRAVITY FORCE
	WHWN ROOM TEMP RISES UP TO 68°C
	FIRE SIGNAL FROM FIRE CONTROL ROOM AND SHUTTER
	SHALL CLOSE DOWN BY GRAVITY FORCE WITHOUT DELAY

LOCATION	SHUTTER NO.	CLEAR WIDTH (STRUCTURE)	CLEAR HEIGHT (STRUCTURE)	QUANTITY	MOTOR POSITION
	FRS	4000 mm	6000mm	1	RH

Colour Code: RAL

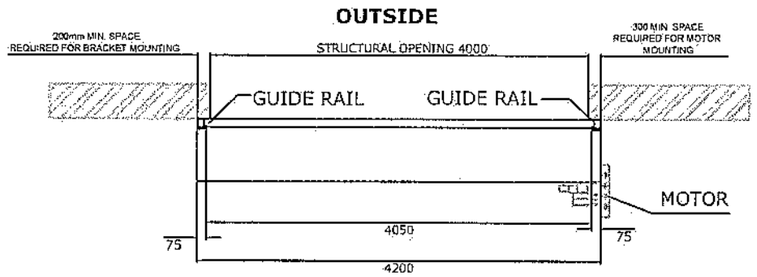


INSIDE
PLAN VIEW

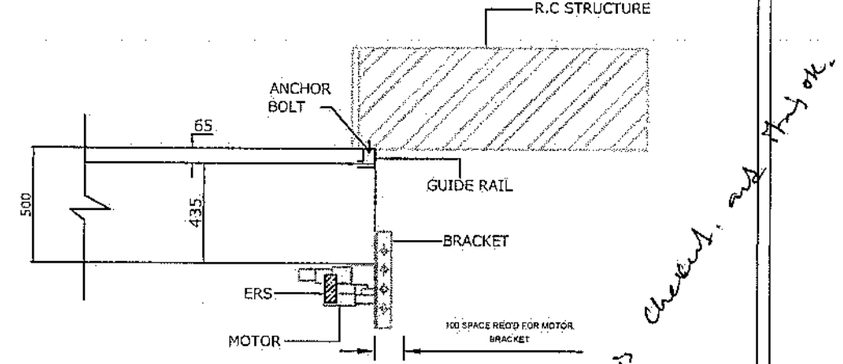


GUIDE & MOTOR ASSEMBLY DETAILS


Site is checked and Found ok.
For TPL

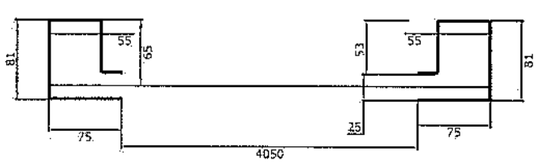

GALVANISED STEEL GUIDE RAIL
THICKNESS 3mm

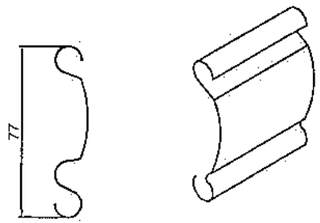

SHUTTER SLAT

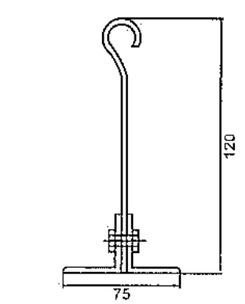

FIRE RATED BOTTOM BAR

LOCATION- TESTING BUILDING PAINT LAB.

This drawing & designing is the property of NIHVA TECHNOLOGIES. Not to be sold or copied to any other concern.

TITLE: FIRE RATED ROLLING SHUTTER

	SIGN	DATE
DRAWN	SURAJ	19/09/17
CHECK	SAGAR P.	19/09/17
REV.		
APPROVAL	SHEKHAR	19/09/17

If any queries contact : projects@nihva.com

ALL DIMENSION ARE IN mm

NIHVA TECHNOLOGIES PVT. LTD.
NIHVA TECHNOLOGIES PVT. LTD. PUNE
Tel : 020 66304033
Email:- info@nihva.com
Website - www.nihva.com

CLIENT - TATA PROJECTS LIMITED
PROJECT -ALSTOM
SITE - MADHEPURA, BIHAR.
DWG. NO. : NIHVA/17-18/0208
SCALE: NTS | WT. | SHEET: 01 OF 01