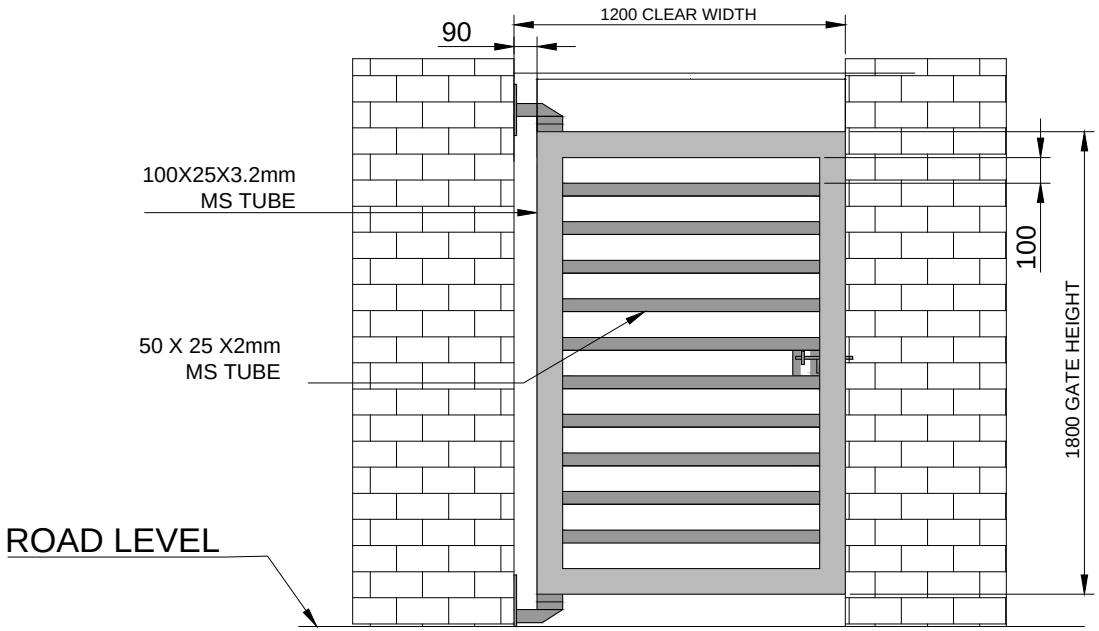

ELEVATION

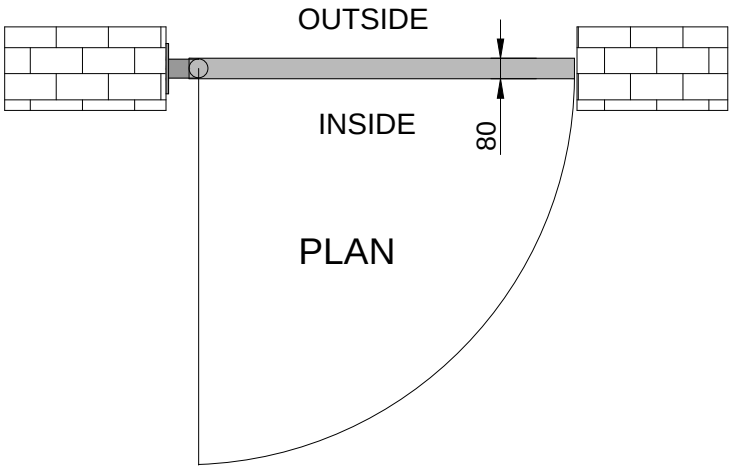

PLAN

SR NO	TUBE SPECIFICATION	
1	100X50X3.2mm	OUTER FRAME
2	50X25X2mm	INNER PATTERN

REV.01.- TUBE SIZE CHANGED

CLEAR WIDTH	CLEAR HEIGHT	QUANTITY
1200	1800	02 NOS

DIMENSION :

CLEAR WIDTH	CLEAR HEIGHT	QUANTITY
1200	1800	02 NOS

MATERIAL :

THICKNESS :

NOTE-
1. ALL REQUIRED CIVIL WORK WILL BE IN CLIENTS SCOPE.

NIHVA
NIHVA TECHNOLOGIES PVT. LTD.
NIHVA TECHNOLOGIES PVT. LTD. PUNE
Email:- info@nihva.com
Website:- www.nihva.com

TITLE:

WICKET GATE

CLIENT'S APPROVAL :

CLIENT - SHILCHAR TECHNOLOGIES LTD.

PROJECT -

SITE LOCATION -VADODARA

DWG. NO. : NIHVA/17-18/0159/R01

SCALE: NTS	WT:	SHEET:1 OF 1

DRAWN BY: OMKAR	DATE: 24-08-2017
CHECK BY: SHEKHAR	DATE: 24-08-2017
APPROVED BY : SHEKHAR	DATE: 24-08-2017

If any queries contact : projects@nihva.com

NOTE: ALL DIMENSIONS ARE IN mm

THIS DRAWING & DESIGNING IS THE PROPERTY OF NIHVA TECHNOLOGIES. NOT TO BE SOLD OR COPIED TO ANY OTHER CONCERN.