

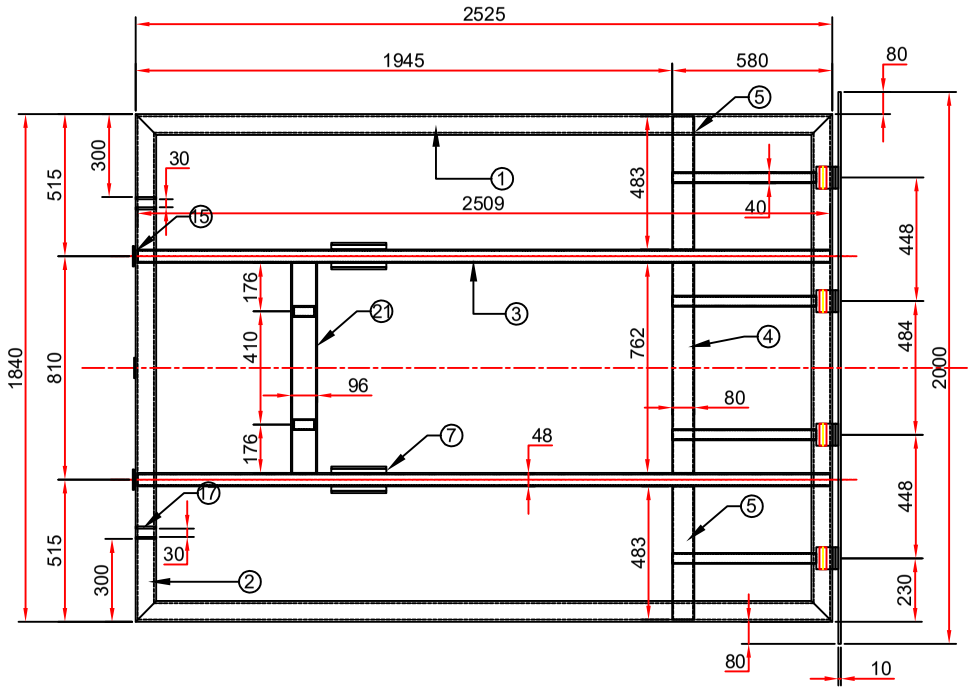


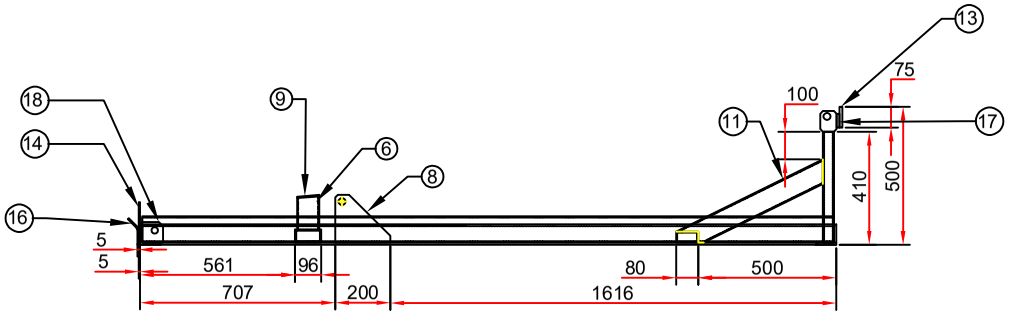

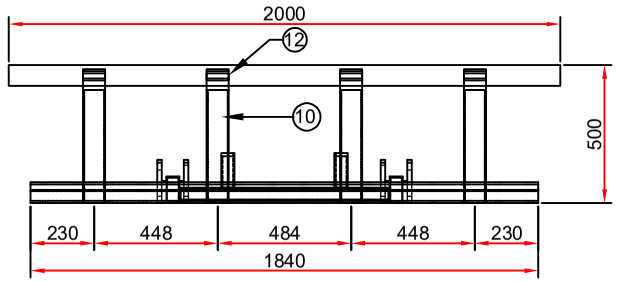

BOM			
SL NO.	DESCRIPTION	SPECIFICATION	QTY
1	ISA	75X75X8X2525	2NOS
2	ISA	75X75X8X1840	2NOS
3	RECT. TUBE	96X48X4.8X2509	2NOS
4	RECT. TUBE	80X40X4X762	1NOS
5	RECT. TUBE	80X40X4X483	2NOS
6	RECT. TUBE	80X40X4X125	2NOS
7	MS FLAT	75X16X200L	4NOS
8	CYLINEDER MTNG BKT	175X8X200L	4NOS
9	MS FLAT	50X5X80L	2NOS
10	RECT.TUBE	80X40X4X410	4NOS
11	RECT.TUBE	80X40X4X593	5NOS
12	MS BLOCK(DECK HLDNG BKT)	75X60X85	4NOS
13	MS FLAT	75X10X2000	1NO
14	MS FLAT	75X5X155	1NO
15	MS FLAT	50X5X75	2NOS
16	MS FLAT	75X5X185	2NOS
17	MS FLAT	50X10X100	4NOS
18	STOPPER BRACKET	75X75X8	4NOS
19	SQ TUBE	25X25X3X590	2NOS
20	MS ANGLE	75X75X8X30L	2NOS
21	RECT.TUBE	96X48X4.8X762	1NO

This drawing & design is the property of NIHVA TECHNOLOGIES. Not to be sold or copied to any other concern.

TITLE:- BASE FRAME

NIHVA TECHNOLOGIES PVT. LTD.

	NAME	DATE	SIGN
DRAWN	SUJATA	17/04/2023	
CHECK	A.K	17/04/2023	
APPRD.	V.T	17/04/2023	

CLIENT - ASIAN PAINT

LOCATION - MUMBAI

PRODUCT - DOCK LEVELER | QTY- 04

If any queries contact : design1@nihva.com | DWG NO:-NIHVA/22-23/MFG/0110 | REV- 0

ALL DIMENSION ARE IN mm | SCALE: NTS | SCALE:-- 1:1 | SHEET: 01 OF 01

Rev No.	Revision	Date	Revised By