

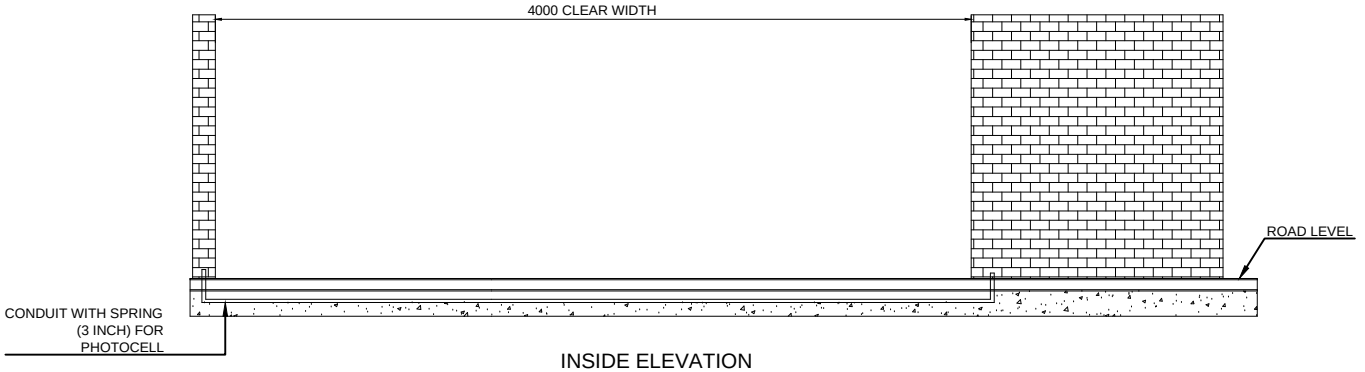


INSIDE ELEVATION

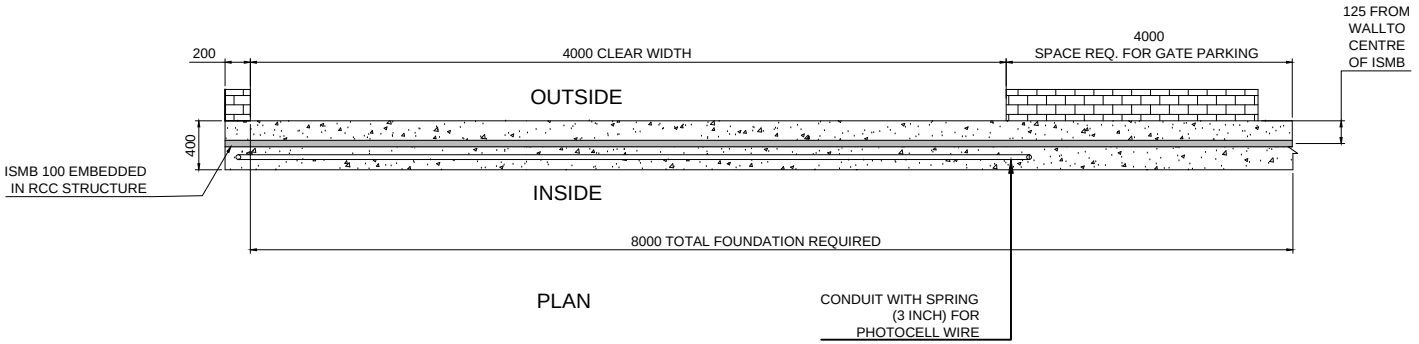

PLAN

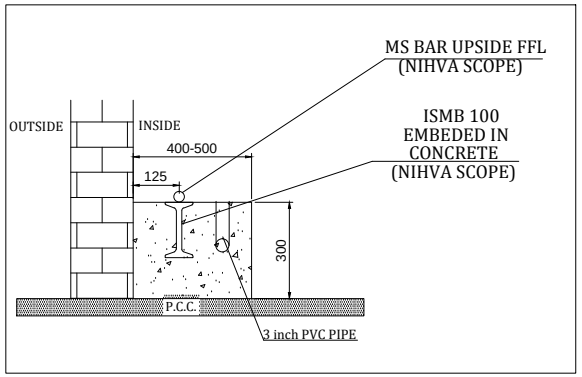

4.0m SLIDING GATE FOUNDATION

ISMB 100 X 50 X 8200L = 1 NO/GATE

REV NO	REV DATE	DRAWN	REMARK
R01	09.11.2019	P.V.A	1. ISMB CENTER DISTANCE CHANGE.

This drawing & design is the property of NIHVA TECHNOLOGIES. Not to be sold or copied to any other concern.

	NAME	SIGN	DATE
DRAWN	P.A		04.11.19
CHECK	G.J		04.11.19
REV.			
APPROVAL			

TITLE: FOUNDATION FOR 4M SLIDING GATE

If any queries contact : projects@nihva.com

ALL DIMENSION ARE IN mm

NIHVA TECHNOLOGIES PVT. LTD.
NIHVA TECHNOLOGIES PVT. LTD. PUNE
Tel : 020 66304033
Email:- info@nihva.com
Website:- www.nihva.com

CLIENT - DHAMALE

PROJECT -

SITE LOCATION - NIGADI, PUNE

DWG. NO. : NIHVA/19-20/0145/R01

SCALE: NTS | WT: | SHEET: 01 OF 01