

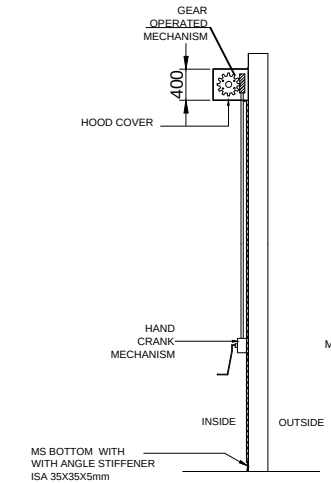



SIDE VIEW

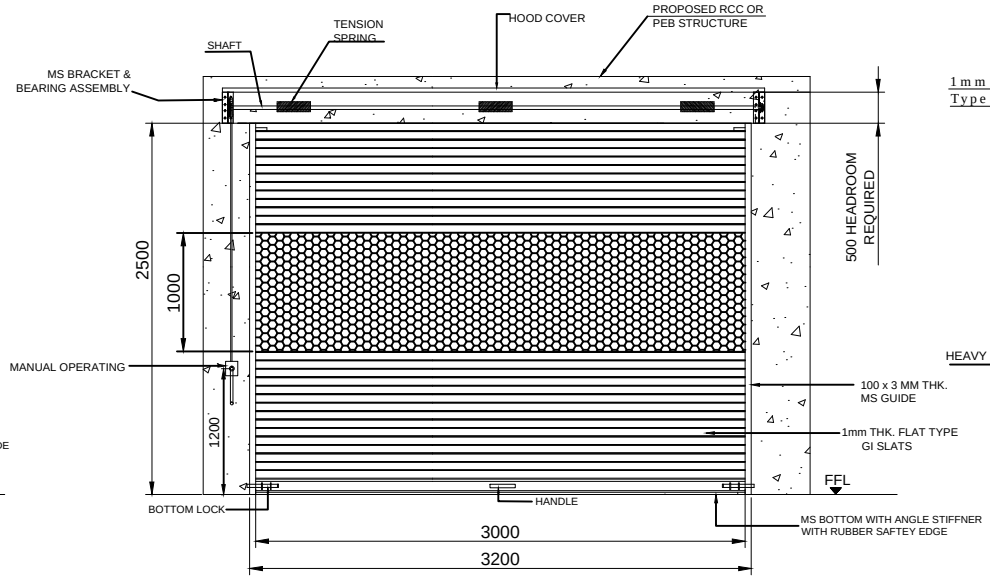


INSIDE ELEVATION

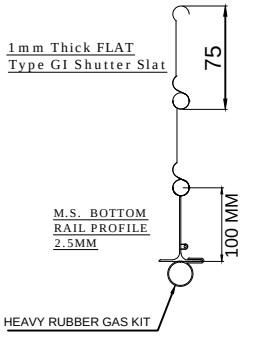


M.S. BOTTOM RAIL PROFILE 2.5MM

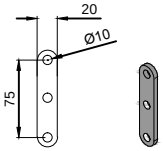


5mm THK. LINK

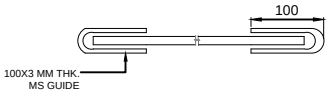

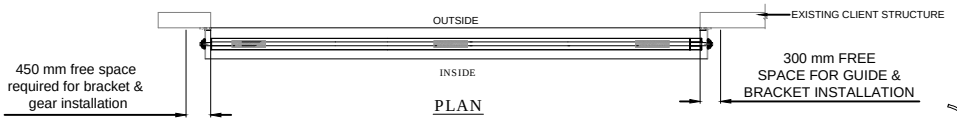

PLAN

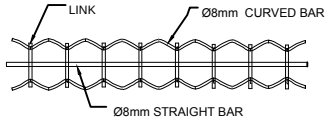

S.NO	FEATURE	EQUIPMENT DETAILS
01	SLATS MODEL	GALVANISE STEEL(GI) SLATS 1mm THK.
02	GUIDE RAIL	100 X 3mm THK MILD STEEL(MS).
03	BOTTOM RAIL	2.5mm THK MILD STEEL (M.S).
04	HOOD COVER	0.9mm THK GALVANISE STEEL (GI).
05	RAL COLOR	RAL 9002

SR.NO.	SIZE	QUANTITY
01	3000(W)X2470(H)	02 NOS

RAL COLOR
RAL 9002 (WHITE GREY)

SHUTTER LOCATION :- METER ROOM

NOTE-
1. ALL CIVIL WORK WILL BE CLIENT'S SCOPE.

SURAJ		R01	21/11/2018.	1.SHUTTER QTY. CHANGED 2.SHUTTER SIZE CHANGED
DRAWN NAME	SIGN	REVISION	DATE	REVISION DETAILS

TOLERANCE - ±10mm

This drawing & design is the property of NIHVA TECHNOLOGIES. Not to be sold or copied to any other concern.

TITLE
GEAR OPERATED ROLLING SHUTTER WITH GRILL.


	NAME	SIGN	DATE
DRAWN	SURAJ		03.10.2018
CHECK	PRADEEP		03.10.2018
APPRD.	DANGE		03.10.2018

If any queries contact : design@nihva.com


ALL DIMENSION ARE IN mm

NIHVA TECHNOLOGIES PVT. LTD.
NIHVA TECHNOLOGIES PVT. LTD. PUNE
Tel : 020 66304033
Email:- info@nihva.com
Website:- www.nihva.com


CLIENT -
PROJECT-
SITE LOCATION -
DWG. NO. : NIHVA/18-19/VDR/163/R01 | REV- 01
SCALE: NTS | WT: | SHEET: 01 OF 01

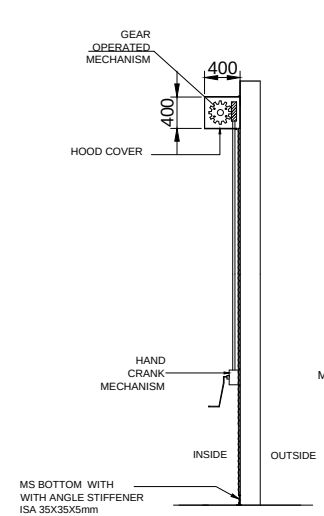


SIDE VIEW

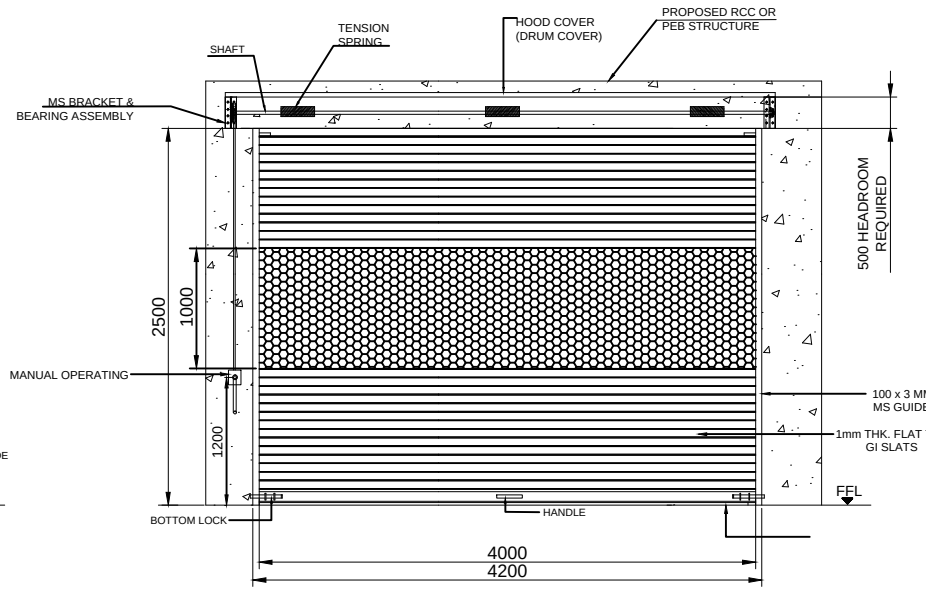


INSIDE ELEVATION

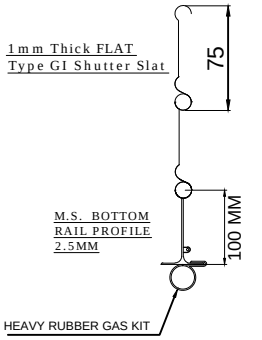


M.S. BOTTOM RAIL PROFILE 2.5MM

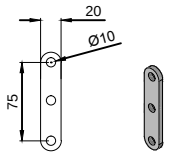


MS BOTTOM WITH ANGLE STIFFNER WITH RUBBER SAFTEY EDGE

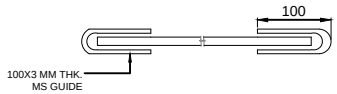

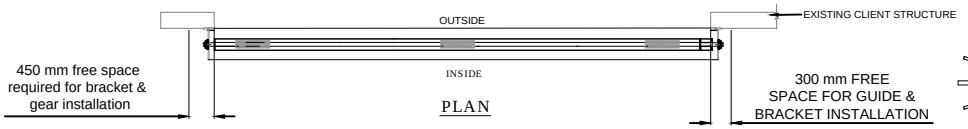

PLAN

5 m m THK. LINK

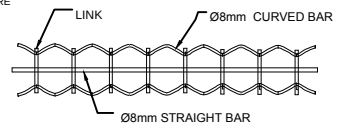

S.NO	FEATURE	EQUIPMENT DETAILS
01	SLATS MODEL	GALVANISE STEEL(GI) SLATS 1mm THK.
02	GUIDE RAIL	100 X 3mm THK MILD STEEL(MS).
03	BOTTOM RAIL	2.5mm THK MILD STEEL (M.S.).
04	HOOD COVER	0.9mm THK GALVANISE STEEL (GI).
05	RAL COLOR	RAL 9002

SR.NO.	SIZE	QUANTITY
01	4000(W)X2430(H)	01 NOS

RAL COLOR
RAL 9002 (WHITE GREY)

SHUTTER LOCATION :- R.M.U

SURAJ		R01	21/11/2018.	1.SHUTTER QTY. CHANGED 2.SHUTTER SIZE CHANGED
DRAWN NAME	SIGN	REVISION	DATE	REVISION DETAILS

NOTE-
1. ALL CIVIL WORK WILL BE CLIENT'S SCOPE.

TOLERANCE - ±10mm

This drawing & design is the property of NIHVA TECHNOLOGIES. Not to be sold or copied to any other concern.

TITLE
GEAR OPERATED ROLLING SHUTTER WITH GRILL.

NIHVA TECHNOLOGIES PVT. LTD.

NIHVA TECHNOLOGIES PVT. LTD. PUNE
Tel : 020 66304033
Website:- www.nihva.com
Email:- info@nihva.com

	NAME	SIGN	DATE
DRAWN	PRADEEP		03.10.2018
CHECK	SURAJ		03.10.2018
APPRD.	DANGE		03.10.2018

CLIENT -
PROJECT-
SITE LOCATION -
If any queries contact : design@nihva.com
DWG. NO. : NIHVA/18-19/VDR/164/R01
REV- 01
ALL DIMENSION ARE IN mm
SCALE: NTS
WT:
SHEET: 01 OF 01