


DRAWING

REV DESCRIPTION	DATE	REV NO
	26-03-2026	REV 00
1.		

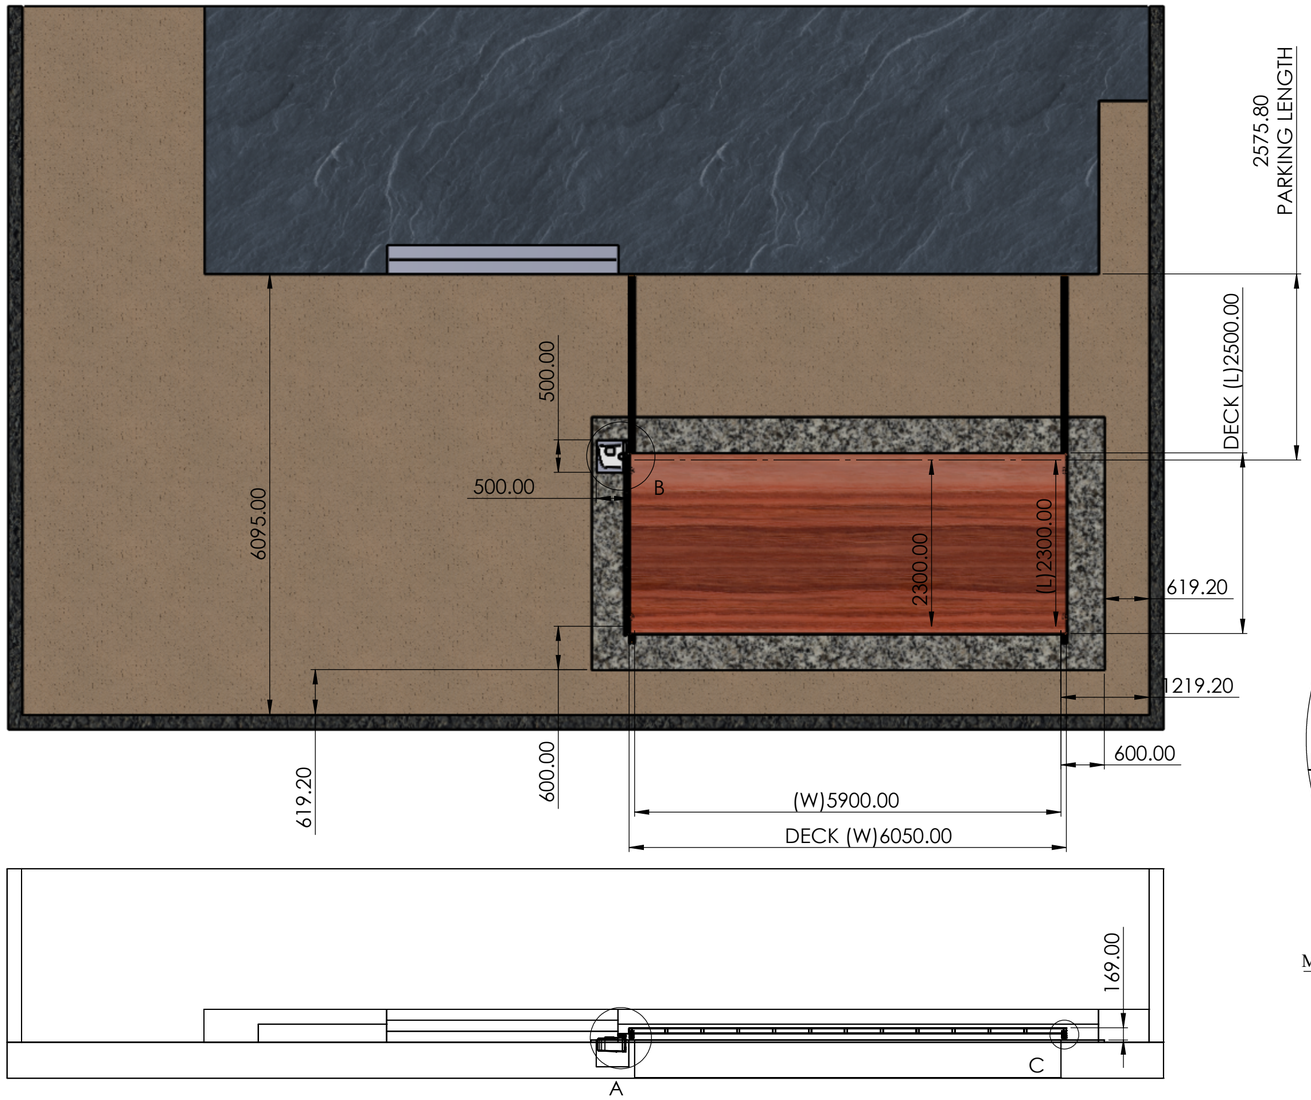


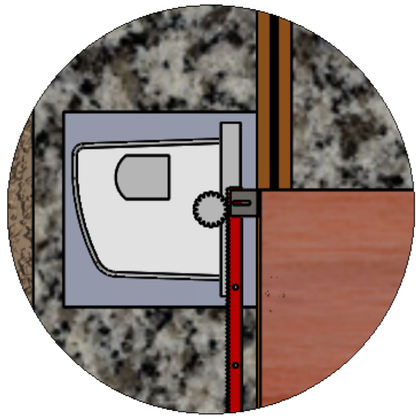

DETAIL B
SCALE 1 : 10

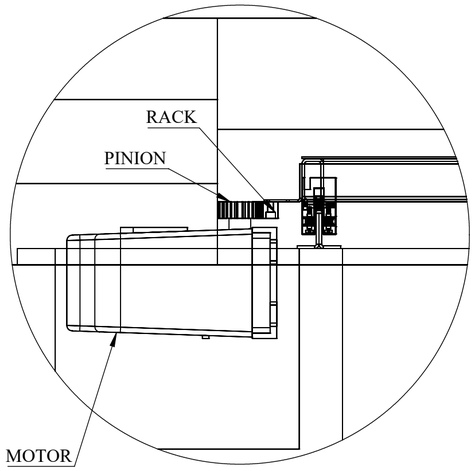

DETAIL A
SCALE 1 : 8

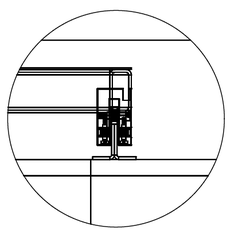

DETAIL C
SCALE 1 : 8

NOTE :

GA DRAWING

SPECIAL INSTRUCTION'S :

TITLE - ROOF AUTOMATION

DWG NO - NTPL-000

NIHVA TECHNOLOGIES PVT.LTD.PUNE
Website - www.nihva.com


	NAME	SIGNATURE	DATE
DRAWN	V.W.		26-03-2026
CHK'D	B.S.		27-03-2026
APPV'D	V.T.		27-03-2026

PRODUCT -
PROJECT NO - NTPL-000
REVISION - 00
SITE LOCATION -
WEIGHT -
MATRIAL -
QTY - 1
SCALE :
PROJECTION METHOD:
SHEET 1 OF 2

If any queries contact - info@nihva.com
ALL DIMENSION ARE IN mm
A2

DRAWING

REV DESCRIPTION	DATE	REV NO
	26-03-2026	REV 00
1.		

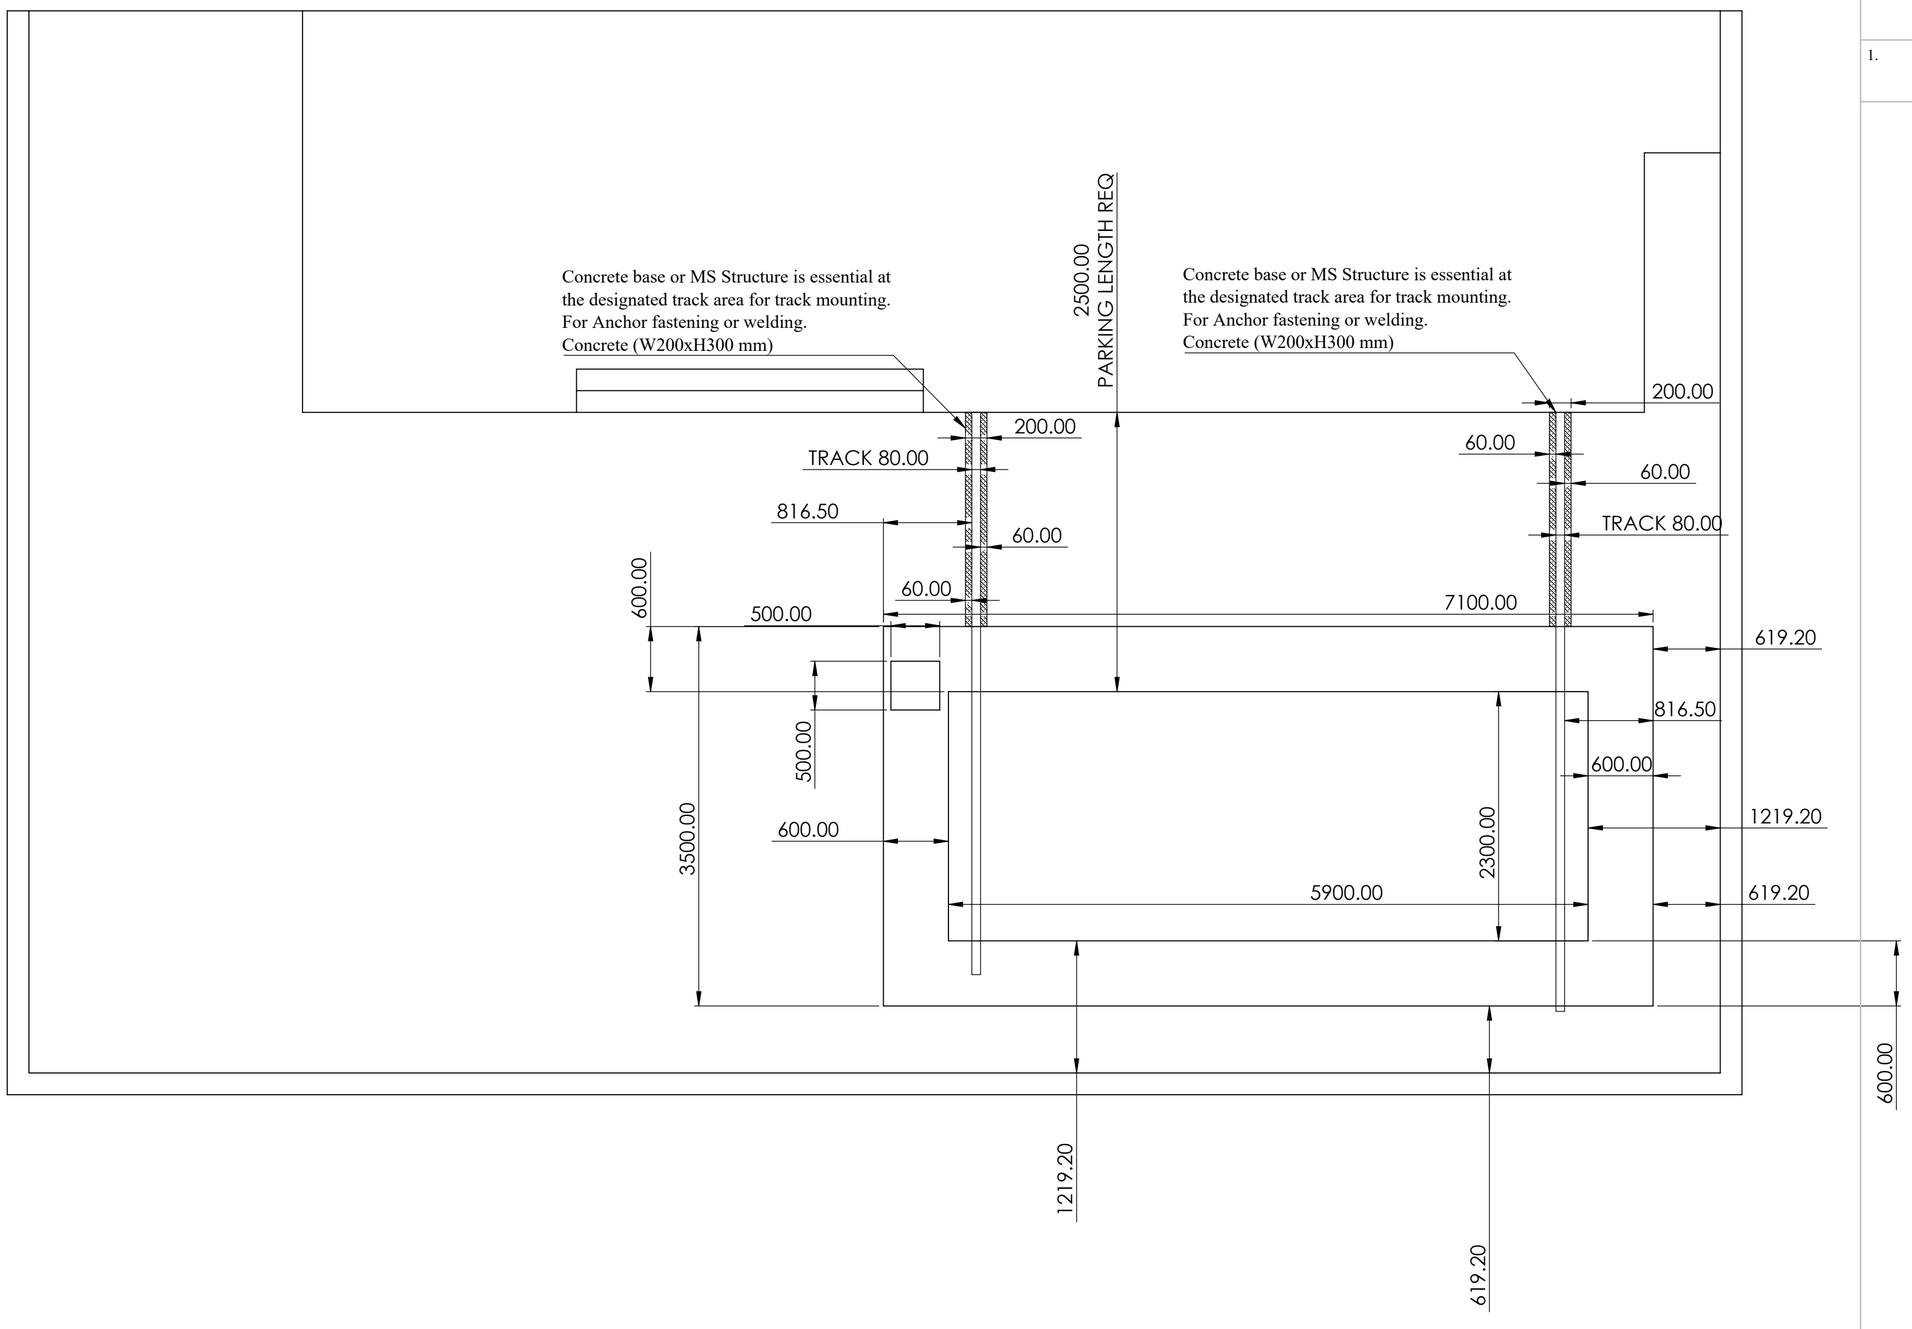

NOTE :

CIVIL DRAWING

SPECIAL INSTRUCTION'S :

TITLE - ROOF AUTOMATION

DWG NO - NTPL-000

NIHVA Technologies Pvt. Ltd.

NIHVA TECHNOLOGIES PVT.LTD.PUNE
Website - www.nihva.com

	NAME	SIGNATURE	DATE
DRAWN	V.W.		26-03-2026
CHK'D	B.S.		27-03-2026
APPV'D	V.T.		27-03-2026

If any queries contact - Design@nihva.com

ALL DIMENSION ARE IN mm | A2

PRODUCT -

PROJECT NO - NTPL-000 | REVISION - 00

SITE LOCATION - | WEIGHT -

MATRIAL - | QTY - 1

PROJECTION METHOD:

SCALE :