



ELEVATION

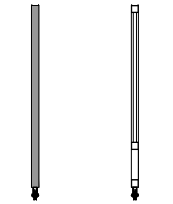

SIDE VIEW DETAIL A-'A'

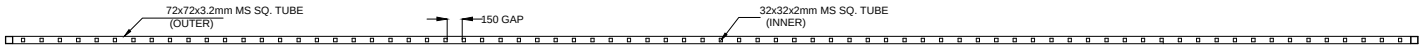

PLAN

SR NO	TUBE SPECIFICATION		MATERIAL	QTY
1	72X72X3.2mm MS TUBE	OUTER FRAME	MILD STEEL	45.6 MTR
2	32X32X2mm MS TUBE	INNER PATTERN	MILD STEEL	90 MTR
3	150mm	GAP BETWEEN TUBES	-	-
4	0.9mm THK	MS SHEET	MILD STEEL	14 X 0.3 MTR

TOLERANCE:- ± 10mm

CLEAR WIDTH (CW)	CLEAR HEIGHT (CH)	QUANTITY
14000mm	1800mm	1 NOS

DIMENSION :

CLEAR WIDTH	CLEAR HEIGHT	QUANTITY
14000mm	1800mm	1 NOS

MATERIAL: MS

THICKNESS :

NOTE-
1. ALL REQUIRED CIVIL WORK WILL BE IN CLIENTS SCOPE.
2. ONE COAT OF RED OXIDE & TWO COAT OF APPROVED RAL SHADE WILL BE GIVEN TO THE GATE.

NIHVA
NIHVA TECHNOLOGIES PVT. LTD.
Website:- www.nihva.com
NIHVA TECHNOLOGIES PVT. LTD. PUNE
Email:- info@nihva.com
TEL :020 66304033

TITLE:

SLIDING GATE LEAF

CLIENT'S APPROVAL :

CLIENT - INOX

PROJECT -

SITE LOCATION -CHENNAI

DWG. NO. : NIHVA/18-19/VDR/170

SCALE: NTS	WT:	SHEET:1 OF 1

	NAME	SIGN	DATE
DRAWN	SURAJ		10-10-2018
CHECK	PRADEEP		10-10-2018
APPROVED	R.D		10-10-2018

IF ANY QUERIES CONTACT:- design@nihva.com

NOTE: ALL DIMENSIONS ARE IN mm

THIS DRAWING & DESIGN IS THE PROPERTY OF NIHVA TECHNOLOGIES. NOT TO BE SOLD OR COPIED TO ANY OTHER CONCERN.