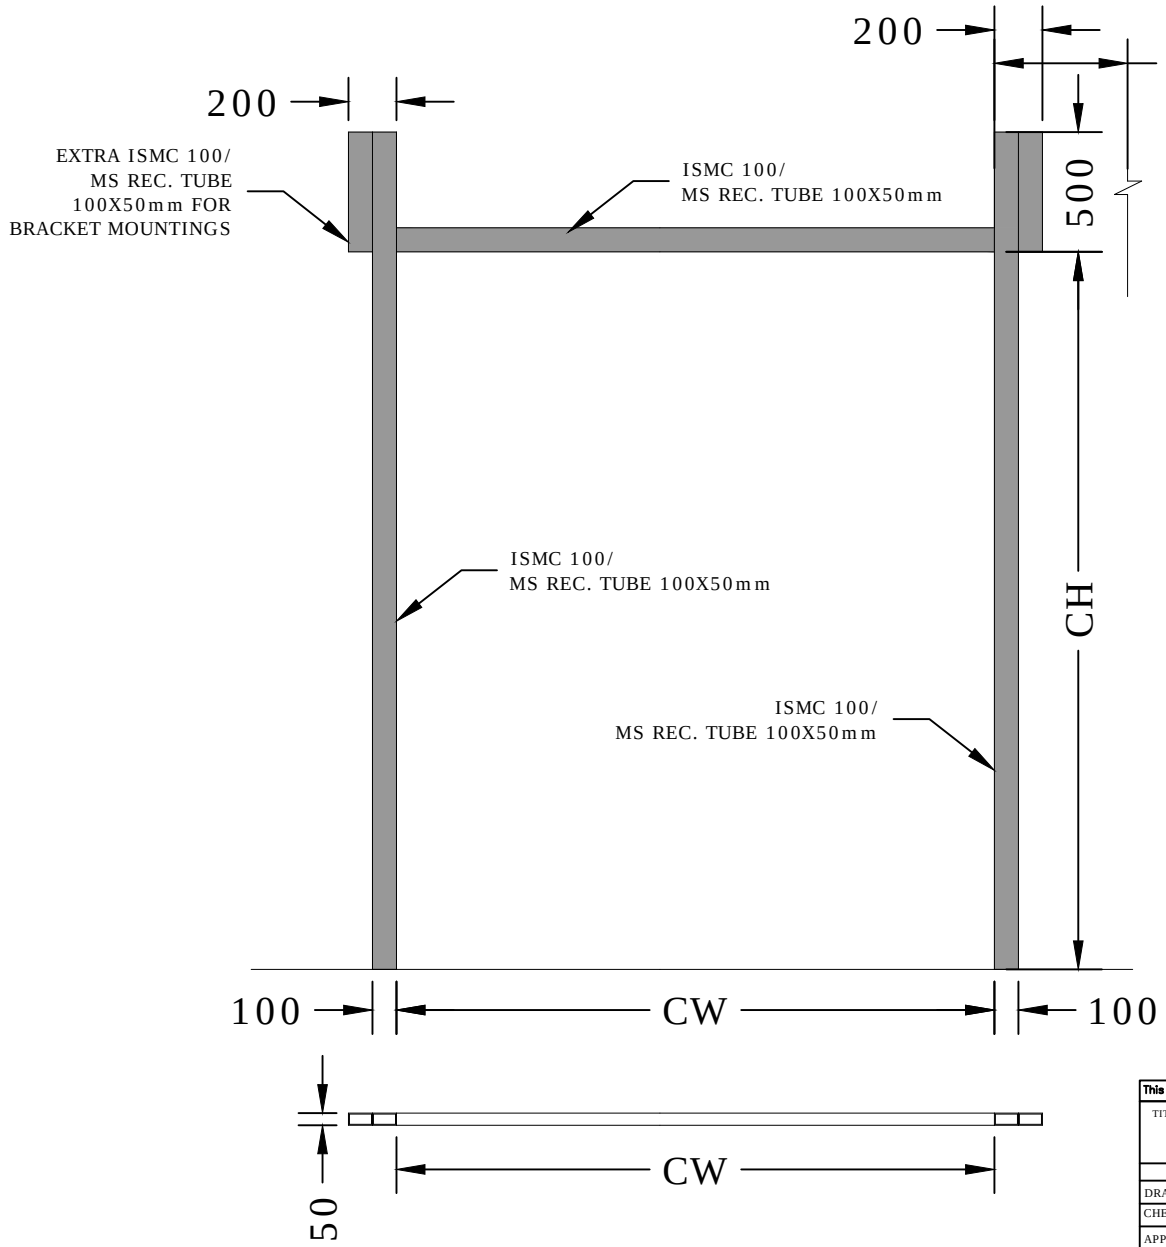

REV NO	DATE	DESCRIPTION
REV -0	03-02-2018	INITIAL DRAWING
REV -1	05-02-2018	SHUTTER HEIGHT & WIDTH REVISED LOCATIONS SPECIFIED

CLEAR WIDTH (CW)	CLEAR HEIGHT (CH)	LOCATION	QUANTITY
3000 mm	3500 mm	BWS 1 BALSA	1 NOS
2895 mm	3530 mm	BWS 2 BALSA	1 NOS

This drawing & design is the property of NIHVA TECHNOLOGIES. Not to be sold or copied to any other concern.

TITLE: MS STRUCTURE FOR DOUBLE WALL ROLLING SHUTTER 2

	SIGN	DATE
DRAWN	OMKAR	03/02/18
CHECK	SHEKHAR	03/02/18
APPROVAL	SHEKHAR	03/02/18

NIHVA TECHNOLOGIES PVT. LTD.
NIHVA TECHNOLOGIES PVT. LTD. PUNE
Tel : 020 66304033
Email:- info@nihva.com
Website:- www.nihva.com

CLIENT - LM WIND POWER BLADES (INDIA) PVT. LTD.
PROJECT -
SITE - BANGLORE

If any queries contact :design@nihva.com
DWG. NO. : NIHVA/17-18/0348 REV- 1
ALL DIMENSION ARE IN mm
SCALE: NTS WT: SHEET: 01 OF 01