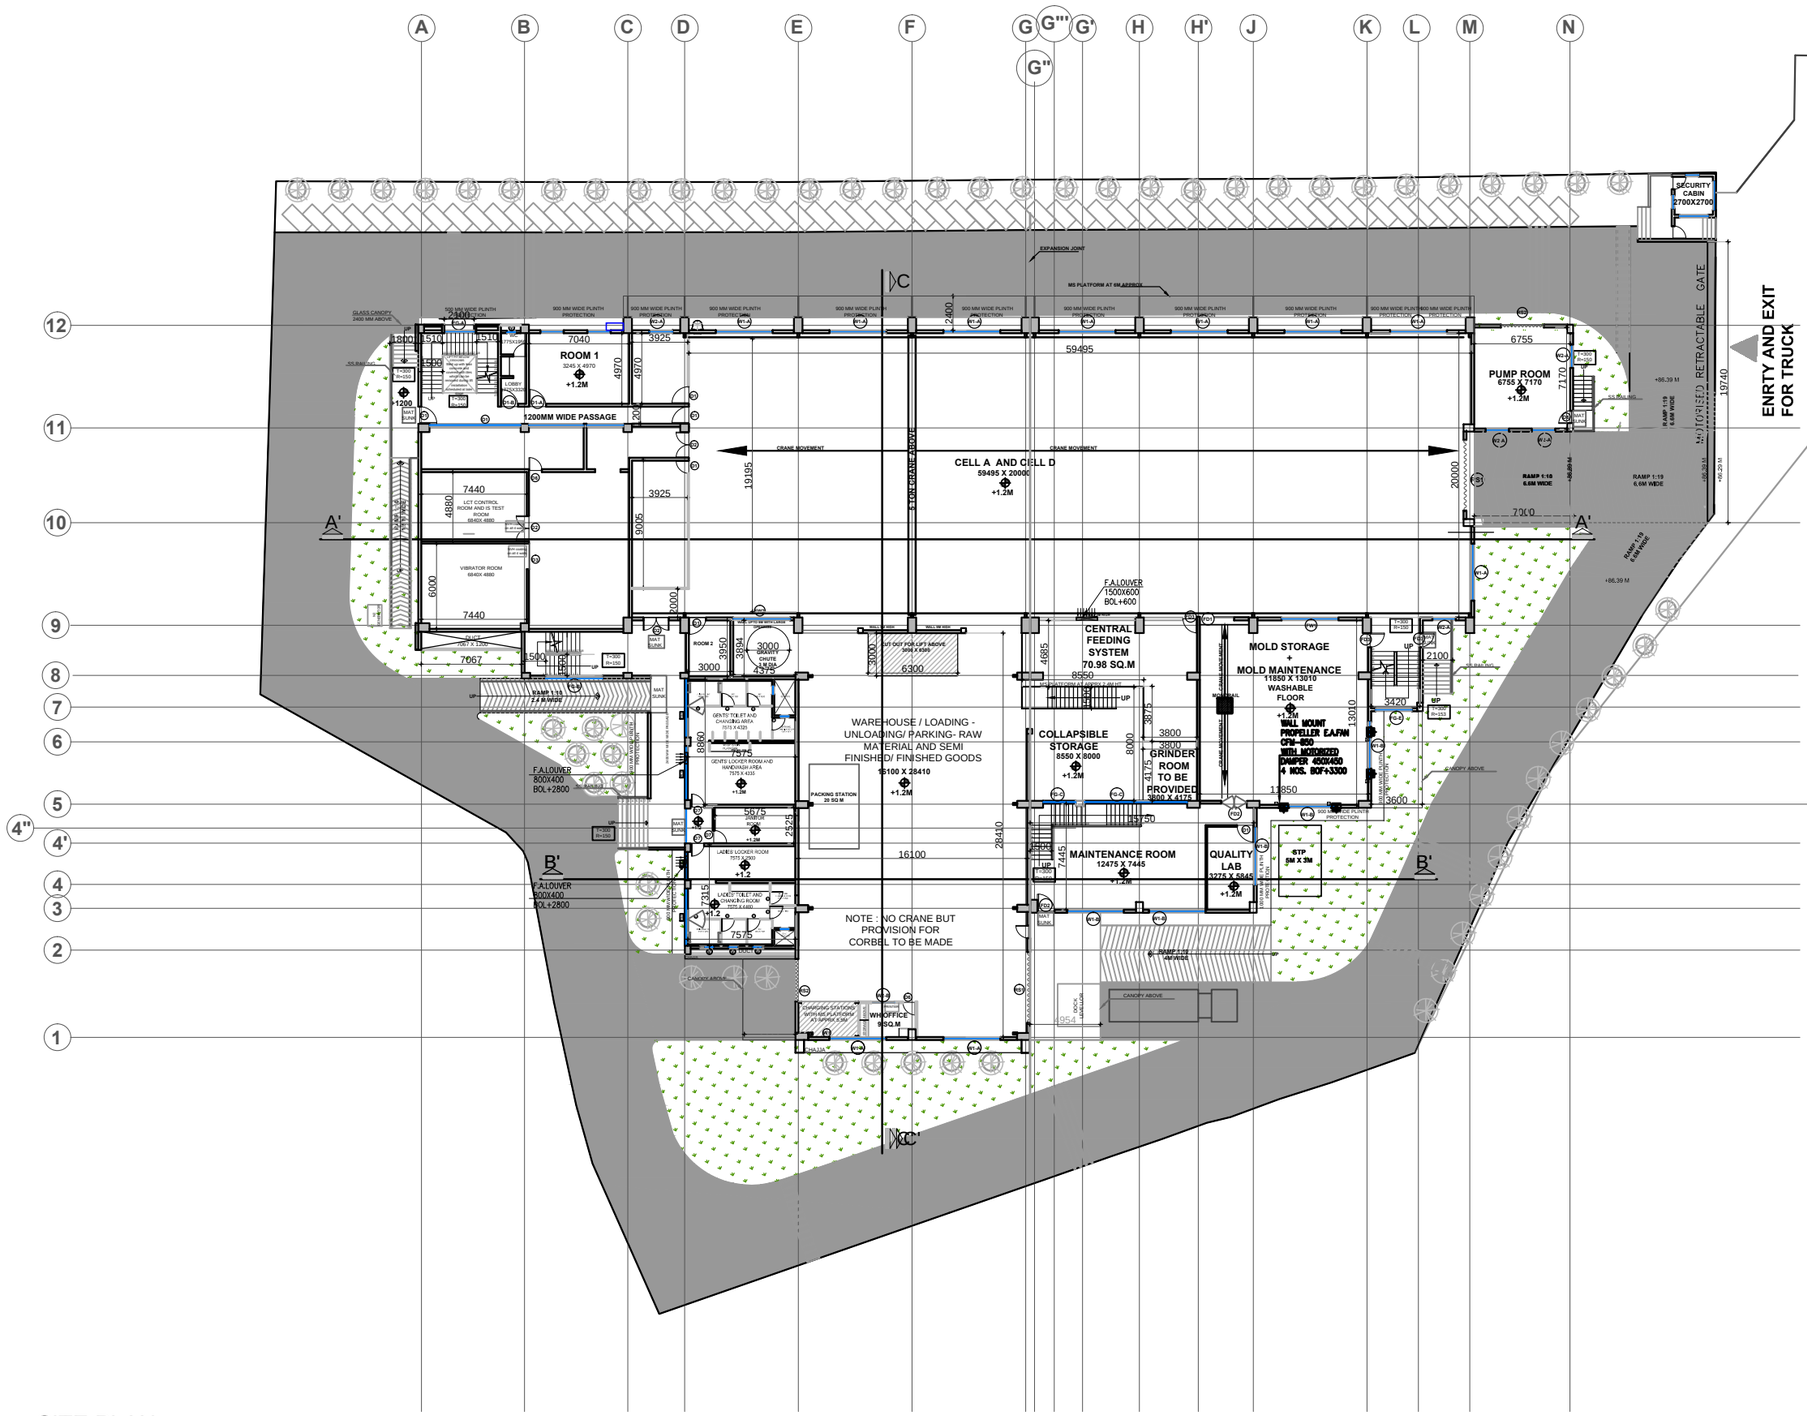


SITE PLAN
SCALE - 1:400

P R O J E C T -

GREENFIELD MANUFACTURING BUILDING
AT E7/A2, CHAKAN MIDC PHASE III, PUNE.

O W N E R -

ARAYMOND FASTENERS
INDIA PVT LTD

D R A W I N G -

TENDER DRAWING - LAYOUT PLAN

SACHIN P. MUJUMDAR
REGD. ARCHITECT CA/90/13058

• DEVEN V. GHOTGE
REGD. ARCHITECT CA/90/12774

FOUNDER PARTNER
LATE SHRI.ABHAY B. SHARMA
LATE SHRI.VIJAY V. GHOTGE

DESIGNED BY: ARCHITECTS UNITED
111/9, 14th Lane Prabhat Road, Pune-411 004
Ph.25441426 E-MAIL:au@architectsunited.co.in

SCALE	DATE	DRAWN BY
AS SPECIFIED	23.03.2019	MEENAKSHI

REVISION

RVN. NO.	DATE	DRAWN BY

NORTH

job no.-
16_20_A10
drg no.-
3002
drg nm.-
16_20_A10_TD_AU_PB_LP_001

NOTES

1) DO NOT SCALE THE DRAWING.
2) WRITTEN DIMENSIONS ARE TO BE FOLLOWED.
3) DISCREPANCY, IF ANY, PLEASE REFER IT TO THE ARCHITECT.
4) CONTRACTOR SHOULD CHECK AND VERIFY THE DRAWING.

PROJECT CONSULTANTS

P M C :
J L L
Lvl 6, Amar Avinash Corporate Plaza,11 Bund Garden Rd,Pune 001
EMAIL - abhay.tiwari@ap.jll.com CONTACT -+91 8805181200

S T R U C T U R A L : -
KEDAR PHADNIS
103,Ganesh Apts,Off Karve Road, Behind Ashtekar Jewellers, Pune-411004
EMAIL - kedarphadnis@yahoo.com CONTACT -+91 9423012603


P L U M B I N G : -
McLIN CONSULTANTS PVT. LTD.
Sirijaõ 5, Sitabaug Colony, Vitthalwadi Road, Pune - 411 030.
EMAIL - mclinpl@gmail.com CONTACT - 020 - 2432 0010 / 2432 4859

FIRE PROTECTION : -
EXPERT_TECH SYSTEMS
51/43, Navsahyadri Society,Karvenagar, Pune 411 052.
EMAIL - etsjdr@gmail.com CONTACT - +91 9371008098

H V A C : -
R.S.KULKARNI HVACR CONSULTING ENGINEERS
512 + 513, Siddharth Tower,Sangam Press Road, Kothrud,Pune I 411029
EMAIL - rskulkarni@rskhvacr.com CONTACT - 020-41315512/13/14/15

E L E C T R I C A L : -
VIDYUT SALLAGAR PVT. LTD.
Savitri, 113 Vinayak Society, Sahakarnagar, Pune - 411 009
EMAIL - vidyutsallagar@gmail.com CONTACT - : 020 24224534

L E E D : -
GREEN DESIGN CONSULTANCY
112 / 8, Vasundhara Apartments, 14th lane, Prabhat Road, Pune - 411 004
EMAIL - greenprojects13@gmail.com CONTACT - : +91 9881371403

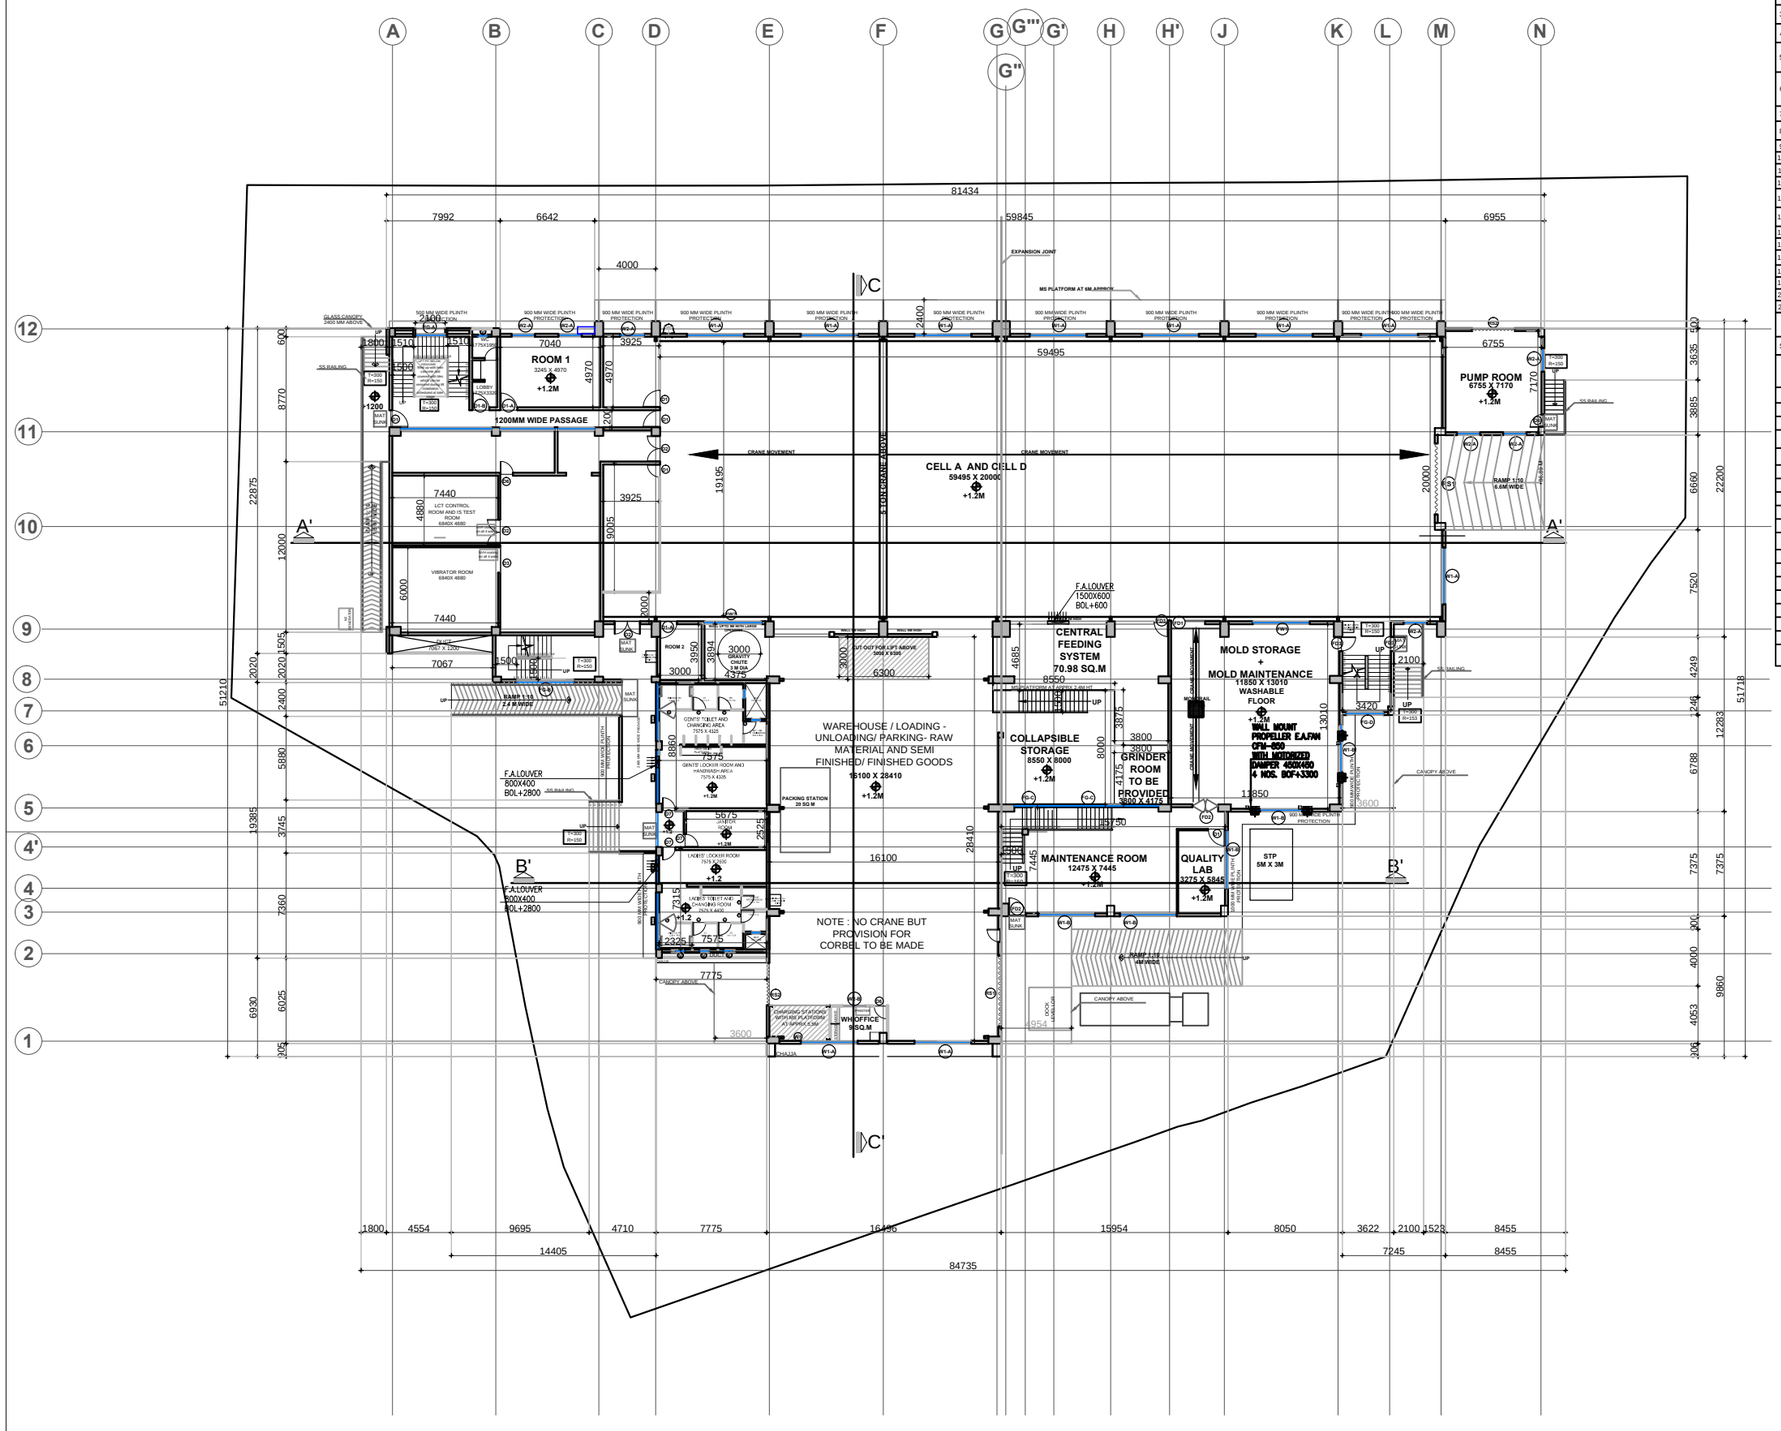

GROUND FLOOR PLAN
SCALE - 1:400

DOOR SCHEDULE				
SR NO	TYPE	SIZE(IN M)	NOS	DESCRIPTION
1	D1	1.2X2.4	5	1200 mm wide single leaf glass door openable
2	D1-A	1.2 X 2.4	3	metal door with vision panel
3	D1-B	1.2 x 2.4	1	Single leaf flush door
4	D2	1.8X2.4	10	Double leaf metal door with vision panel.
5	D3	1.8X2.4	1	Thick metal sliding door acoustical and vibration proof.
6	D4	0.9X2.4	1	security cabin door
7	D5	1.2X2.4	2	Single leaf flush door - both side swing.
8	D6	0.9X2.4	4	Metal door 300 X 300 vision panel.
9	D7	0.9X2.4	15	Single leaf flushdoor.
10	D8	0.9X2.4	1	Access control door
11	D9	0.9 x 2.4	1	Wicket gate
12	FD1	3.0X2.4	1	Fire rated sliding door.
13	FD2	1.8X2.4	2	Double leaf fire rated with vision panel,metal.
14	FD3	1.0X2.4	8	Fire rated single leaf door with vision panel.
15	RS-1	5.0X7.0	2	Motorized rolling shutter.
16	RS-2	3.0X3.0	2	Motorized rolling shutter.
17	RS-3	3.0 X 3.0	1	Motorized rolling shutter with collapsible door on outer side
18	RS-4	5.0X3.0	1	Motorized rolling shutter.
19	RRS-1	2.4X3.0	4	Rapid rolling shutter.
20	RRS-2	1.8X3.0	2	Rapid rolling shutter.
21	GATE	18M WIDE	1	Motorized Retractable gate

WINDOW SCHEDULE

SR.NO.	TYPE	SIZE(IN M)	NOS.	DESCRIPTION
1	W1-A	4.00X1.8	10	2 track aluminium window with fixed glass in between and louvers at bottom 600mm.
2	W1-B	4.00X1.8	9	2 track aluminium window fire rated
3	W1-C	6.20X2.25	8	Double glass unit (DGU)
	W1-C'	6.20X2.25	9	Sliding window
4	W2-A	1.65X1.8	9	2track aluminium window with louvers at bottom
5	W2-B	1.65X1.8	1	2track aluminium window sliding.
6	W2-C	2.20X2.25	2	Sliding window
7	W3	900 X 1500	2	Openable window
8	W4	4.0 X 600	1	Gravity louvers
9	FW-1	4.00X 1.8	1	Fixed firerated glass window.
10	FW-2	4.00X1.8	13	Fixed glass window.
11	FW-3	2.0 X 1.5	2	Fixed glass, aluminium frame security cabin)
12	FG	3.43X7.96	1	Structural glazing.
13	FG-A	2.10X3.30	3	Fixed glass.
14	FG-B	4.00 X14.05	1	Structural glazing.
15	FG-C	4.50 X length	6	Fixed glass.
16	FG-D	2.55X3.30	4	Fixed glass.
17	FG-E	13.03X2.30	2	D.G.U
18	FG-F	6.36X2.30	2	D.G.U
19	V	0.6X0.9	6	Louvers

P R O J E C T -

GREENFIELD MANUFACTURING BUILDING AT E7/A2, CHAKAN MIDC PHASE III, PUNE.

O W N E R -

ARAYMOND FASTENERS INDIA PVT LTD

D R A W I N G -

TENDER DRAWING - GROUND FLOOR PLAN

SACHIN P. MUJUMDAR
REGD. ARCHITECT CA/90/13058

• DEVEN V. GHOTGE
REGD. ARCHITECT CA/90/12774

FOUNDER PARTNER
LATE SHRI.LABHAY B. SHARMA
LATE SHRI.VIJAY V. GHOTGE

DESIGNED BY: ARCHITECTS UNITED
111/9, 14th Lane Prabhat Road, Pune-411 004
Ph.25441426 E-MAIL:au@architectsunited.co.in

SCALE	DATE	DRAWN BY
AS SPECIFIED	23.03.2019	MEENAKSHI

REVISION

RVN. NO.	DATE	DRAWN BY

NORTH

job no.- 16_20_A10
drg no.- 3006
drg nm.- 16_20_A10_TD_AU_PB_GF_005

NOTES
1) DO NOT SCALE THE DRAWING.
2) WRITTEN DIMENSIONS ARE TO BE FOLLOWED.
3) DISCREPANCY, IF ANY, PLEASE REFER IT TO THE ARCHITECT.
4) CONTRACTOR SHOULD CHECK AND VERIFY THE DRAWING.

PROJECT CONSULTANTS

P M C : -
J L L
Lvl 6, Amar Avinash Corporate Plaza,11 Bund Garden Rd,Pune 001
EMAIL -abhay.tiwari@ap.jll.com CONTACT -+91 8805181200

S T R U C T U R A L : -
KEDAR PHADNIS
103,Ganesh Apts,Off Karve Road, Behind Ashtekar Jewellers, Pune-411004
EMAIL - kedarphadnis@yahoo.com CONTACT -+91 9423012603


P L U M B I N G : -
McLIN CONSULTANTS PVT. LTD.
Girijia0 5, Sitabaug Colony, Vitthalwadi Road, Pune - 411 030.
EMAIL - mclinpl@gmail.com CONTACT -020 - 2432 0010 / 2432 4859


FIRE PROTECTION : -
EXPERT_TECH SYSTEMS
51/43, Navsahyadri Society,Karvenagar, Pune 411 052.
EMAIL - etsjdr@gmail.com CONTACT - +91 9371008098

H V A C : -
R.S.KULKARNI HVACR CONSULTING ENGINEERS
512 + 513, Siddharth Tower,Sangam Press Road, Kothrud,Pune 1 411029
EMAIL - rskulkarni@rskhvacr.com CONTACT - 020-41315512/13/14/15

E L E C T R I C A L : -
VIDYUT SALLAGAR PVT. LTD.
Savitri, 113 Vinayak Society, Sahakarnagar, Pune - 411 009
EMAIL - vidyutsallagar@gmail.com CONTACT - : 020 24224534

L E E D : -
GREEN DESIGN CONSULTANCY
112 / 8, Vasundhara Apartments, 14th lane, Prabhat Road, Pune - 411 004
EMAIL - greenprojects13@gmail.com CONTACT - : +91 9881371403

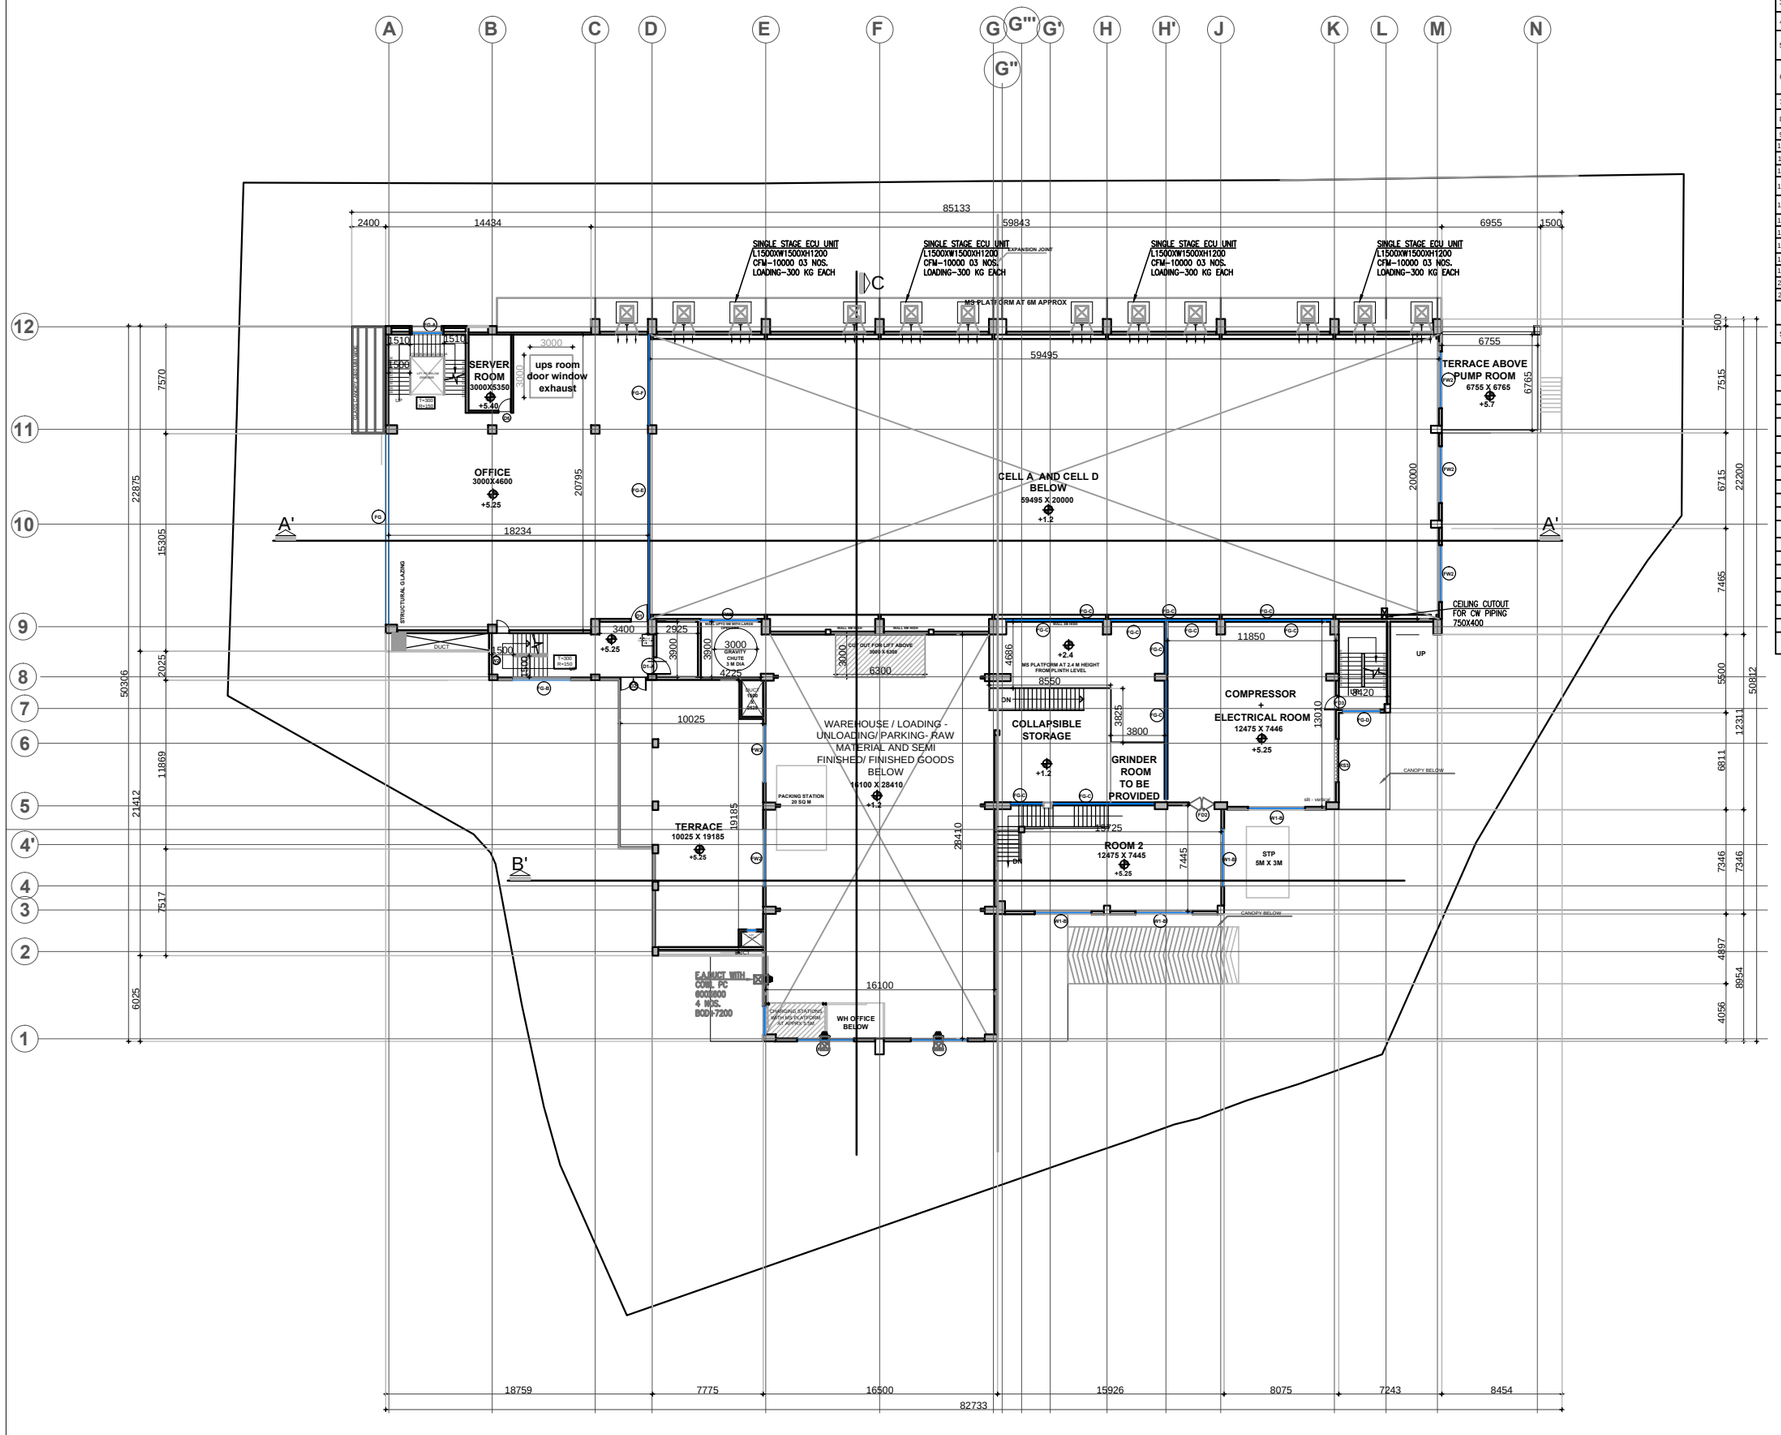
A
B
C
D
E
F
G
G'''
G''
G'
H
H'
J
K
L
M
N
12
11
10
9
8
7
6
5
4'
4
3
2
1
A'
B'
SINGLE STAGE ECU UNIT L1500XW1500XH1200 CFM-10000 03 NOS. LOADING-300 KG EACH
EXPANSION JOINT
MS PLATFORM AT 6M APPROX
SERVER ROOM 3000X5350 +5.40
ups room door window exhaust
OFFICE 3000X4600 +5.25
CELL A AND CELL D BELOW 59495 X 20000 +1.2
TERRACE ABOVE PUMP ROOM 6755 X 6765 +5.7
CEILING CUTOUT FOR CW PIPING 750X400
STRUCTURAL GLAZING
DUCT
UP
COMPRESSOR + ELECTRICAL ROOM 12475 X 7446 +5.25
COLLAPSIBLE STORAGE +1.2
GRINDER ROOM TO BE PROVIDED
MS PLATFORM AT 2.4 M HEIGHT FROM PLINTH LEVEL +2.4
WAREHOUSE / LOADING - UNLOADING/ PARKING- RAW MATERIAL AND SEMI FINISHED/ FINISHED GOODS BELOW 16100 X 28410 +1.2
TERRACE 10025 X 19185 +5.25
PACKING STATION 20 SQ M
ROOM 2 12475 X 7445 +5.25
STP 5M X 3M
CANOPY BELOW
E.A.HUCT WITH COIL PC 6000800 4 NOS. BOD=7200
WH OFFICE BELOW
85133
59843
59495
14434
2400
6955
1500
6755
18234
10025
16100
82733
18759
7775
16500
15926
8075
7243
8454
22875
15305
7570
2025
5030.6
11869
21412
7517
6025
20795
20000
6765
22200
6715
7515
500
7485
5500
5080.2
1231.1
6811
7346
7346
4897
8954
4056
13010
11850
8550
6300
4686
3800
3805
4725
2925
3400
2400
1510
1500
3000
3600
1200
1100
1800
1350
1400
500
2025
19185
28410
12475
7445
4600
4000
3000
3600
3800
3000
3000
3000

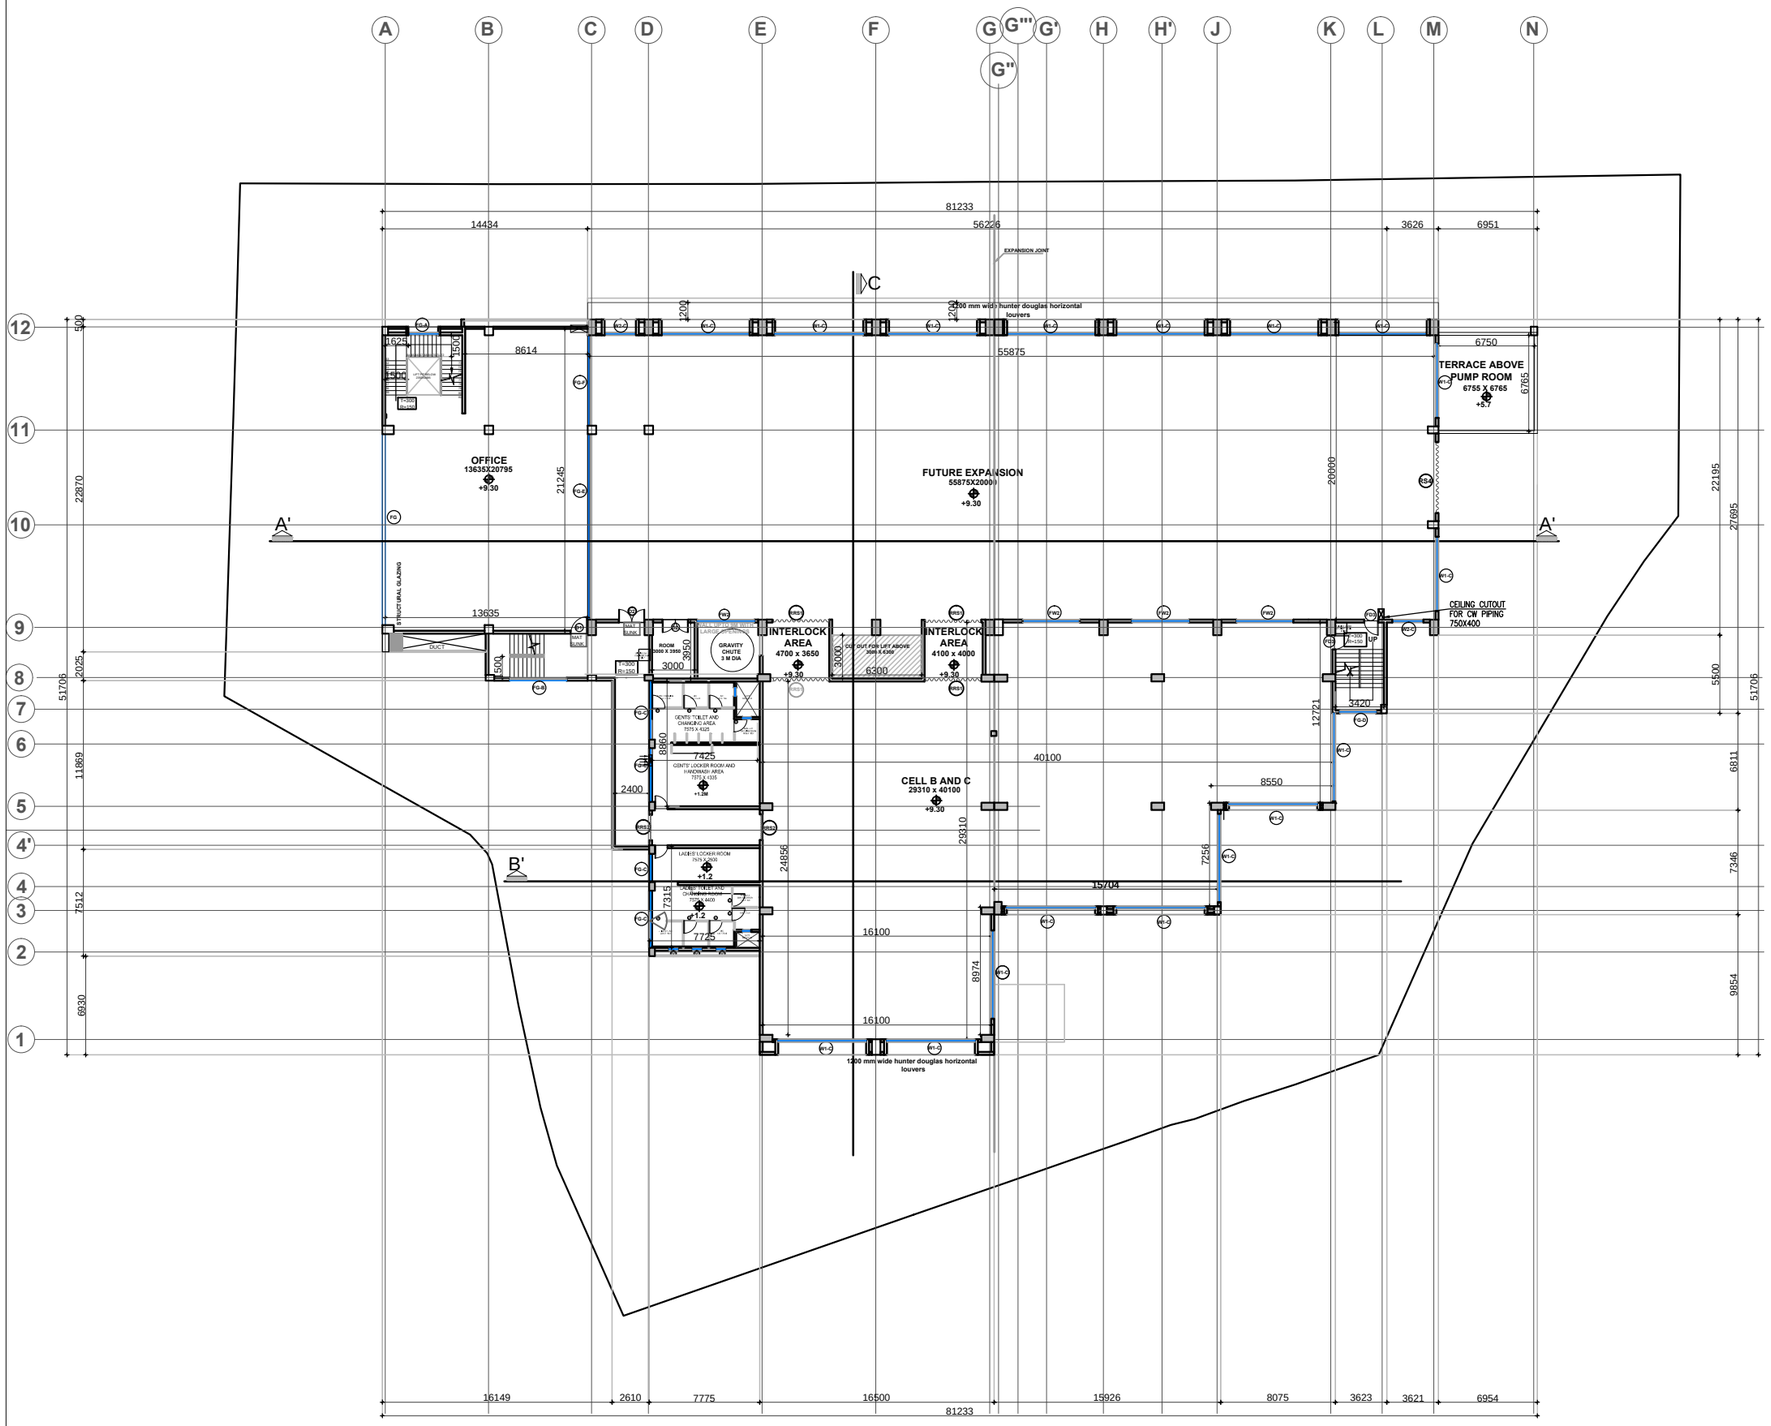

SECOND FLOOR PLAN
SCALE - 1:400

DOOR SCHEDULE

SR NO.	TYPE	SIZE(IN M)	NOS	DESCRIPTION
1	D1	1.2X2.4	5	1200 mm wide single leaf glass door openable
2	D1-A	1.2 X 2.4	3	metal door with vision panel
3	D1-B	1.2 x 2.4	1	Single leaf flush door
4	D2	1.8X2.4	10	Double leaf metal door with vision panel.
5	D3	1.8X2.4	1	Thick metal sliding door -acoustical and vibration proof.
6	D4	0.9X2.4	1	security cabin door
7	D5	1.2X2.4	2	Single leaf flush door - both side swing.
8	D6	0.9X2.4	4	Metal door 300 X 300 vision panel.
9	D7	0.9X2.4	15	Single leaf flushdoor.
10	D8	0.9X2.4	1	Access control door
11	D9	0.9 x 2.4	1	Wicket gate
12	FD1	3.0X2.4	1	Fire rated sliding door.
13	FD2	1.8X2.4	2	Double leaf fire rated with vision panel,metal.
14	FD3	1.0X2.4	8	Fire rated single leaf door with vision panel.
15	RS-1	5.0X7.0	2	Motorized rolling shutter.
16	RS-2	3.0X3.0	2	Motorized rolling shutter.
17	RS-3	3.0 X 3.0	1	Motorized rolling shutter with collapsible door on outer side.
18	RS-4	5.0X3.0	1	Motorized rolling shutter.
19	RRS-1	2.4X3.0	4	Rapid rolling shutter.
20	RRS-2	1.8X3.0	2	Rapid rolling shutter.
21	GATE	18M WIDE	1	Motorized Retractable gate

WINDOW SCHEDULE

SR.NO.	TYPE	SIZE(IN M)	NOS.	DESCRIPTION
1	W1-A	4.00X1.8	10	2 track aluminium window with fixed glass in between and louvers at bottom 600mm
2	W1-B	4.00X1.8	9	2 track aluminium window fire rated.
3	W1-C	6.20X2.25	8	Double glass unit (DGU)
	W1-C'	6.20X2.25	9	Sliding window
4	W2-A	1.65X1.8	9	2track aluminium window with louvers at bottom
5	W2-B	1.65X1.8	1	2track aluminium window sliding.
6	W2-C	2.20X2.25	2	Sliding window
7	W3	900 X 1500	2	Openable window
8	W4	4.0 X 600	1	Gravity louvers
9	FW-1	4.00X 1.8	1	Fixed firerated glass window.
10	FW-2	4.00X1.8	13	Fixed glass window.
11	FW-3	2.0 X 1.5	2	Fixed glass, aluminium frame security cabin)
12	FG	3.43X7.96	1	Structural glazing.
13	FG-A	2.10X3.30	3	Fixed glass.
14	FG-B	4.00 X14.05	1	Structural glazing.
15	FG-C	4.50 X length	6	Fixed glass.
16	FG-D	2.55X3.30	4	Fixed glass.
17	FG-E	13.03X2.30	2	D.G.U
18	FG-F	6.36X2.30	2	D.G.U
19	V	0.6X0.9	6	Louvers

P R O J E C T -

GREENFIELD MANUFACTURING BUILDING AT E7/A2, CHAKAN MIDC PHASE III, PUNE.

O W N E R -

ARAYMOND FASTENERS
INDIA PVT LTD

D R A W I N G -

TENDER DRAWING - SECOND FLOOR PLAN

SACHIN P. MUJUMDAR
REGD. ARCHITECT CA/90/13058

• DEVEN V. GHOTGE
REGD. ARCHITECT CA/90/12774

FOUNDER PARTNER
LATE SHRI.ABHAY B. SHARMA
LATE SHRI.VIJAY V. GHOTGE

DESIGNED BY: ARCHITECTS UNITED
111/9, 14th Lane Prabhat Road, Pune-411 004
Ph.25441426 E-MAIL:au@architectsunited.co.in

SCALE	DATE	DRAWN BY
AS SPECIFIED	23.03.2019	MEENAKSHI

REVISION

RVN. NO.	DATE	DRAWN BY

NORTH

job no.- 16_20_A10
drg no.- 3008
drg nm.- 16_20_A10_TD_AU_PB_007

NOTES
1) DO NOT SCALE THE DRAWING.
2) WRITTEN DIMENSIONS ARE TO BE FOLLOWED.
3) DISCREPANCY, IF ANY, PLEASE REFER IT TO THE ARCHITECT.
4) CONTRACTOR SHOULD CHECK AND VERIFY THE DRAWING.

PROJECT CONSULTANTS

P M C : JLL
Lvl 6, Amar Avinash Corporate Plaza,11 Bund Garden Rd,Pune 001
EMAIL -abhay.tiwari@ap.jll.com CONTACT -+91 8805181200

STRUCTURAL : -
KEDAR PHADNIS
203,Ganesh Apts,Off Karve Road, Behind Ashtekar Jewellers, Pune-411004
EMAIL - kedarphadnis@yahoo.com CONTACT -+91 9423012603


P L U M B I N G : - McLIN CONSULTANTS PVT. LTD.
Sirijaa 5, Sitabaug Colony, Vitthalwadi Road, Pune - 411 030.
EMAIL - mclinpl@gmail.com CONTACT - 020 - 2432 0010 / 2432 4859

FIRE PROTECTION : - EXPERT_TECH SYSTEMS
51/43, Navsahyadri Society,Karvenagar, Pune 411 052.
EMAIL - etsjdr@gmail.com CONTACT - +91 9371008098

H V A C : - R.S.KULKARNI HVACR CONSULTING ENGINEERS
512 + 513, Siddharth Tower,Sangam Press Road, Kothrud,Pune I 411029
EMAIL - rskulkarni@rskhvacr.com CONTACT - 020-41315512/13/14/15

E L E C T R I C A L : - VIDYUT SALLAGAR PVT. LTD.
Savitri, 113 Vinayak Society, Sahakarnagar, Pune - 411 009
EMAIL - vidyutsallagar@gmail.com CONTACT - : 020 24224534

L E E D : - GREEN DESIGN CONSULTANCY
112 / 8, Vasundhara Apartments, 14th lane, Prabhat Road, Pune - 411 004
EMAIL - greenprojects13@gmail.com CONTACT - : +91 9881371403

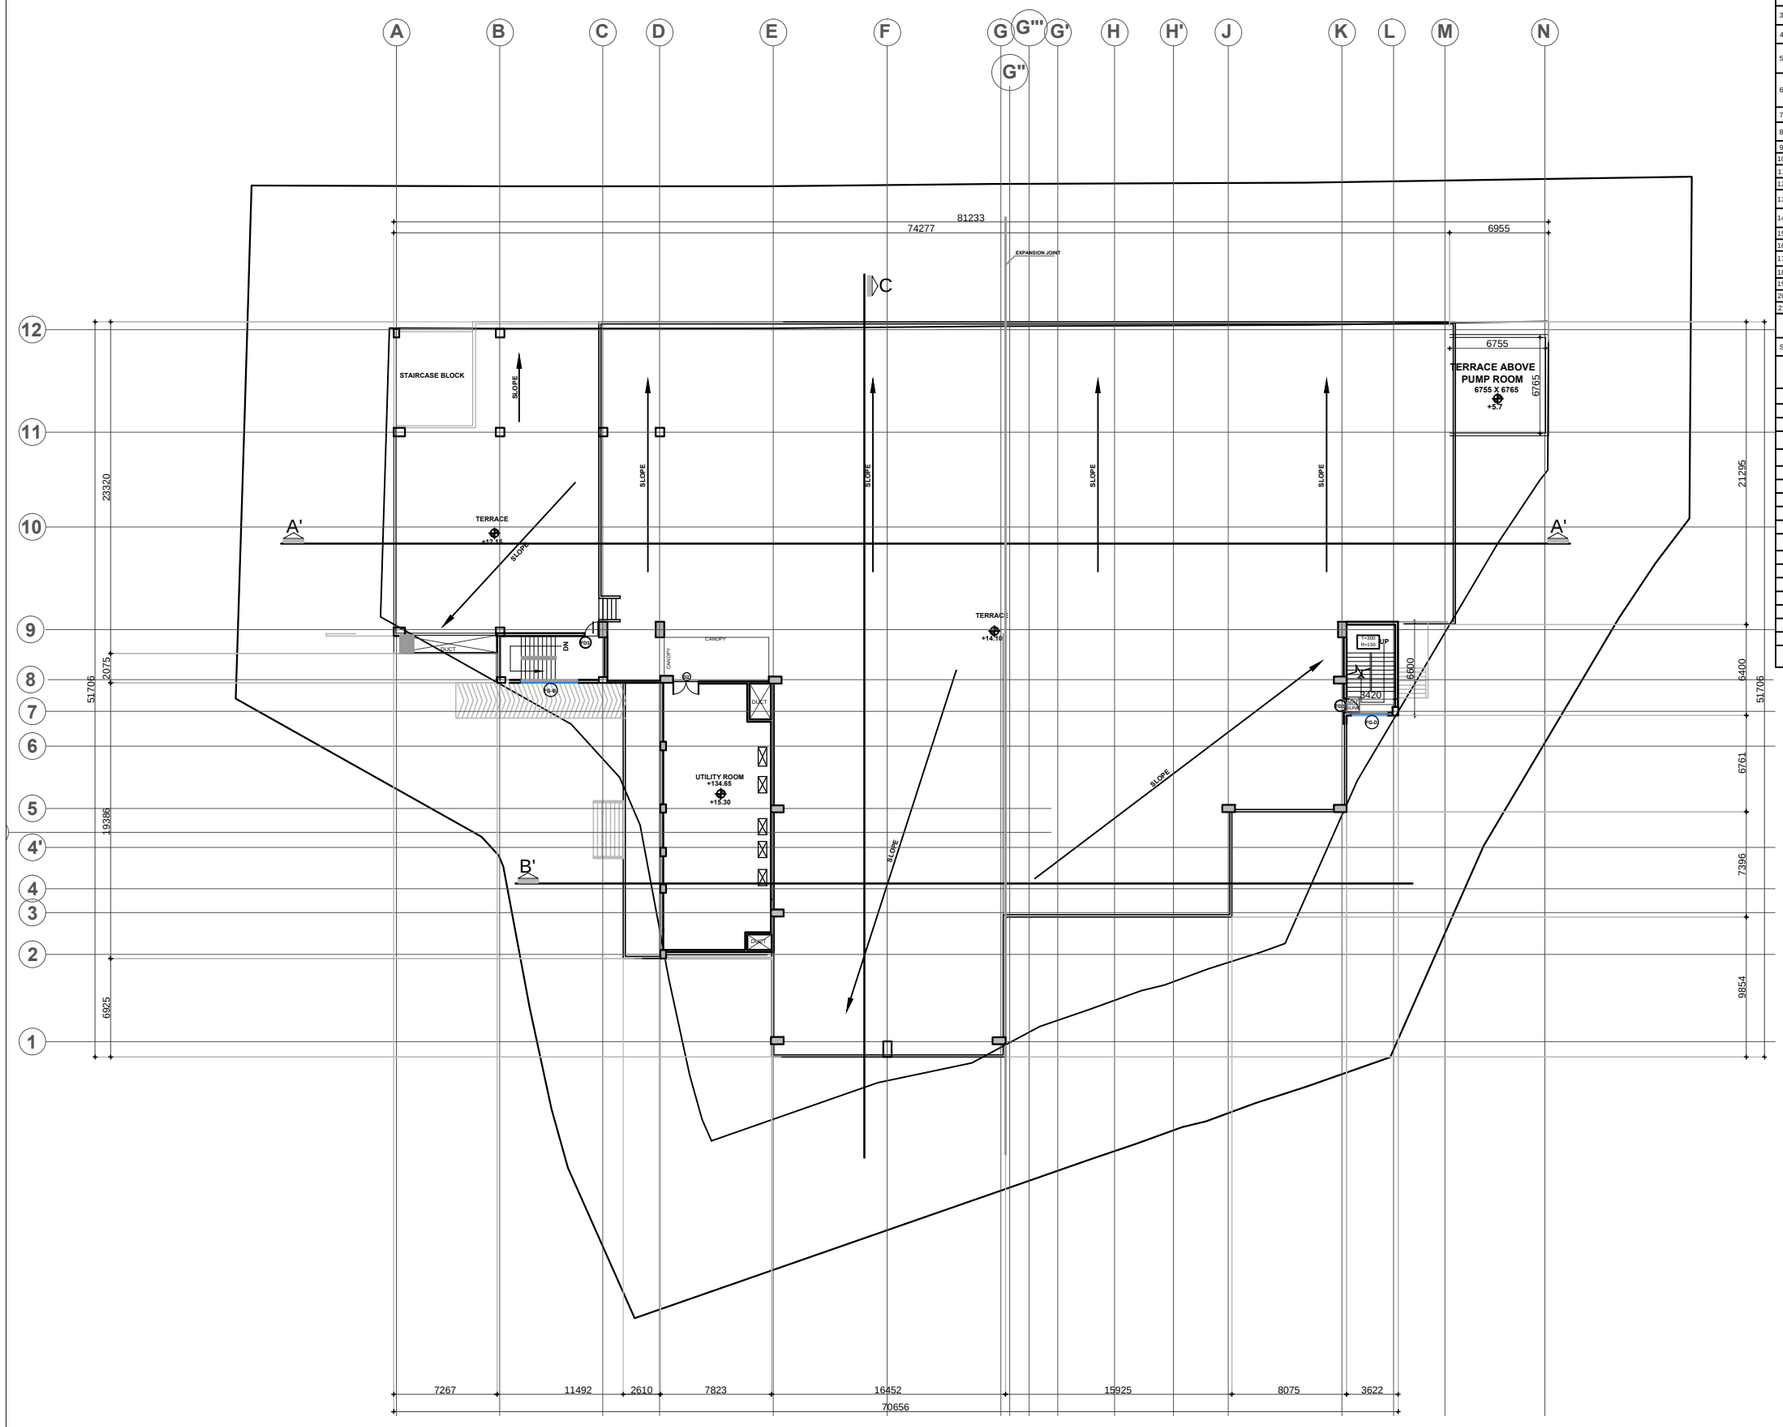

TERRACE FLOOR PLAN
SCALE - 1:400

DOOR SCHEDULE

SR NO	TYPE	SIZE(IN M)	NOS	DESCRIPTION
1	D1	1.2X2.4	5	1200 mm wide single leaf glass door openable
2	D1-A	1.2 X 2.4	3	metal door with vision panel
3	D1-B	1.2 x 2.4	1	Single leaf flush door
4	D2	1.8X2.4	10	Double leaf metal door with vision panel.
5	D3	1.8X2.4	1	Thick metal sliding door acoustical and vibration proof.
6	D4	0.9X2.4	1	security cabin door
7	D5	1.2X2.4	2	Single leaf flush door - both side swing.
8	D6	0.9X2.4	4	Metal door 300 X 300 vision panel.
9	D7	0.9X2.4	15	Single leaf flushdoor.
10	D8	0.9X2.4	1	Access control door
11	D9	0.9 x 2.4	1	Wicket gate
12	FD1	3.0X2.4	1	Fire rated sliding door.
13	FD2	1.8X2.4	2	Double leaf fire rated with vision panel,metal.
14	FD3	1.0X2.4	8	Fire rated single leaf door with vision panel.
15	RS-1	5.0X7.0	2	Motorized rolling shutter.
16	RS-2	3.0X3.0	2	Motorized rolling shutter.
17	RS-3	3.0 X 3.0	1	Motorized rolling shutter with collapsible door on outer side.
18	RS-4	5.0X3.0	1	Motorized rolling shutter.
19	RRS-1	2.4X3.0	4	Rapid rolling shutter.
20	RRS-2	1.8X3.0	2	Rapid rolling shutter.
21	GATE	18M WIDE	1	Motorized Retractable gate

WINDOW SCHEDULE

SR.NO.	TYPE	SIZE(IN M)	NOS.	DESCRIPTION
1	W1-A	4.00X1.8	10	2 track aluminium window with fixed glass in between and louvers at bottom 600mm.
2	W1-B	4.00X1.8	9	2 track aluminium window fire rated.
3	W1-C	6.20X2.25	8	Double glass unit (DGU)
	W1-C'	6.20X2.25	9	Sliding window
4	W2-A	1.65X1.8	9	2track aluminium window with louvers at bottom.
5	W2-B	1.65X1.8	1	2track aluminium window sliding.
6	W2-C	2.20X2.25	2	Sliding window
7	W3	900 X 1500	2	Openable window
8	W4	4.0 X 600	1	Gravity louvers
9	FW-1	4.00X 1.8	1	Fixed firerated glass window.
10	FW-2	4.00X1.8	13	Fixed glass window.
11	FW-3	2.0 X 1.5	2	Fixed glass, aluminium frame (security cabin)
12	FG	3.43X7.96	1	Structural glazing.
13	FG-A	2.10X3.30	3	Fixed glass.
14	FG-B	4.00 X14.05	1	Structural glazing.
15	FG-C	4.50 X length	6	Fixed glass.
16	FG-D	2.55X3.30	4	Fixed glass.
17	FG-E	13.03X2.30	2	D.G.U
18	FG-F	6.36X2.30	2	D.G.U
19	V	0.6X0.9	6	Louvers

P R O J E C T -

GREENFIELD MANUFACTURING BUILDING AT E7/A2, CHAKAN MIDC PHASE III, PUNE.

O W N E R -

ARAYMOND FASTENERS INDIA PVT LTD

D R A W I N G -

TENDER DRAWING - TERRACE FLOOR PLAN

SACHIN P. MUJUMDAR
REGD. ARCHITECT CA/90/13058
• DEVEN V. GHOTGE
REGD. ARCHITECT CA/90/12774
FOUNDER PARTNER
LATE SHRI.LABHAY B. SHARMA
LATE SHRI.VIJAY V. GHOTGE
DESIGNED BY: ARCHITECTS UNITED
111/9, 14th Lane Prabhat Road, Pune-411 004
Ph.25441426 E-MAIL:au@architectsunited.co.in

SCALE	DATE	DRAWN BY
AS SPECIFIED	23.03.2019	MEENAKSHI

REVISION

RVN. NO.	DATE	DRAWN BY

NORTH

job no.- 16_20_A10
drg no.- 3009
drg nm.- 16_20_A10_TD_AU_PB_TF_008

NOTES

1) DO NOT SCALE THE DRAWING.
2) WRITTEN DIMENSIONS ARE TO BE FOLLOWED.
3) DISCREPANCY, IF ANY, PLEASE REFER IT TO THE ARCHITECT.
4) CONTRACTOR SHOULD CHECK AND VERIFY THE DRAWING.

PROJECT CONSULTANTS

P M C : JLL
Lvl 6, Amar Avinash Corporate Plaza,11 Bund Garden Rd,Pune 001
EMAIL -abhay.tiwari@ap.jll.com CONTACT -+91 8805181200

STRUCTURAL : -
KEDAR PHADNIS
103,Ganesh Apts,Off Karve Road, Behind Ashtekar Jewellers, Pune-411004
EMAIL - kedarphadnis@yahoo.com CONTACT -+91 9423012603


P L U M B I N G : - McLIN CONSULTANTS PVT. LTD.
Girijad 5, Sitabaug Colony, Vitthalwadi Road, Pune - 411 030.
EMAIL - mclinpl@gmail.com CONTACT - 020 - 2432 0010 / 2432 4859

FIRE PROTECTION : - EXPERT_TECH SYSTEMS
51/43, Navsahyadri Society,Karvenagar, Pune 411 052.
EMAIL - etsjdr@gmail.com CONTACT - +91 9371008098


H V A C : - R.S KULKARNI HVACR CONSULTING ENGINEERS
512 + 513, Siddharth Tower,Sangam Press Road, Kothrud,Pune I 411029
EMAIL - rskulkarni@rskhvacr.com CONTACT - 020-41315512/13/14/15

E L E C T R I C A L : - VIDYUT SALLAGAR PVT. LTD.
Savitri, 113 Vinayak Society, Sahakarnagar, Pune - 411 009
EMAIL - vidyutsallagar@gmail.com CONTACT - : 020 24224534


L E E D : - GREEN DESIGN CONSULTANCY
112 / 8, Vasundhara Apartments, 14th lane, Prabhat Road, Pune - 411 004
EMAIL - greenprojects13@gmail.com CONTACT - : +91 9881371403

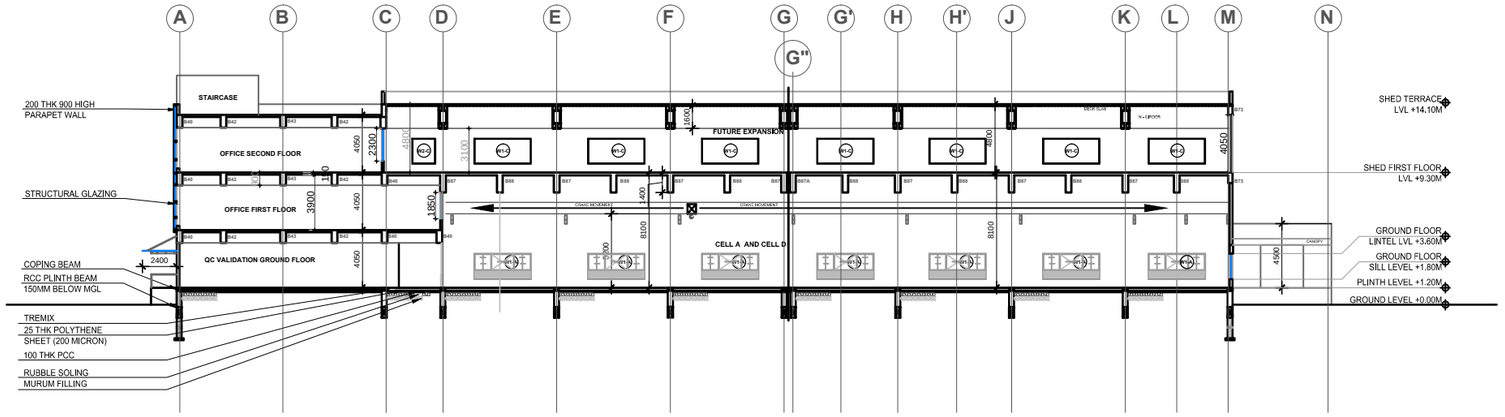

SECTION A-A'
SCALE - 1:400

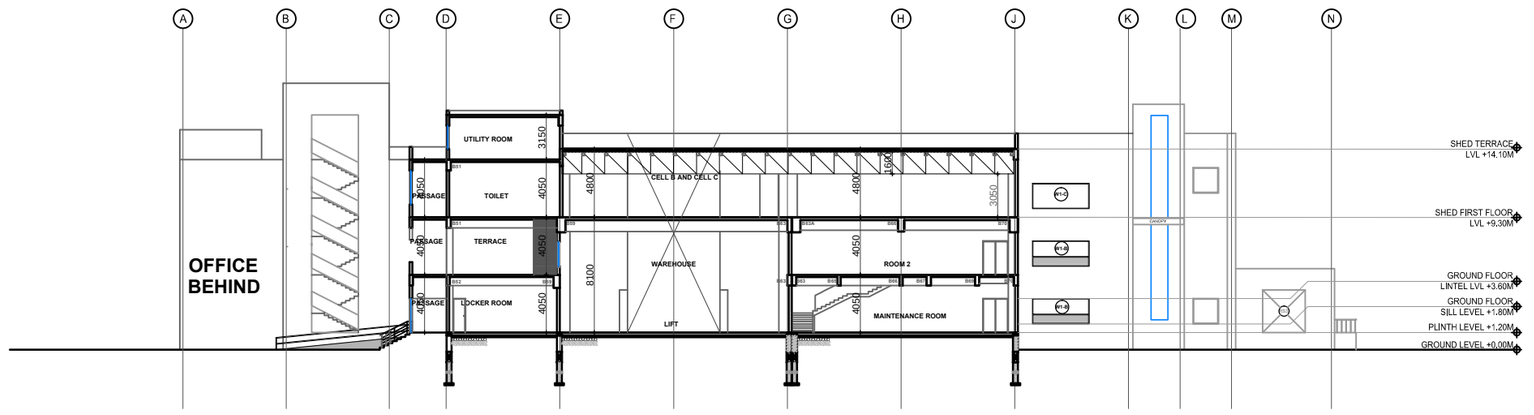

SECTION B-B
SCALE - 1:400

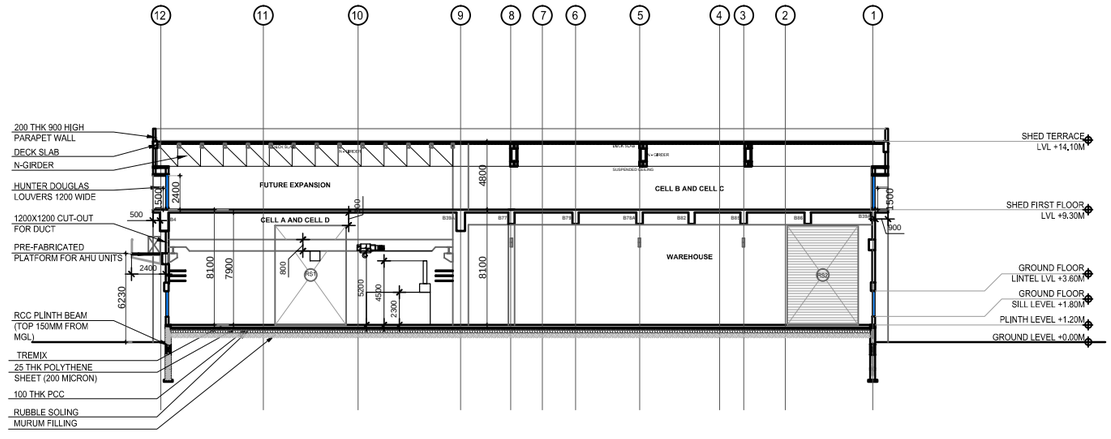

SECTION C-C
SCALE - 1:400

P R O J E C T -

GREENFIELD MANUFACTURING BUILDING
AT E7/A2, CHAKAN MIDC PHASE III, PUNE.

O W N E R -

ARAYMOND FASTENERS
INDIA PVT LTD

D R A W I N G -

TENDER DRAWING - SECTIONS

SACHIN P. MUJUMDAR
REGD. ARCHITECT CA/90/13058

• DEVEN V. GHOTGE
REGD. ARCHITECT CA/90/12774

FOUNDER PARTNER

LATE SHRI.ABHAY B. SHARMA

LATE SHRI.VIJAY V. GHOTGE

DESIGNED BY: ARCHITECTS UNITED
111/9, 14th Lane Prabhat Road, Pune-411 004
Ph.25441426 E-MAIL:au@architectsunited.co.in

SCALE	DATE	DRAWN BY
AS SPECIFIED	19.03.2019	MEENAKSHI

REVISION

RVN. NO.	DATE	DRAWN BY

NORTH

job no.-
16_20_A10
drg no.-
3010
drg nm.-
16_20_A10_TD_AU_PB_SEC_009

NOTES

1) DO NOT SCALE THE DRAWING.
2) WRITTEN DIMENSIONS ARE TO BE FOLLOWED.
3) DISCREPANCY, IF ANY, PLEASE REFER IT TO THE ARCHITECT.
4) CONTRACTOR SHOULD CHECK AND VERIFY THE DRAWING.

PROJECT CONSULTANTS

P M C :
J L L
Lvl 6, Amar Avinash Corporate Plaza,11 Bund Garden Rd,Pune 001
EMAIL -abhay.tiwari@ap.jll.com CONTACT -+91 8805181200

S T R U C T U R A L : -
KEDAR PHADNIS
103,Ganesh Apts,Off Karve Road, Behind Ashtekar Jewellers, Pune-411004
EMAIL - kedarphadnis@yahoo.com CONTACT -+91 9423012603


P L U M B I N G : -
McLIN CONSULTANTS PVT. LTD.
Girijaa 5, Sitabaug Colony, Vitthalwadi Road, Pune - 411 030.
EMAIL - mclinpl@gmail.com CONTACT -020 - 2432 0010 / 2432 4859

F I R E P R O T E C T I O N : -
EXPERT_TECH SYSTEMS
51/43, Navsahyadri Society,Karvenagar, Pune 411 052.
EMAIL - etsjdr@gmail.com CONTACT - +91 9371008098


H V A C : -
R.S.KULKARNI HVACR CONSULTING ENGINEERS
512 + 513, Siddharth Tower,Sangam Press Road, Kothrud,Pune I 411029
EMAIL - rskulkarni@rskhvacr.com CONTACT - 020-41315512/13/14/15

E L E C T R I C A L : -
VIDYUT SALLAGAR PVT. LTD.
Savitri, 113 Vinayak Society, Sahakarnagar, Pune - 411 009
EMAIL - vidyutsallagar@gmail.com CONTACT - : 020 24224534


L E E D : -
GREEN DESIGN CONSULTANCY
112 / 8, Vasundhara Apartments, 14th lane, Prabhat Road, Pune - 411 004
EMAIL - greenprojects13@gmail.com CONTACT - : +91 9881371403

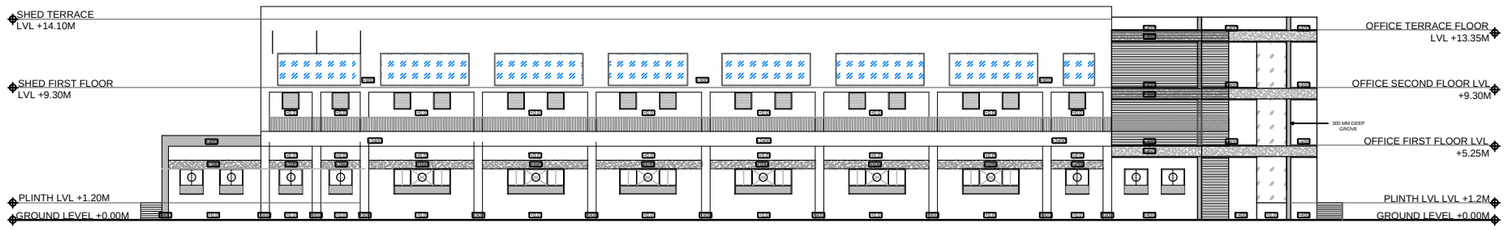


NORTH SIDE ELEVATION
SCALE - 1:400

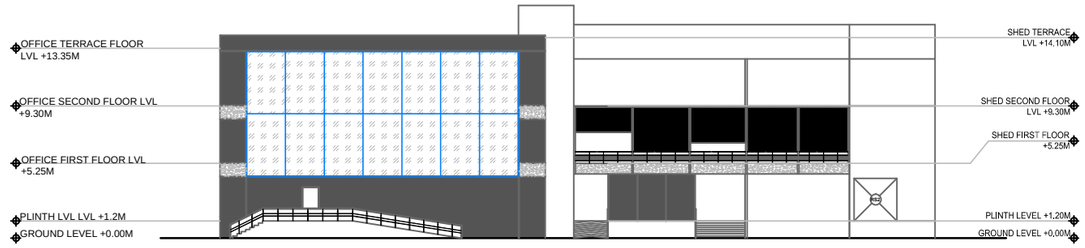

WEST SIDE ELEVATION
SCALE - 1:400

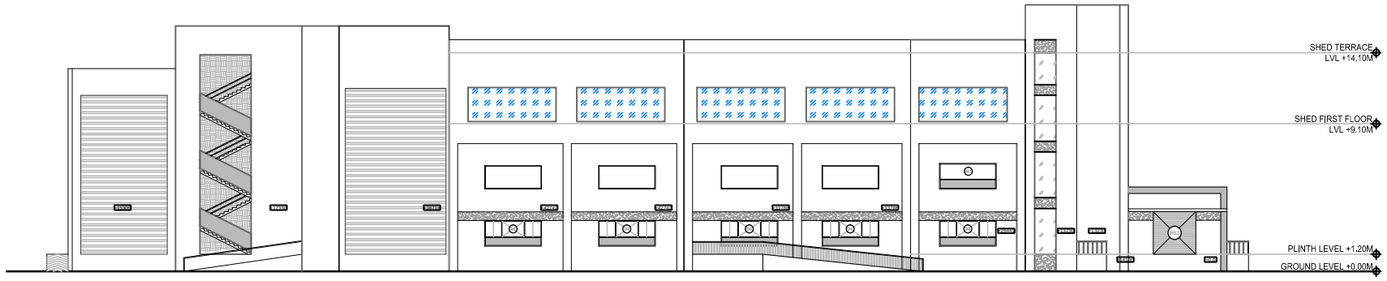

SOUTH SIDE ELEVATION
SCALE - 1:400

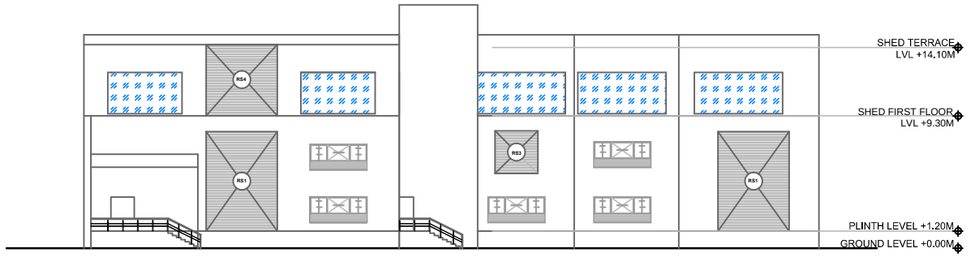

EAST SIDE ELEVATION
SCALE - 1:400

PROJECT -

GREENFIELD MANUFACTURING BUILDING
AT E7/A2, CHAKAN MIDC PHASE III, PUNE.

OWNER -

ARAYMOND FASTENERS
INDIA PVT LTD

DRAWING -

TENDER DRAWING - ELEVATIONS

SACHIN P. MUJUMDAR
REGD. ARCHITECT CA/90/13058

• DEVEN V. GHOTGE
REGD. ARCHITECT CA/90/12774

FOUNDER PARTNER
LATE SHRI.ABHAY B. SHARMA
LATE SHRI.VIJAY V. GHOTGE

DESIGNED BY: ARCHITECTS UNITED
111/9, 14th Lane Prabhat Road, Pune-411 004
Ph.25441426 E-MAIL:au@architectsunited.co.in

SCALE	DATE	DRAWN BY
AS SPECIFIED	23.03.2019	MEENAKSHI

REVISION

RVN. NO.	DATE	DRAWN BY

NORTH

job no.-
16_20_A10
drg no.-
3011
drg nm.-
16_20_A10_TD_AU_PB_ELE_010

NOTES

1) DO NOT SCALE THE DRAWING.
2) WRITTEN DIMENSIONS ARE TO BE FOLLOWED.
3) DISCREPANCY, IF ANY, PLEASE REFER IT TO THE ARCHITECT.
4) CONTRACTOR SHOULD CHECK AND VERIFY THE DRAWING.

PROJECT CONSULTANTS

P M C :
J L L
Lvl 6, Amar Avinash Corporate Plaza,11 Bund Garden Rd,Pune 001
EMAIL -abhay.tiwari@ap.jll.com CONTACT -+91 8805181200

STRUCTURAL : -
KEDAR PHADNIS
103,Ganesh Apts,Off Karve Road, Behind Ashtekar Jewellers, Pune-411004
EMAIL - kedarphadnis@yahoo.com CONTACT -+91 9423012603


P L U M B I N G : -
McLIN CONSULTANTS PVT. LTD.
4Sirijaõ 5, Sitabaug Colony, Vitthalwadi Road, Pune - 411 030.
EMAIL - mclinpl@gmail.com CONTACT - 020 - 2432 0010 / 2432 4859

FIRE PROTECTION : -
EXPERT_TECH SYSTEMS
51/43, Navsahyadri Society,Karvenagar, Pune 411 052.
EMAIL - etsjdr@gmail.com CONTACT - +91 9371008098

H V A C : -
R.S.KULKARNI HVACR CONSULTING ENGINEERS
512 + 513, Siddharth Tower,Sangam Press Road, Kothrud,Pune I 411029
EMAIL - rskulkarni@rskhvacr.com CONTACT - 020-41315512/13/14/15

E L E C T R I C A L : -
VIDYUT SALLAGAR PVT. LTD.
Savitri, 113 Vinayak Society, Sahakarnagar, Pune - 411 009
EMAIL - vidyutsallagar@gmail.com CONTACT - : 020 24224534

L E E D : -
GREEN DESIGN CONSULTANCY
112 / 8, Vasundhara Apartments, 14th lane, Prabhat Road, Pune - 411 004
EMAIL - greenprojects13@gmail.com CONTACT - : +91 9881371403

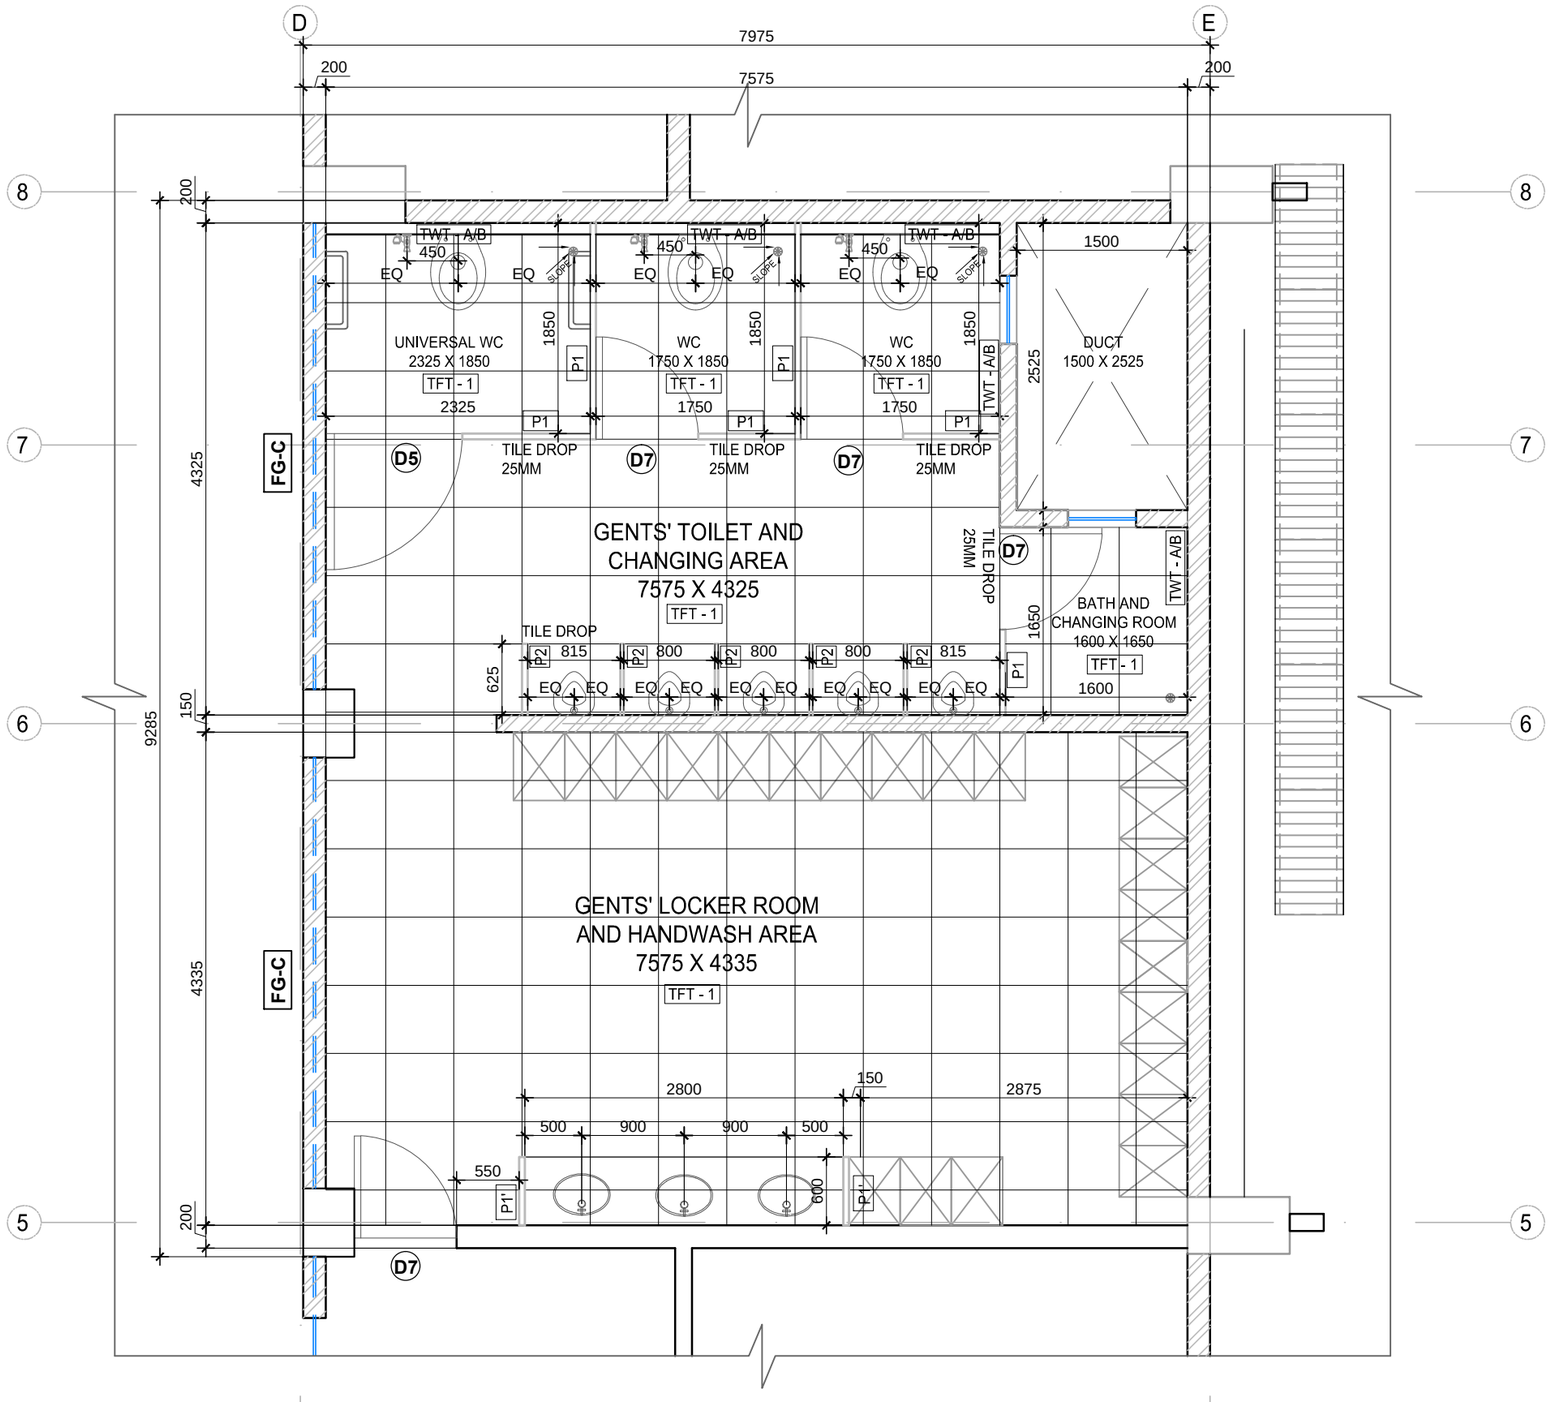

TOILET DETAIL A
SCALE - 1:50

P R O J E C T -

GREENFIELD MANUFACTURING BUILDING
AT E7/A2, CHAKAN MIDC PHASE III, PUNE.

O W N E R -

ARAYMOND FASTENERS
INDIA PVT LTD

D R A W I N G -

TENDER DRAWING - TOILET DETAIL A

SACHIN P MUJUMDAR
REGD. ARCHITECT CA/90/13058

• DEVEN V. GHOTGE
REGD. ARCHITECT CA/90/12774

FOUNDER PARTNER
LATE SHRI.ABHAY B. SHARMA
LATE SHRI.VIJAY V. GHOTGE

DESIGNED BY: ARCHITECTS UNITED
111/9, 14th Lane Prabhat Road, Pune-411 004
Ph.25441426 E-MAIL:au@architectsunited.co.in

SCALE	DATE	DRAWN BY
AS SPECIFIED	23.03.2019	POORVA

REVISION

RVN. NO.	DATE	DRAWN BY

NORTH

job no.-
16_20_A10
drg no.-
3025
drg nm.-
16_20_A10_TD_AU_PB_TDA_017

NOTES
1) DO NOT SCALE THE DRAWING.
2) WRITTEN DIMENSIONS ARE TO BE FOLLOWED.
3) DISCREPANCY, IF ANY, PLEASE REFER IT TO THE ARCHITECT.
4) CONTRACTOR SHOULD CHECK AND VERIFY THE DRAWING.

LEGEND
P1 - MODULAR PARTITION 2400MM HIGH FROM FFL
P1' - MODULAR PARTITION 1500MM HIGH FROM FFL
P2 - STANDARD DIVISION PLATE FOR URINALS
TFT-1 - TOILET FLOORING TILES - 600X600 ANTI SKID VITRIFIED TILES
TWT-A/B - TOILET WALL TILES - 300X450 COLOURED GLAZED DADO (LIGHT AND DARK USED IN COMBINATION)
NOTE - TOILET SLOPE TOWARDS FLOOR TRAP 1:200

P R O J E C T C O N S U L T A N T S

P M C :
J L L
Lvl 6, Amar Avinash Corporate Plaza,11 Bund Garden Rd,Pune 001
EMAIL -abhay.tiwari@ap.jll.com CONTACT - +91 8805181200

S T R U C T U R A L : -
KEDAR PHADNIS
103,Ganesh Apts,Off Karve Road, Behind Ashtekar Jewellers, Pune-411004
EMAIL - kedarphadnis@yahoo.com CONTACT -+91 9423012603


P L U M B I N G : -
McLIN CONSULTANTS PVT. LTD.
Girijaö 5, Sitabaug Colony, Vitthalwadi Road, Pune - 411 030.
EMAIL - mclinpl@gmail.com CONTACT - 020 - 2432 0010 / 2432 4859

F I R E P R O T E C T I O N : -
EXPERT_TECH SYSTEMS
51/43, Navsahyadri Society,Karvenagar, Pune 411 052.
EMAIL - etsjdr@gmail.com CONTACT - +91 9371008098

H V A C : -
R.S.KULKARNI HVACR CONSULTING ENGINEERS
512 + 513, Siddharth Tower,Sangam Press Road, Kothrud,Pune I 411029
EMAIL - rskulkarni@rskhvacr.com CONTACT - 020-41315512/13/14/15

E L E C T R I C A L : -
VIDYUT SALLAGAR PVT. LTD.
Savitri, 113 Vinayak Society, Sahakarnagar, Pune - 411 009
EMAIL - vidyutsallagar@gmail.com CONTACT - : 020 24224534

L E E D : -
GREEN DESIGN CONSULTANCY
112 / 8, Vasundhara Apartments, 14th lane, Prabhat Road, Pune - 411 004
EMAIL - greenprojects13@gmail.com CONTACT - : +91 9881371403

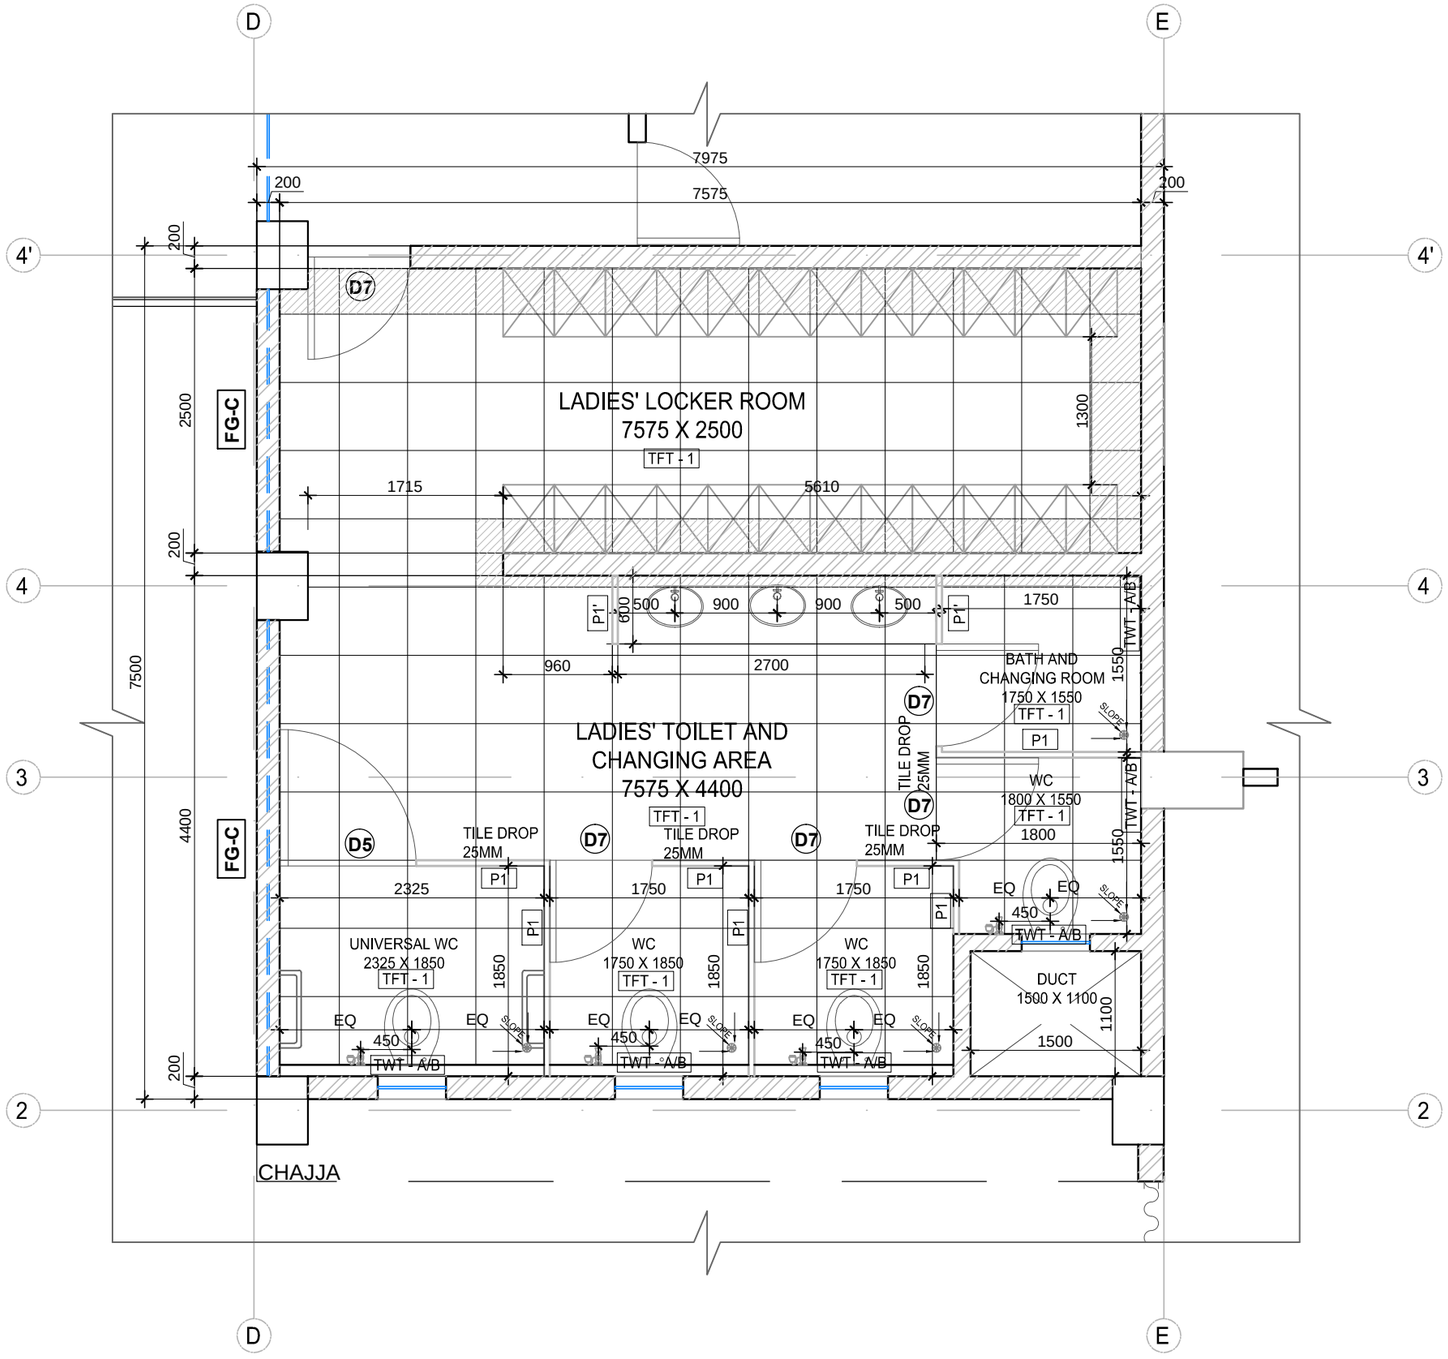

TOILET DETAIL B
SCALE - 1:50

P R O J E C T -

GREENFIELD MANUFACTURING BUILDING
AT E7/A2, CHAKAN MIDC PHASE III, PUNE.

O W N E R -

ARAYMOND FASTENERS
INDIA PVT LTD

D R A W I N G -

TENDER DRAWING - TOILET DETAIL B

SACHIN P. MUJUMDAR
REGD. ARCHITECT CA/90/13058

• DEVEN V. GHOTGE
REGD. ARCHITECT CA/90/12774

FOUNDER PARTNER
LATE SHRI.ABHAY B. SHARMA
LATE SHRI.VIJAY V. GHOTGE

DESIGNED BY: ARCHITECTS UNITED
111/9, 14th Lane Prabhat Road, Pune-411 004
Ph.25441426 E-MAIL:au@architectsunited.co.in

SCALE	DATE	DRAWN BY
AS SPECIFIED	23.03.2019	POORVA

REVISION

RVN. NO.	DATE	DRAWN BY

NORTH

job no.-
16_20_A10
drg no.-
3025
drg nm.-
16_20_A10_TD_AU_PB_TDB_018

NOTES

1) DO NOT SCALE THE DRAWING.
2) WRITTEN DIMENSIONS ARE TO BE FOLLOWED.
3) DISCREPANCY, IF ANY, PLEASE REFER IT TO THE ARCHITECT.
4) CONTRACTOR SHOULD CHECK AND VERIFY THE DRAWING.

PROJECT CONSULTANTS

P M C : -
J L L
Lvl 6, Amar Avinash Corporate Plaza,11 Bund Garden Rd,Pune 001
EMAIL - abhay.tiwari@ap.jll.com CONTACT - +91 8805181200

S T R U C T U R A L : -
KEDAR PHADNIS
103,Ganesh Apts,Off Karve Road, Behind Ashtekar Jewellers, Pune-411004
EMAIL - kedarphadnis@yahoo.com CONTACT - +91 9423012603

P L U M B I N G : -
McLIN CONSULTANTS PVT. LTD.
Girija5, Sitabaug Colony, Vitthalwadi Road, Pune - 411 030.
EMAIL - mclinpl@gmail.com CONTACT - 020 - 2432 0010 / 2432 4859

F I R E P R O T E C T I O N : -
EXPERT_TECH SYSTEMS
51/43, Navsahyadri Society,Karvenagar, Pune 411 052.
EMAIL - etsjdr@gmail.com CONTACT - +91 9371008098

H V A C : -
R.S.KULKARNI HVACR CONSULTING ENGINEERS
512 + 513, Siddharth Tower,Sangam Press Road, Kothrud,Pune I 411029
EMAIL - rskulkarni@rskhvacr.com CONTACT - 020-41315512/13/14/15

E L E C T R I C A L : -
VIDYUT SALLAGAR PVT. LTD.
Savitri, 113 Vinayak Society, Sahakarnagar, Pune - 411 009
EMAIL - vidyutsallagar@gmail.com CONTACT - : 020 24224534

L E E D : -
GREEN DESIGN CONSULTANCY
112 / 8, Vasundhara Apartments, 14th lane, Prabhat Road, Pune - 411 004
EMAIL - greenprojects13@gmail.com CONTACT - : +91 9881371403