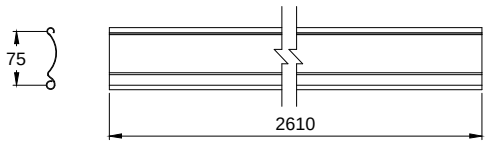

Curved slat

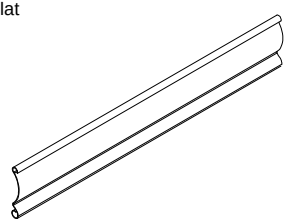

Slat profile- curved type.
Material- GI
Thickness - 1mm
Length of slats - 2610mm
Total no of slat - 49

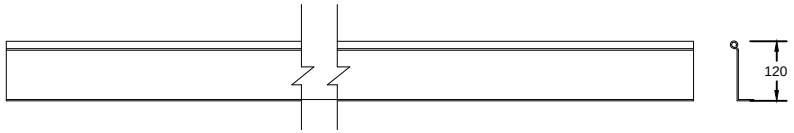

Material- MS
Thickness - 2.5mm
Length of bottom profile - 2610mm
Quantity- 1 Nos.

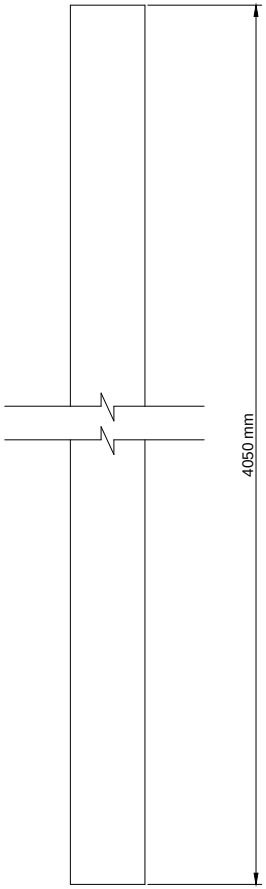

Material- MS
Thickness - 2.5mm
Length of guide - 4050mm
Quantity- 2 Nos.

DIMENSION :

CLEAR WIDTH	CLEAR HEIGHT	QUANTITY
2500mm	4000mm	03

MATERIAL : GI

THICKNESS : 0.9mm

NIHVA TECHNOLOGIES PVT. LTD.

NIHVA TECHNOLOGY PVT. LTD. PUNE
Email:- info@nihva.com
Website:- www.nihva.com

TITLE:

SLAT, GUIDE & BOTTOM PROFILE

CLIENT'S APPROVAL :

CLIENT -

PROJECT -

SITE LOCATION -

DWG. NO. : NIHVA/16-17/VDR/0038

SCALE: NTS	WT:	SHEET:1 OF 1

DRAWN BY: SURAJ	DATE: 15-05-2017
CHECK : SAGAR P.	DATE: 15-05-2017

If any queries contact : projects@nihva.com

NOTE: ALL DIMENSION ARE IN mm

THIS DRAWING & DESIGNING IS THE PROPERTY OF NIHVA TECHNOLOGIES. NOT BE SOLD OR COPY TO ANY OTHER CONCERN.