

TOP VIEW

INSIDE

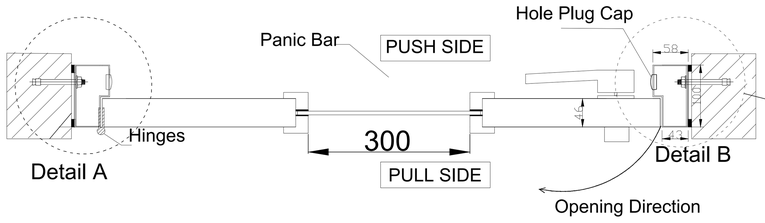



OUT SIDE

SECTION 'X'-'X'

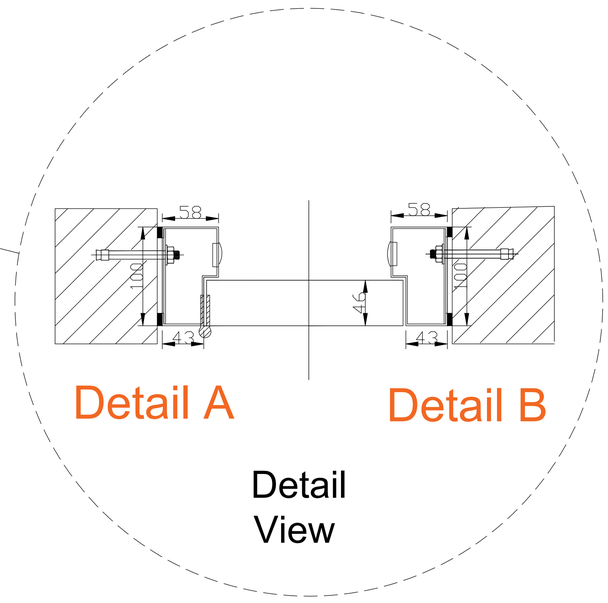

SIDE VIEW

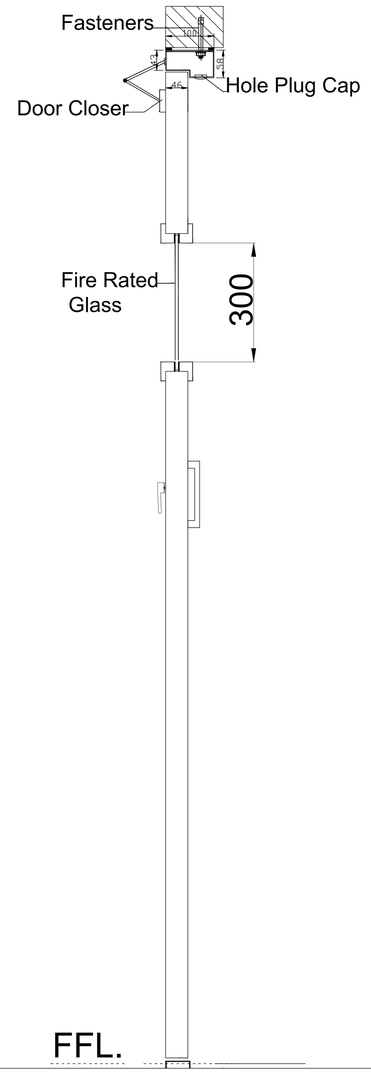

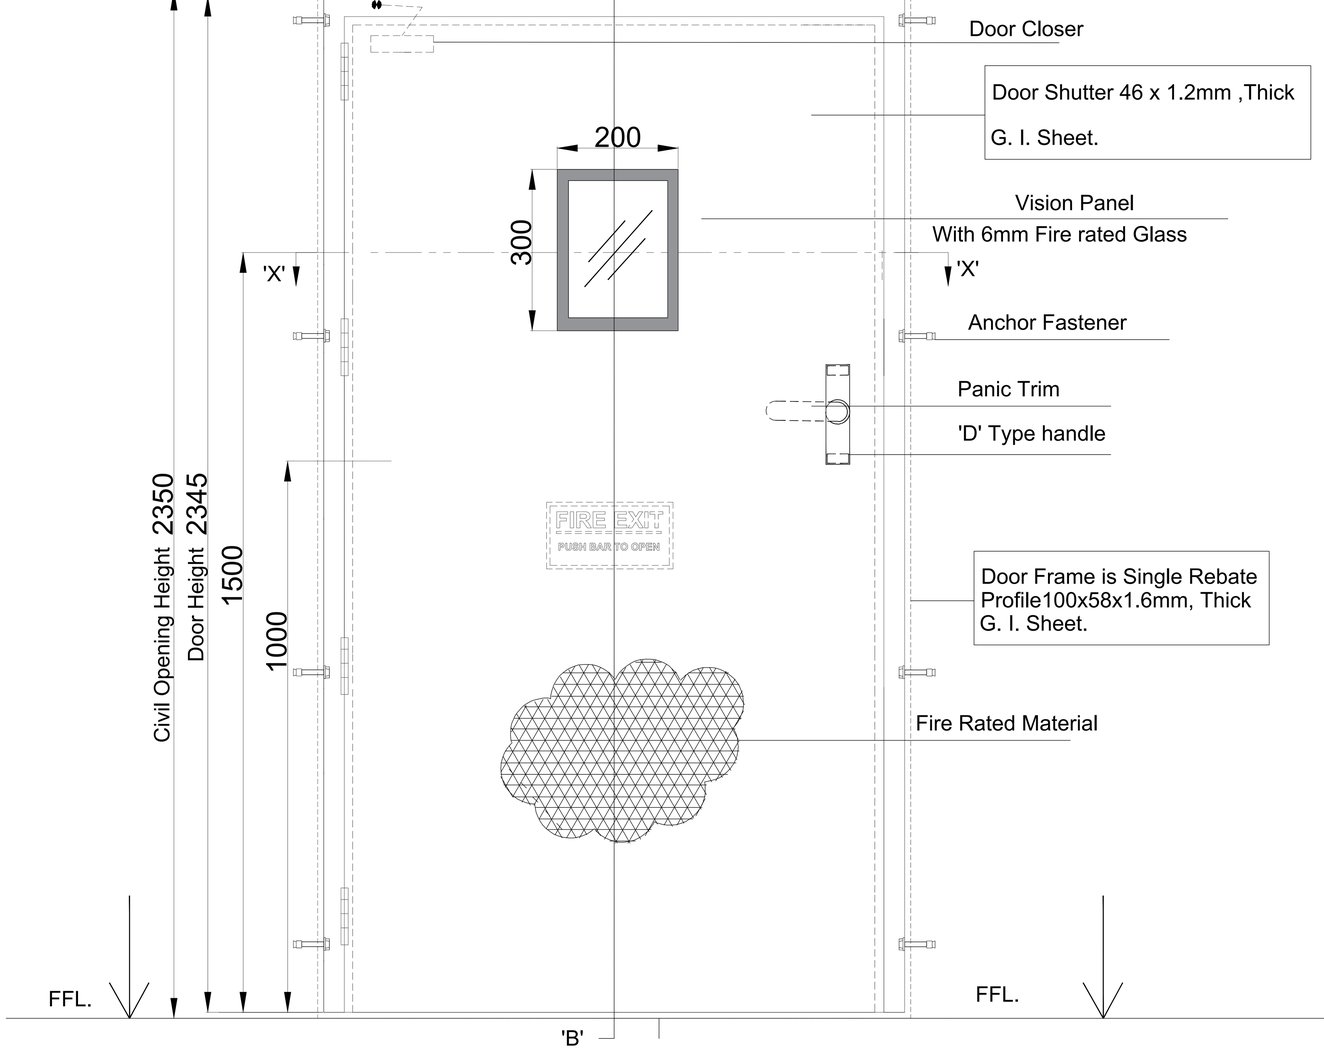

ELEVATION

SECTION B-B

FRONT VIEW

SIZE:

TECHNICAL SPECIFICATION :

Sr.	DESCRIPTION & DETAILS
01	Door frame - 100X58 mm x1.6mm thick G.I. Sheet
02	Door Shutter - 46 mm x1.2mm thick G.I. Sheet
03	SS Ball Bearing Hinges 4"x3"x3mm
04	'D' Type handle
05	External Panic Trim
06	Anchor Fasteners (M10x100mm Dia)
07	Heavy Duty Door Closer (TS 1000)
08	Vision Window With 6mm Fire Rated Glass
09	Fire Rating - 120 Minutes
10	RAL Code - 7044

Sr.	Clear Width	Clear Height	Qty
01	1070	2350	01

This Drawing & Design is the property of NIHVA TECHNOLOGIES. Not to be sold or copied to any other concern.

TITLE :- FIRE DOOR			NIHVA TECHNOLOGIES PVT. LTD. PUNE Tel : 020 66304033 Email : info@nihva.com Website : www.nihva.com	
NAME	DATE	SIGN		
S.J	21/09/2024		CLIENT -	
B.B	21/09/2024		LOCATION - PUNE	
V.T	21/09/2024		PRODUCT - FIRE DOOR	QTY-01 Nos
If any queries contact : design2@nihva.com			DWG NO - NIHVA/24-25/00XX	REV- 0
All dimensions are in MM			SCALE : NTS	SHEET : 01 OF 01