
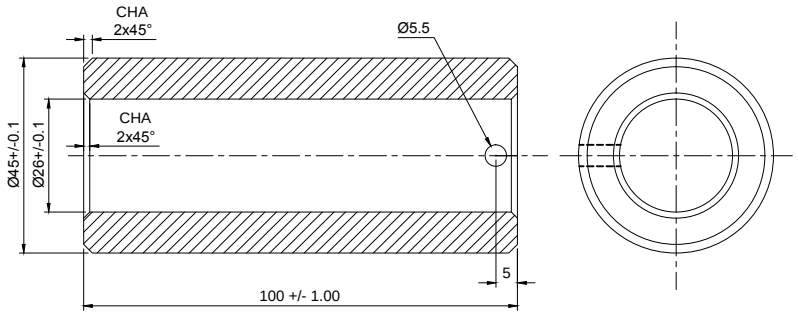


NOTE:~ MTL : MS

1. BUSH Ø45 X 103L = 2 NOS
2. M5 X 25L = 2 NOS

NOTE : ~ WELD AT BOTH ENDS OF LIP

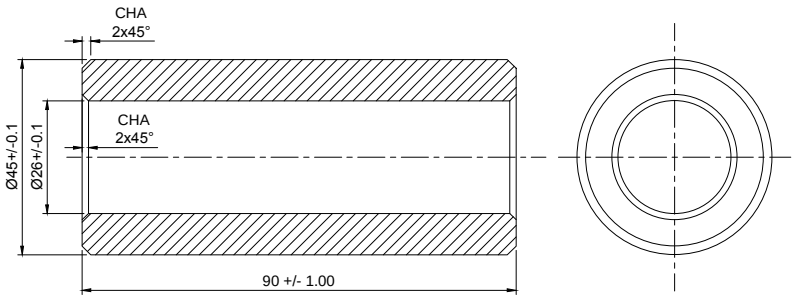


NOTE:~ MTL : MS

BUSH Ø45 X 93L = 1 NO

NOTE : ~ WELD AT CENTER OF LIP

NOTE : ~ PLEASE MAINTAIN 5 MM GAP BETWEEN TWO LIP BUSHES.

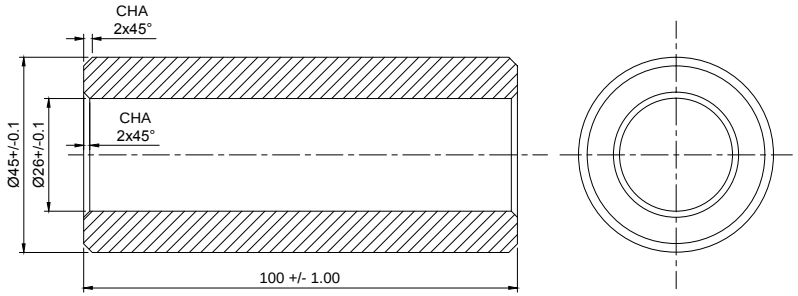

NOTE:~ MTL : MS

BUSH Ø45 X 103L = 18 NOS

This drawing & design is the property of NIHVA TECHNOLOGIES. Not to be sold or copied to any other concern.

TITLE

LIP MOUNTING BUSH

	NAME	SIGN	DATE
DRAWN	P.A		
CHECK	SHEKHAR		
APPRD.	SHEKHAR		

NIHVA TECHNOLOGIES PVT. LTD.

NIHVA TECHNOLOGIES PVT. LTD. PUNE
Tel : 020 66304033
Email:- info@nihva.com
Website:- www.nihva.com

CLIENT -

PROJECT - DLBJ1001

SITE LOCATION -

If any queries contact : design@nihva.com

DWG. NO. : NIHVA/17-18/ REV- 0

ALL DIMENSION ARE IN mm

SCALE: NTS WT: SHEET: 01 OF 01