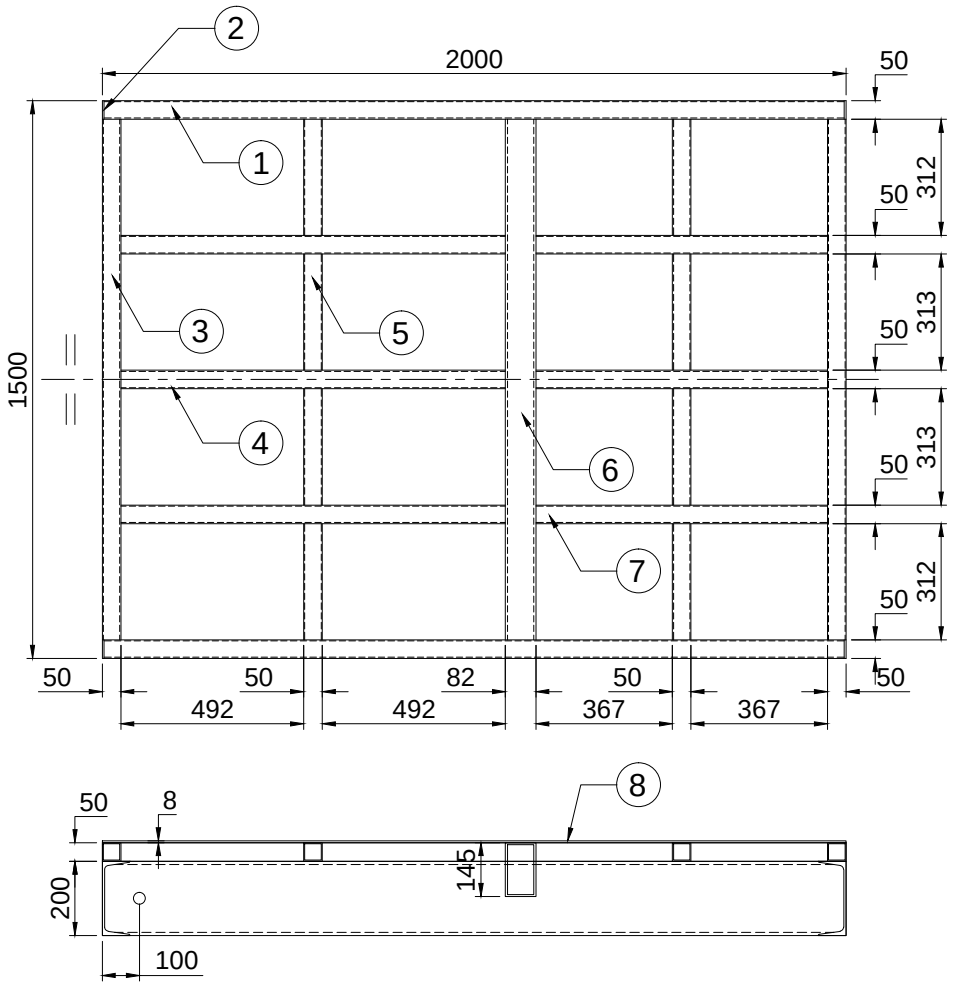

SR NO	PART NAME	SPECIFICATION	QTY
1	SQ.TUBE	50 X 50 X 3THK X1990L	2 NOS
2	FLAT	50 X 5 X 50L	2 NOS
3	SQ.TUBE	50 X 50 X 3THK X1400L	2 NOS
4	SQ.TUBE	50 X 50 X 3THK X1034L	3 NOS
5	SQ.TUBE	50 X 50 X 3THK X312L	8 NOS
6	RE.TUBE	145 X 82 X 5.4THK X 1488L	1 NO
7	SQ.TUBE	50 X 50 X 3THK X 784L	3 NOS
8	CHEQ. SHEET	1500 X 2000 X 8 THK	1 NO

This drawing & design is the property of NIHVA TECHNOLOGIES. Not to be sold or copied to any other concern.

TITLE : -

TOP STIFFENING FRAME

NIHVA TECHNOLOGIES PVT. LTD. PUNE
Tel : 020 66304033
Email:- info@nihva.com
Website:- www.nihva.com

	SIGN	DATE
DRAWN	P.A	10.01.19
CHECK	R.D	10.01.19
REV.		
APPROVAL		

If any queries contact : projects@nihva.com

ALL DIMENSION ARE IN mm

CLIENT -

PROJECT -

SITE -

DWG. NO. : NIHVA/18-19//MFG/NSCL327/03

SCALE: NTS | WT: | SHEET: 01 OF 01