

THIS PRINT IS THE PROPERTY OF NIHVA IT IS TO BE USED ONLY FOR THE PURPOSE FOR WHICH IT WAS LENT AND MUST NOT BE USED IN ANY WAY DERTIMENTAL TO THE INTEREST OF THIS COMPANY AND IS SUBJECT TO RETURN ON DEMAND.

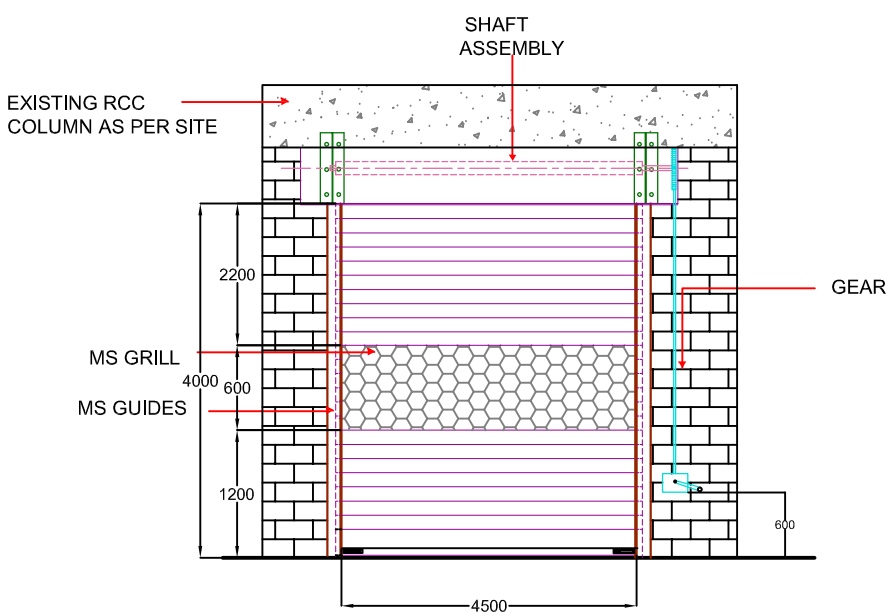


INSIDE ELEVATION


Clear Opening size:-
(W)4.5 mx(H)4.0m

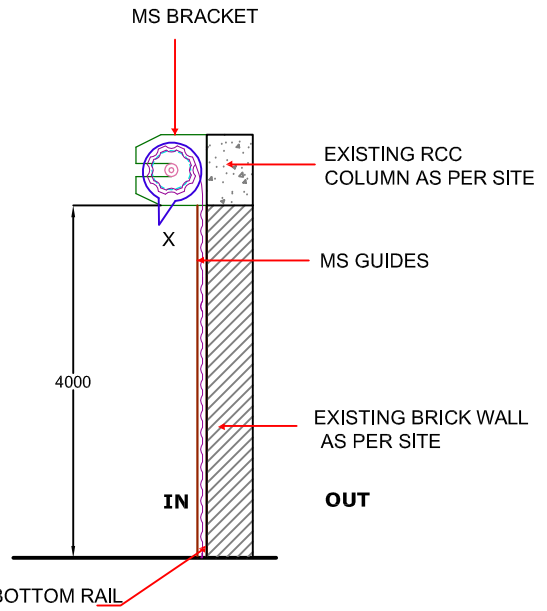


SIDE VIEW

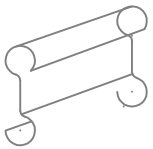


Box/Straight Type Slat Profile

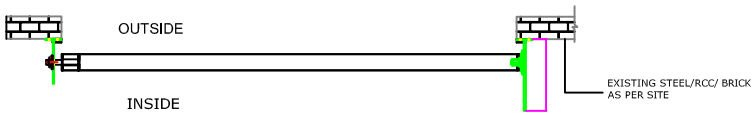

PLAN

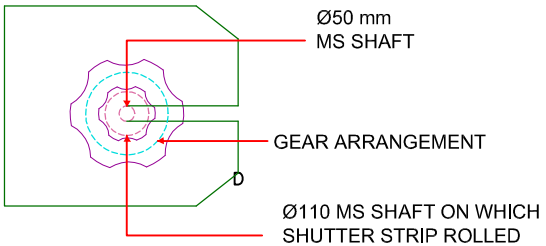

Bracket

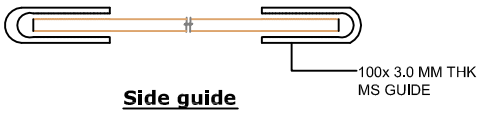

Side guide

Location :- Cafeteria
Size :- 4.5m(W) X 4.0M (H)
Qty :- 02 nos
Type :- GRS1- (Partyl grilled)

TITLE: Manual Gear Operated Rolling Shutter	DO NOT SCALE DRAWING		
		SIGN	DATE
CLIENTS APPROVEL:-	DRAWN	Anil	
	CHECK		
	ENG		
	APPRD.		
UNLESS & OTHERWISE SPECIFIED DIMENSION ARE IN M.M.	PROD		
	MFG		
	Ref. No.		

NIHVA TECHNOLOGIES PVT. LTD.
NIHVA TECHNOLOGIES PVT. LTD. Pune:-411044
Tel :- 020 66304033
Email :- info@nihva.com

CLIENT: Shapoorji Palonji Co. Ltd
PROJECT / SITE: GE,CHAKAN
PRODUCT NAME:
DWG. NO.: NVA/SP/04R
REV.: 0
SCALE: NTS WT: SHEET: 1 OF 1