


DRAWING


REV DESCRIPTION	DATE	REV NO
	14-10-2026	REV 00
1.		

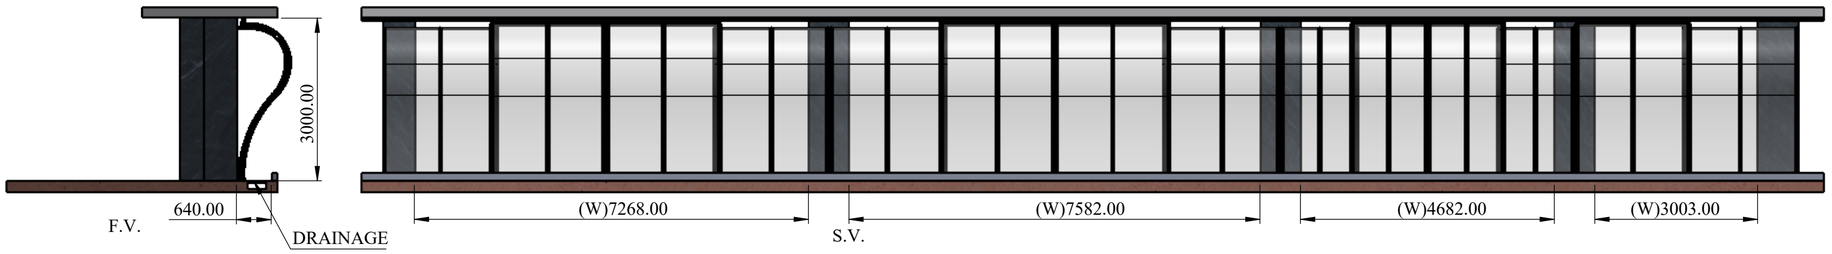

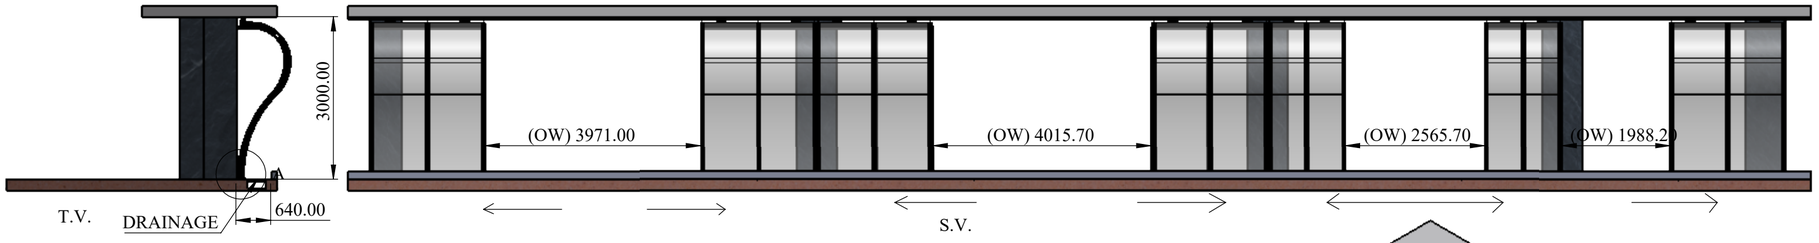


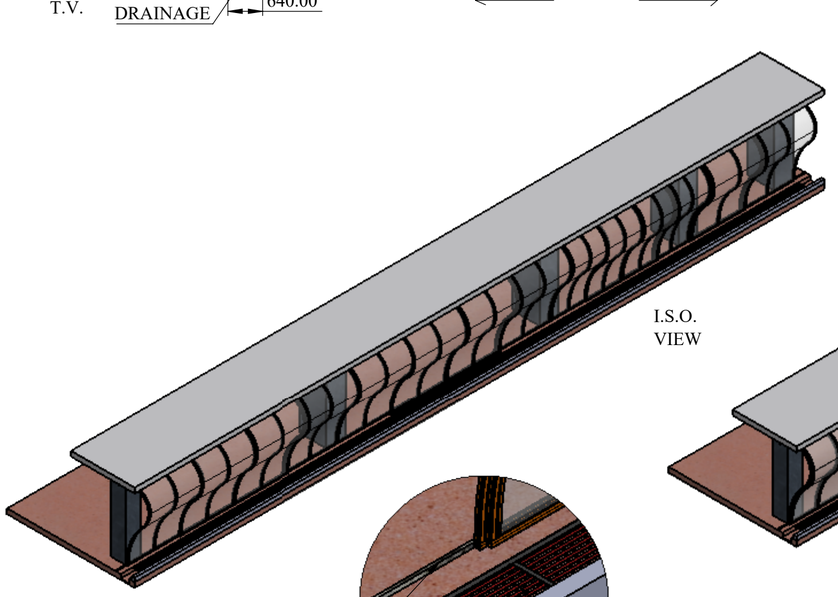


I.S.O.
VIEW

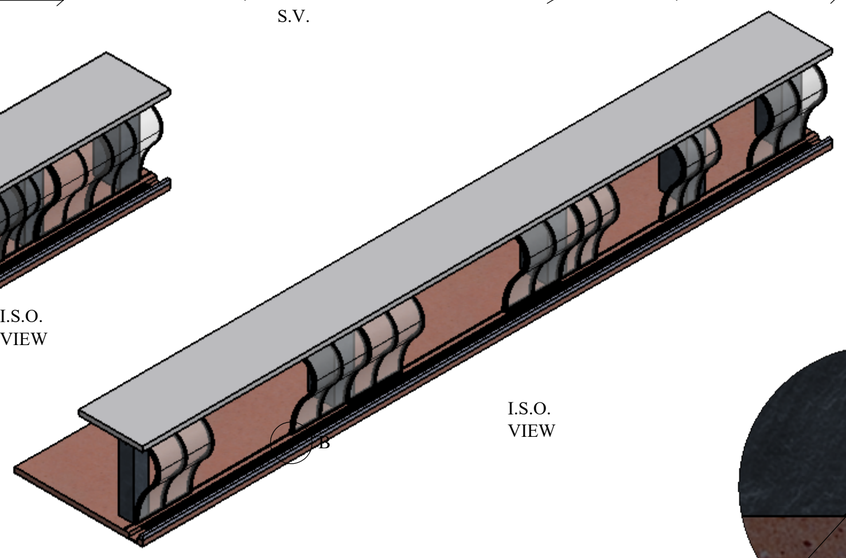

I.S.O.
VIEW

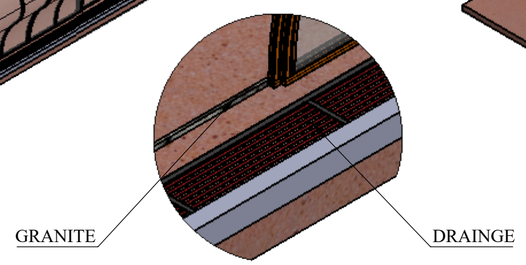

DETAIL B
SCALE 1 : 20

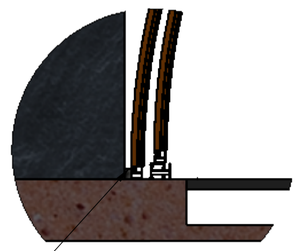

DETAIL A
SCALE 1 : 14

NOTE :

GA DRAWING
THIS DRAWING IS ONLY FOR CLIENT APPOVAL
BASE STRCTURE IN CLIENT SCOPE

SPECIAL INSTRUCTION'S :

This drawing & design is the property of NIHVA TECHONOLOGIES PVT. LTD. Not to be sold or copied to any other concern

TITLE - ROOF AUTOMATION

DWG NO - NTPL-

NIHVA TECHNOLOGIES PVT.LTD.PUNE
Website - www.nihva.com


	NAME	SIGNATURE	DATE
DRAWN	V.W.		14-10-2026
CHK'D	S.P.		15-10-2026
APPV'D	V.T.		15-10-2026


PRODUCT - MANUAL BALCONY ENCLOSURE
CLIENT NAME - 24k.
SITE LOCATION - MUMBAI FORT.
MATRIAL -
QTY - 1
SCALE :
SHEET 1 OF 2


If any queries contact - info@nihva.com
ALL DIMENSION ARE IN mm
A2
PROJECTION METHOD:

DRAWING

REV DESCRIPTION	DATE	REV NO
	14-10-2026	REV 00
1.		

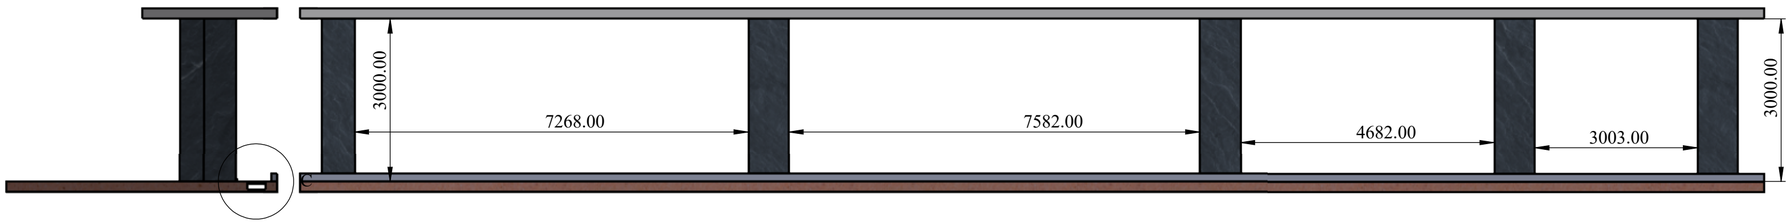

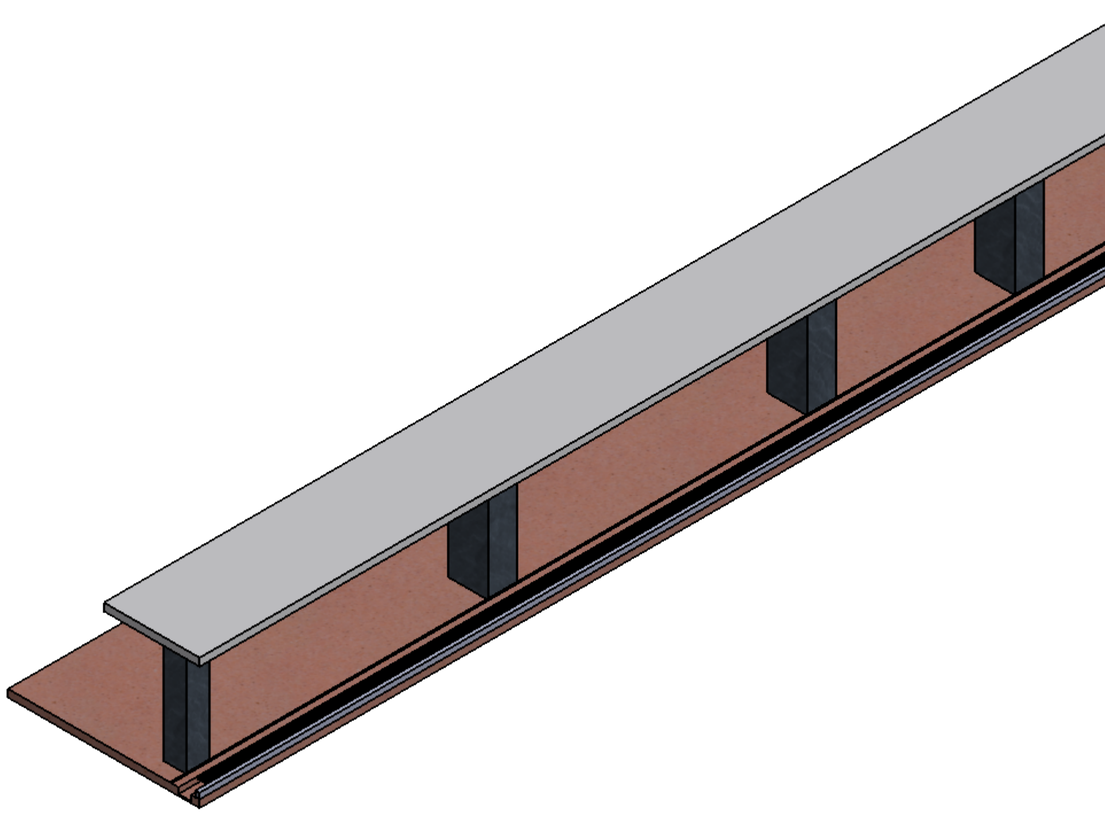

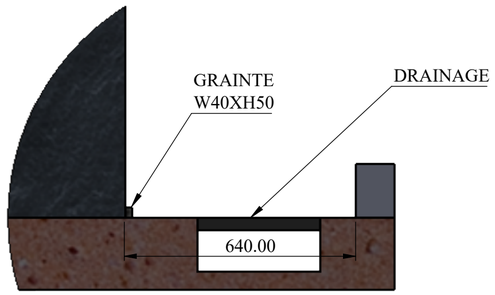

DETAIL C
SCALE 1 : 12

NOTE :

BASE STRCTURE IN CLIENT SCOPE

SPECIAL INSTRUCTION'S :

This drawing & design is the property of NIHVA TECHONOLOGIES PVT. LTD. Not to be sold or copied to any other concern

TITLE - ROOF AUTOMATION

DWG NO - NTPL-

NIHVA Technologies Pvt. Ltd.

NIHVA TECHNOLOGIES PVT.LTD.PUNE
Website - www.nihva.com

	NAME	SIGNATURE	DATE
DRAWN	V.W.		14-10-2026
CHK'D	S.P.		15-10-2026
APPV'D	V.T.		15-10-2026

PRODUCT - MANUAL BALCONY ENCLOSURE

CLIENT NAME - 24k.

SITE LOCATION - MUMBAI FORT.

MATRIAL -

QTY - 1

If any queries contact - info@nihva.com

ALL DIMENSION ARE IN mm

A2

PROJECTION METHOD:

SCALE :