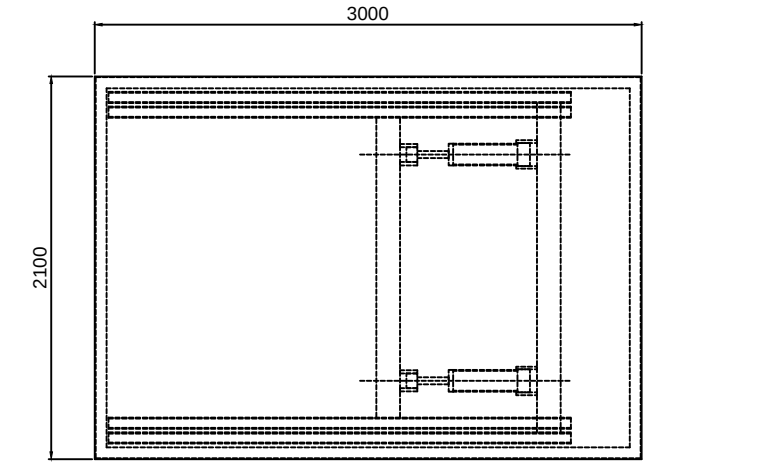

PLAN VIEW

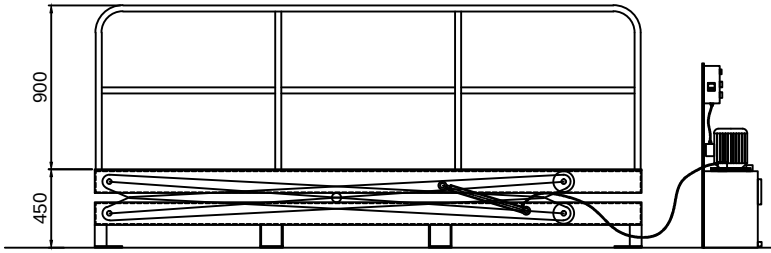

CLOSED FRONT VIEW

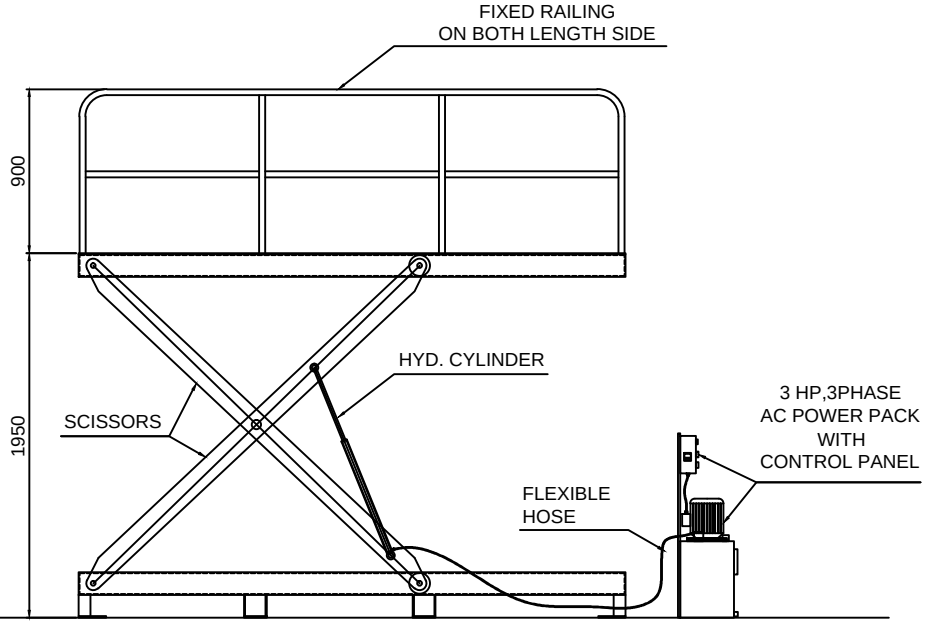

OPEN FRONT VIEW

SAFETY RAILING	900 MM			
POWER PACK	3HP , 3PHASE		FLEXIBLE HOSE	PARKER
LIFT HEIGHT	1500 MM		CONTROL PANEL	NIHVA
MAX HEIGHT	1950 MM		HYD. CYLINDER	NIHVA
SHUT HEIGHT	450 MM		SOLE. VALVE	YUKEN
PLATFORM SIZE	3000L X 2100W		HYD. PUMP	DOWTY
CAPACITY	1 TON		MOTOR	SIEMENS

NOTE :
1. HOSE BURST VALVE PROVIDE.
2. OVER LOAD RELAY & M.C.B IS IN CONTROL PANEL.

This drawing & design is the property of NIHVA TECHNOLOGIES. Not to be sold or copied to any other concern.

TITLE: SCISSOR LIFT

	NAME	SIGN	DATE
DRAWN	P.A		19.10.19
CHECK	G.J		19.10.19
APPRD.			

If any queries contact : design@nihva.com

ALL DIMENSION ARE IN mm

NIHVA TECHNOLOGIES PVT. LTD.
NIHVA TECHNOLOGIES PVT. LTD. PUNE
Tel : 020 66304033
Email:- info@nihva.com
Website:- www.nihva.com

CLIENT - TATA GLOBAL BEVERAGES LTD

PROJECT -

SITE LOCATION - HARYANA

DWG. NO. : NIHVA/19-20/0138

SCALE: NTS | WT: | REV- 00