

PRODUCED BY AN AUTODESK EDUCATIONAL PRODUCT

4000X5000

STRUCTURAL DETAILS

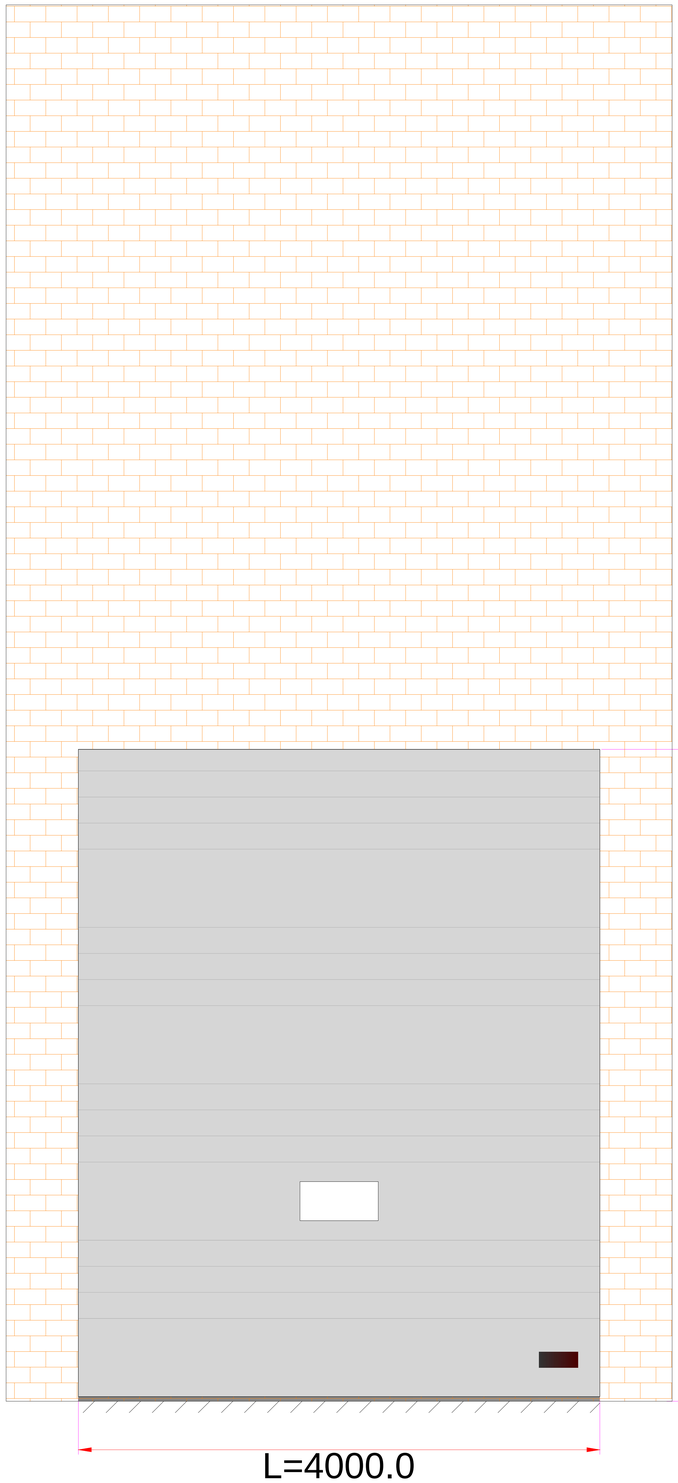

OUTSIDE VIEW

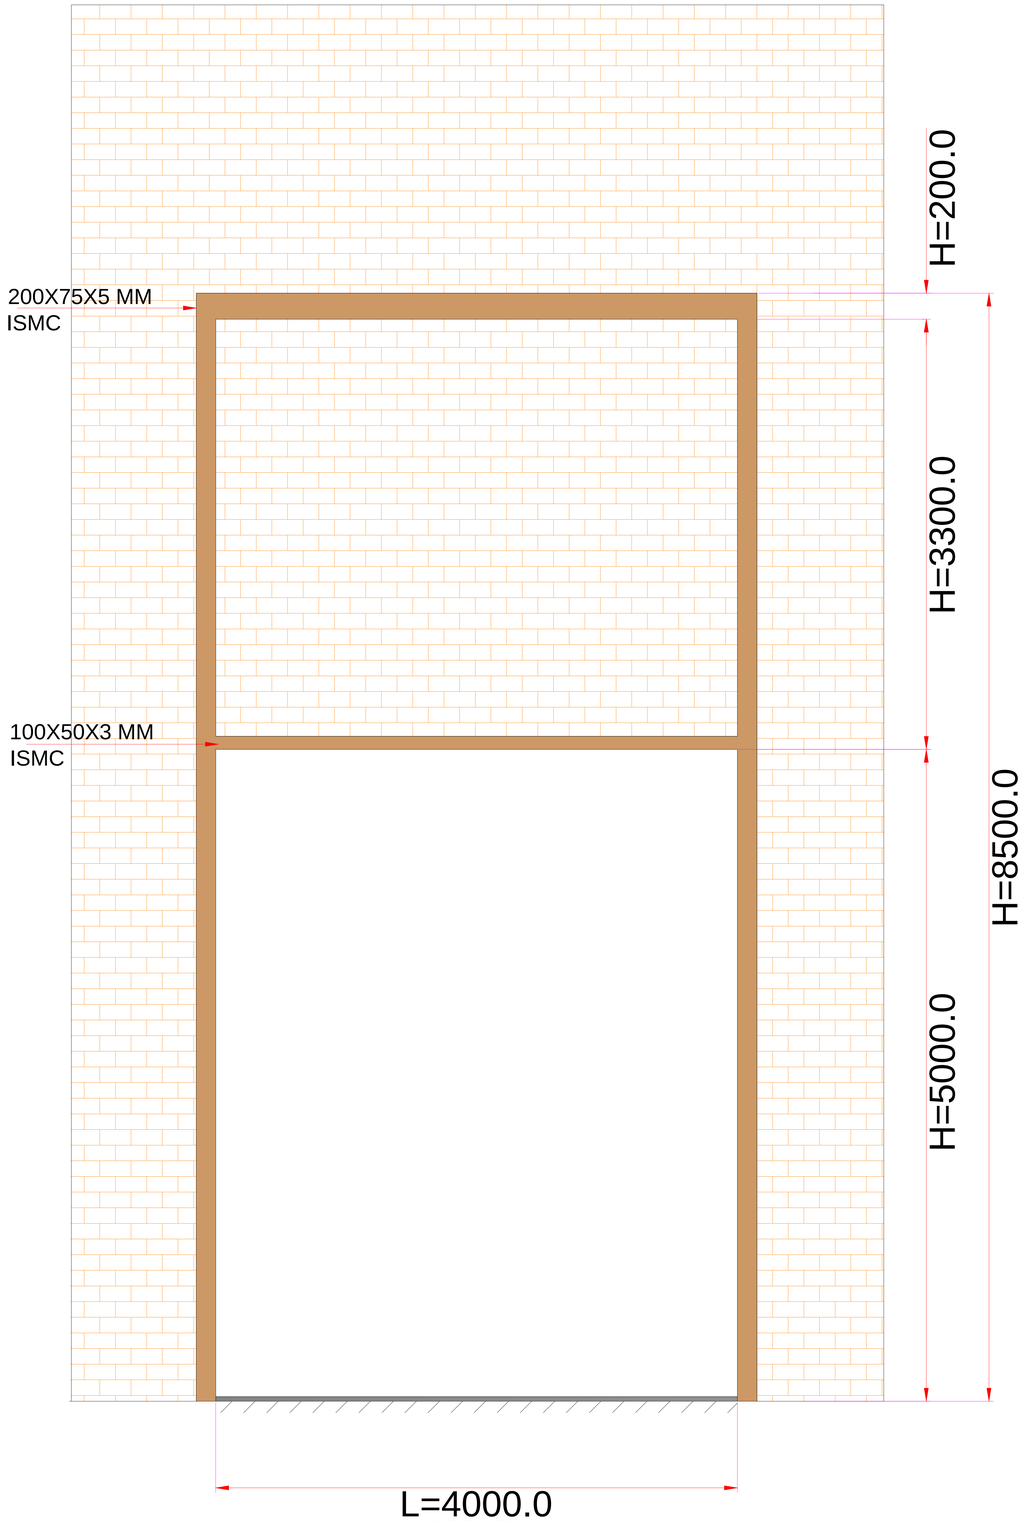

INSIDE VIEW

NOTE:-

LEGEND:-

SYMBOL	DESCRIPTION	QTY.

REVISION DETAILS :-

REVISION	DESCRIPTIONS	DATE
R 0	1. ATTENDANCE PURPOSE READER SHIFTED TO TS4 -P-D01	17.12.09

Released For :

Tender	Approval	Construction	As built
☐	☐	☐	☐

OWNERS :

PROJECT MANAGEMENT CONSULTANT :

SERVICE CONSULTANT :

ARCHITECTS :

TECHNOCRATS SECURITY SYSTEM PVT.LTD
Unit C-2, Modal Industrial Colony, Vishwedhwar Nagar , Road No.2,
Off. Aarey Road, Goregaon (E), Mumbai 63. E mail : design@technocrat.asia

PROJECT :

NIHVA

DRAWING TITLE :

SECTIONAL DOOR HORIZONTAL


JOB No.	DRG.NO.	REV.
------	------	------


SCALE:	DATE:	DRAWN:	CHKD :	APPVD:
NTS	6/12/2014	JACOB SANJAY		------


PRODUCED BY AN AUTODESK EDUCATIONAL PRODUCT
THIS DRAWING & DESIGNING IS THE PROPERTY OF TECHNOCRATS SECURITY SYSTEMS PVT. LTD. AND MUST NOT BE COPIED OR LENT WITHOUT THEIR PERMISSION IN WRITING.

D:\AUTOMATION PROJECT 2013\SECTIONAL DOORS\NIHVA SECTIONAL DOOR MANUAL VERTICAL\rev2\3600x4000x5000\NIHVA SECTIONAL DOOR .dwg, Layout1, 15-Dec-14 11:28:42 AM, Siva, DWG To PDF.pc3, Previous paper size (1189.00 x 841.00 MM), 1:23.7251

PRODUCED BY AN AUTODESK EDUCATIONAL PRODUCT

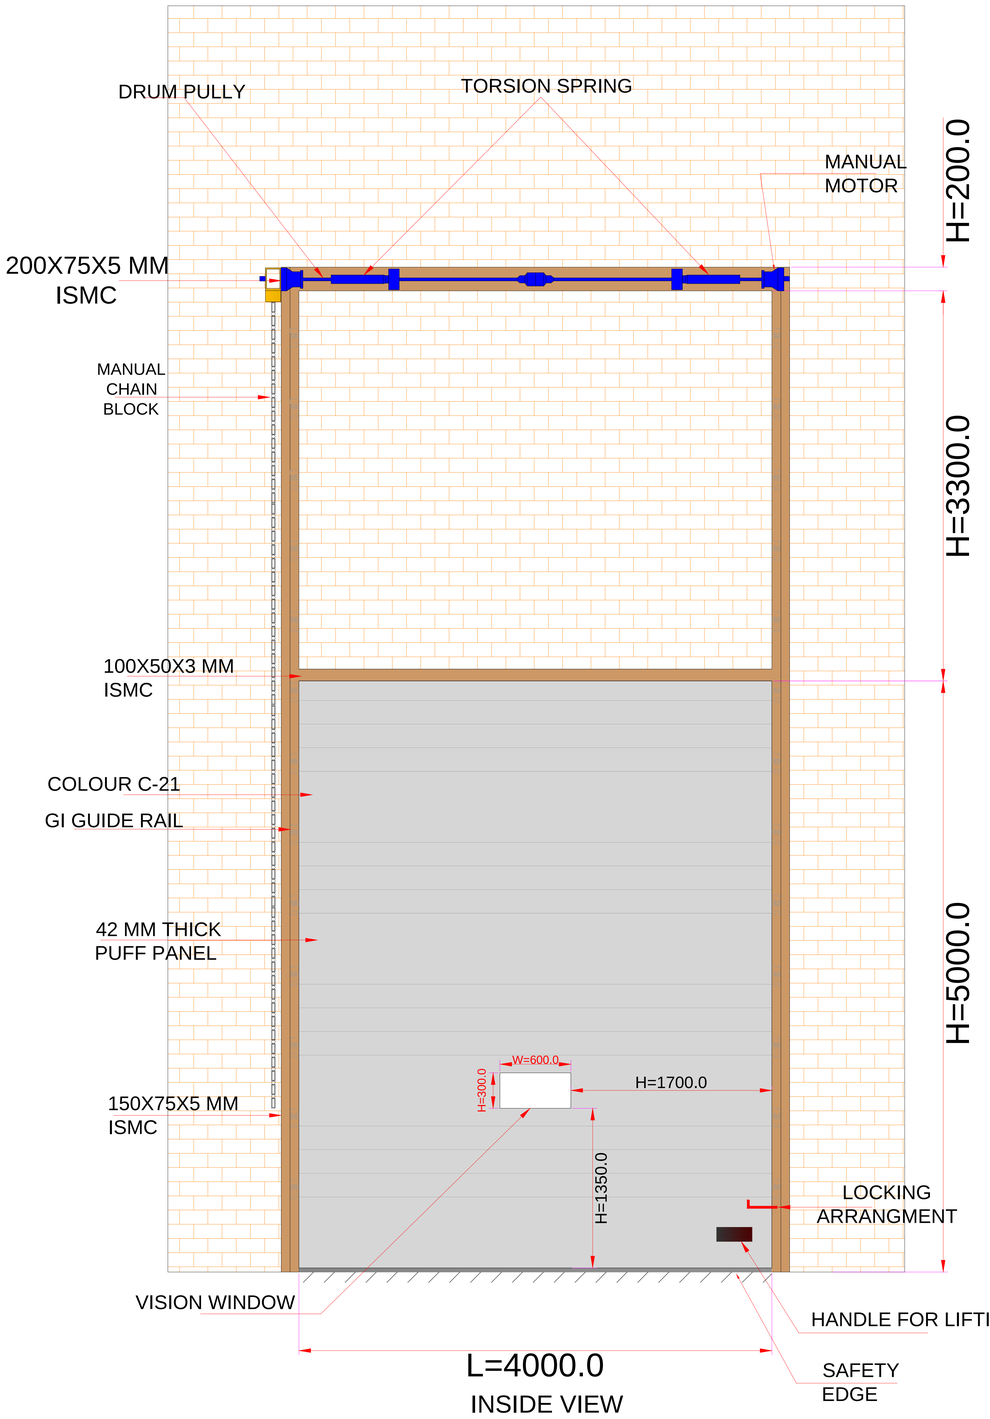

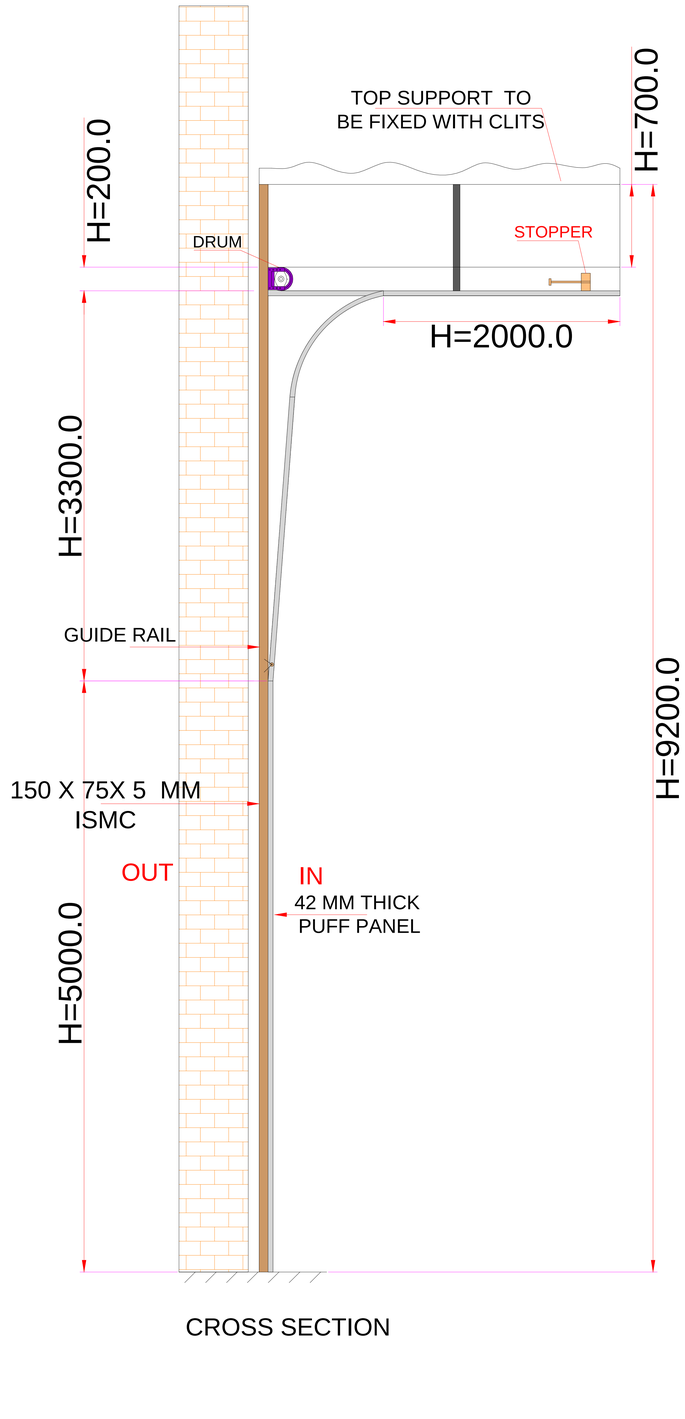

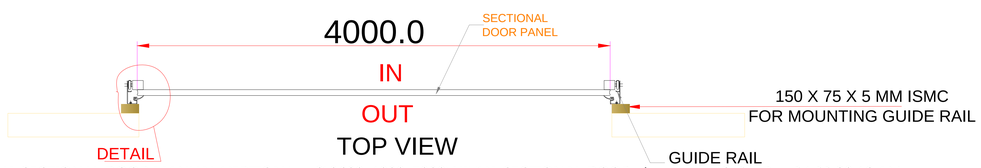

NOTE:-

LEGEND:-

SYMBOL	DESCRIPTION	QTY.

REVISION DETAILS :-

REVISION	DESCRIPTIONS	DATE
R 0	1. ATTENDANCE PURPOSE READER SHIFTED TO TS4 -P-D01	17.12.09

Released For :

Tender	Approval	Construction	As built
☐	☐	☐	☐

OWNERS :

PROJECT MANAGEMENT CONSULTANT :

SERVICE CONSULTANT :

ARCHITECTS :

TECHNOCRATS SECURITY SYSTEM PVT.LTD
Unit C-2, Modal Industrial Colony, Vishweshwar Nagar , Road No.2,
Off. Aarey Road, Goregaon (E), Mumbai 63. E mail : design@technocrat.asia

PROJECT :

NIHVA

DRAWING TITLE :

SECTIONAL DOOR HORIZONAL

JOB No.	DRG.NO.	REV.
------	------	------


SCALE:	DATE:	DRAWN:	CHKD :	APPVD:
NTS	6/12/2014	JACOB	SANJAY	------

THIS DRAWING & DESIGNING IS THE PROPERTY OF TECHNOCRATS SECURITY SYSTEMS PVT. LTD. AND MUST NOT BE COPIED OR LENT WITHOUT THEIR PERMISSION IN WRITING.

PRODUCED BY AN AUTODESK EDUCATIONAL PRODUCT

GUIDE RAIL

150 X 75 X 5 MM ISMC FOR MOUNTING GUIDE RAIL

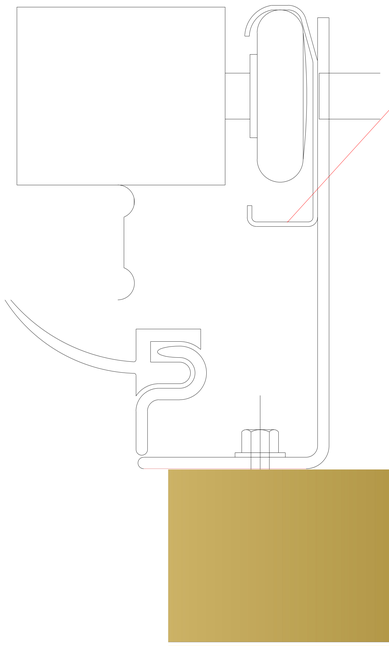

NOTE:-

LEGEND:-

SYMBOL	DESCRIPTION	QTY.

REVISION DETAILS :-

REVISION	DESCRIPTIONS	DATE
R 0	1. ATTENDANCE PURPOSE READER SHIFTED TO TS4 -P-D01	17.12.09

Released For :

Tender	Approval	Construction	As built
☐	☐	☐	☐

OWNERS :

PROJECT MANAGEMENT CONSULTANT :

SERVICE CONSULTANT :

ARCHITECTS :

TECHNOCRATS SECURITY SYSTEM PVT.LTD
THE SECURED WORLD
Unit C-2, Modal Industrial Colony, Vishweshwar Nagar , Road No.2,
Off. Aarey Road, Goregaon (E), Mumbai 63.. E mail : design@technocrat.asia

PROJECT :

NIHVA

DRAWING TITLE :

DETAIL OF GUIDE RAIL

	JOB No.	DRG.NO.	REV.
THE SECURED WORLD	------	------	------

SCALE:	DATE:	DRAWN:	CHKD :	APPVD:
NTS	6/12/2014	JACOB	SANJAY	------

THIS DRAWING & DESIGNING IS THE PROPERTY OF TECHNOCRATS SECURITY SYSTEMS PVT. LTD. AND MUST NOT BE COPIED OR LENT WITHOUT THEIR PERMISSION IN WRITING.

PRODUCED BY AN AUTODESK EDUCATIONAL PRODUCT

D:\AUTOMATION PROJECT 2013\SECTIONAL DOORS\NIHVA SECTIONAL DOOR MANUAL VERTICAL\rev2\3600x4000x5000\NIHVA SECTIONAL DOOR .dwg, Layout3, 15-Dec-14 11:28:51 AM, Siva, DWG To PDF.pc3, ISO A0 (841.00 x 1189.00 MM), 1:23.3273