| ITEM NO. | PART NUMBER | DESCRIPTION | MATERIAL | SIZE | QTY. |
|---|---|---|---|---|---|
| 1 | NTPL174-PLT04 | MS PLATE FOR CENTER STRUCTURE | MS | 85X45X3 MM THK | 10 |

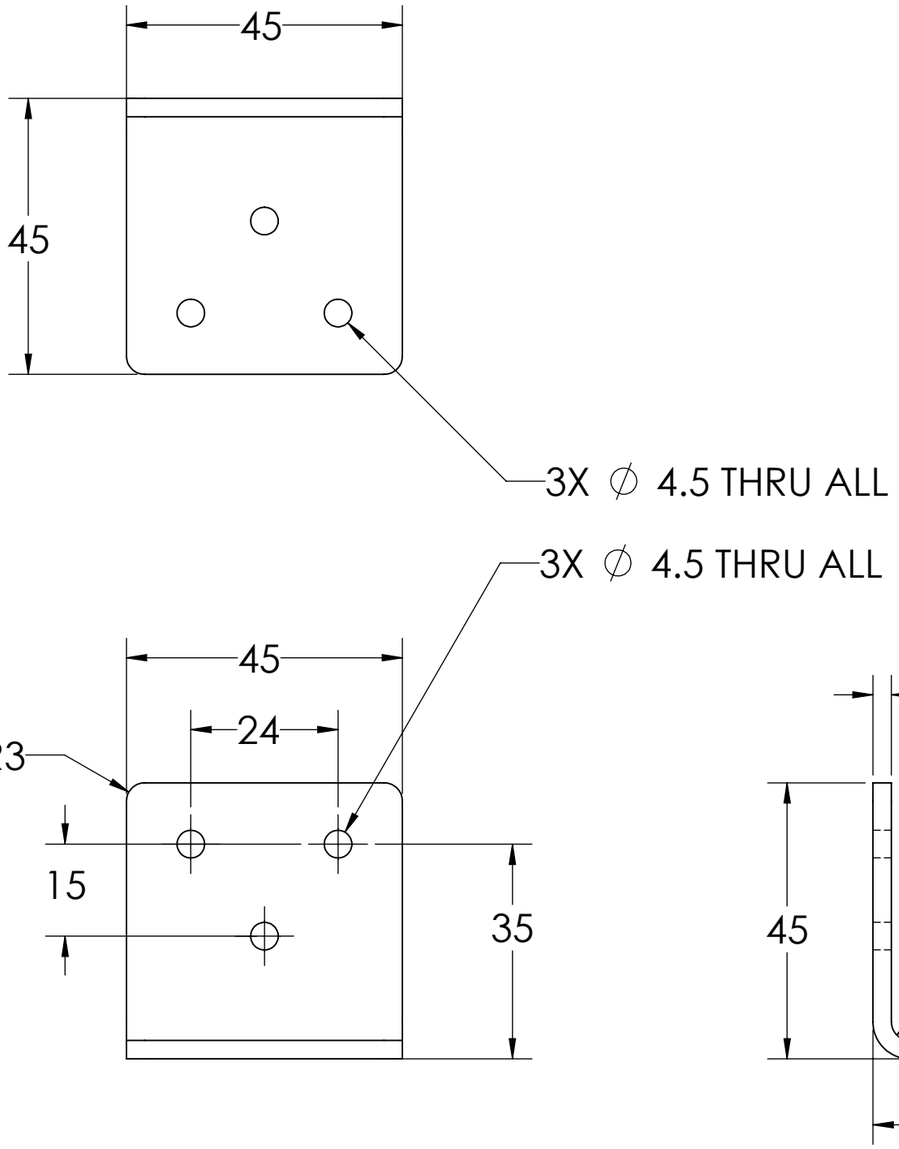


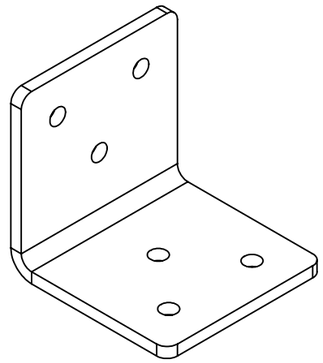

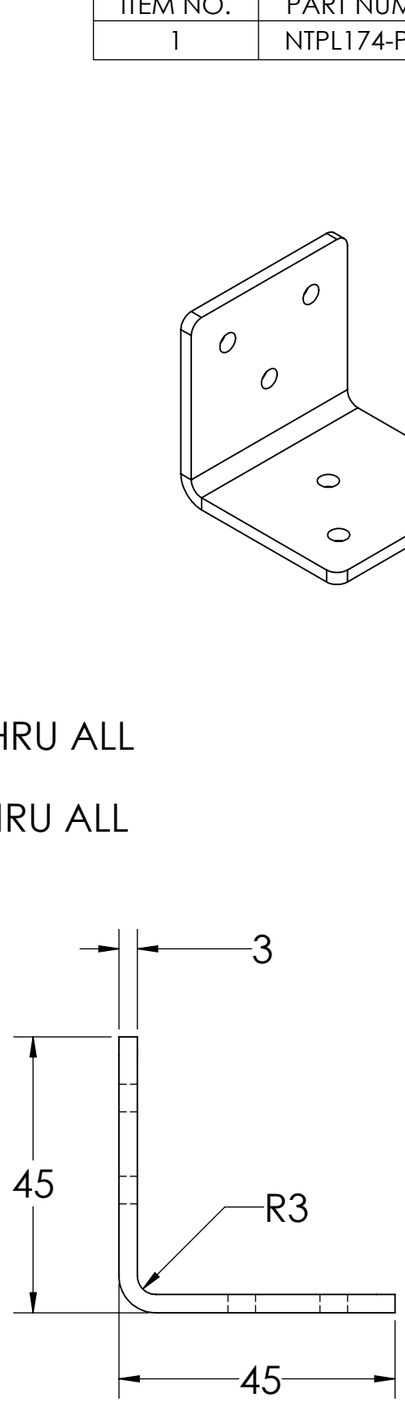


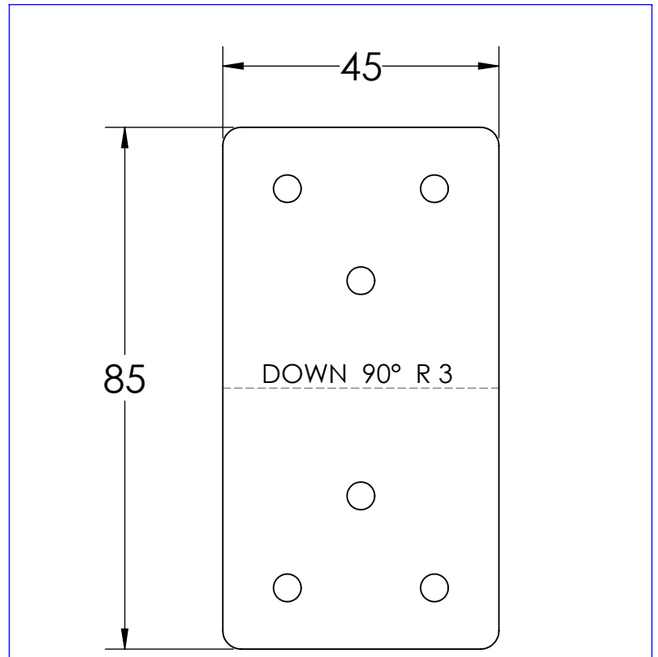


**FLAT PATTERN**

| | | | | |
|---|---|---|---|---|
| TITLE - MS PLATE FOR CENTER STRUCTURE | | | | NIHVA TECHNOLOGIES PVT.LTD.PUNE |
| DWG NO - NTPL174-PLT04 | | | QTY - 10 | Website - www.nihva.com |
| | NAME | SIGNATURE | DATE | PROJECT NO - NTPL174 |
| DRAWN | D.V. | | 20.06.2023 | PRODUCT - RETRACTABLE ROOF |
| CHK'D | P.M. | | 20.06.2023 | SITE LOCATION - |
| APPV'D | V.T. | | 20.06.2023 | |
| if any queries contact - supportautomation@nihva.com | | | | REVISION - |
| ALL DIMENSION ARE IN mm | | | A3 | SCALE - SHEET 1 OF 1 |