



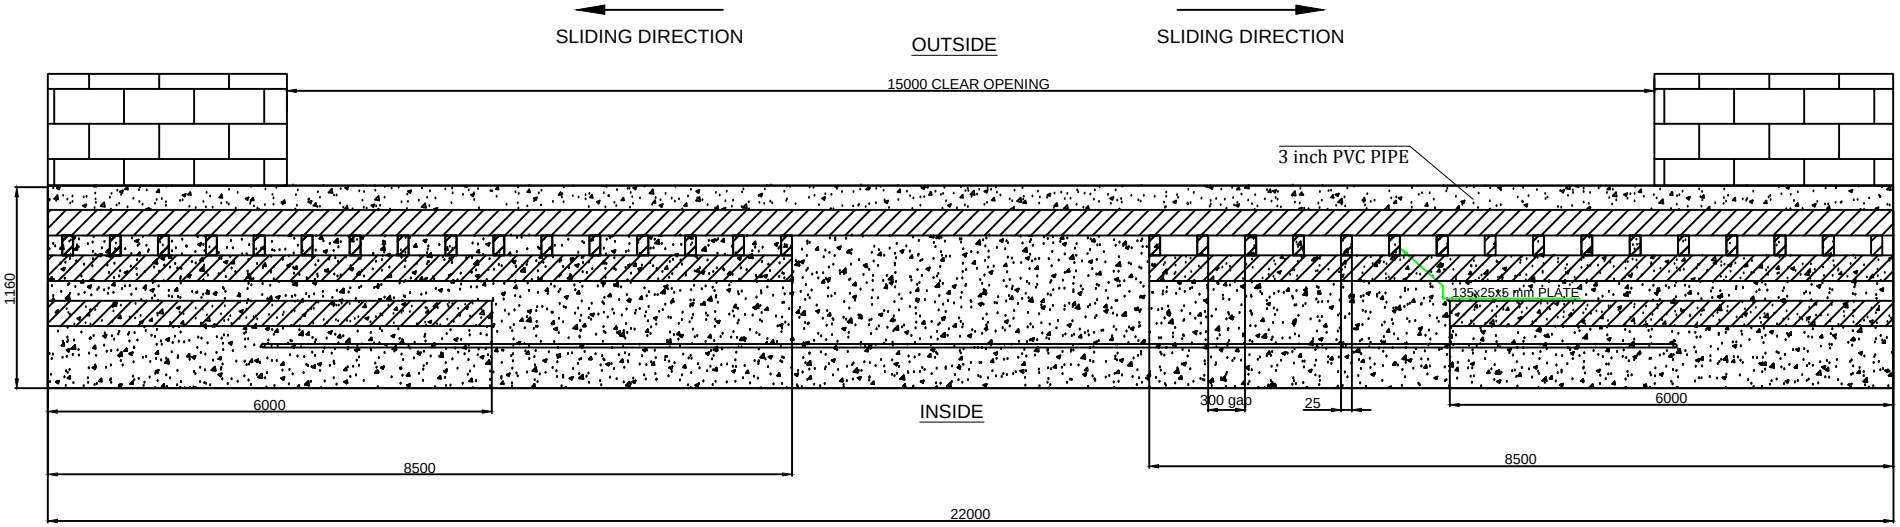

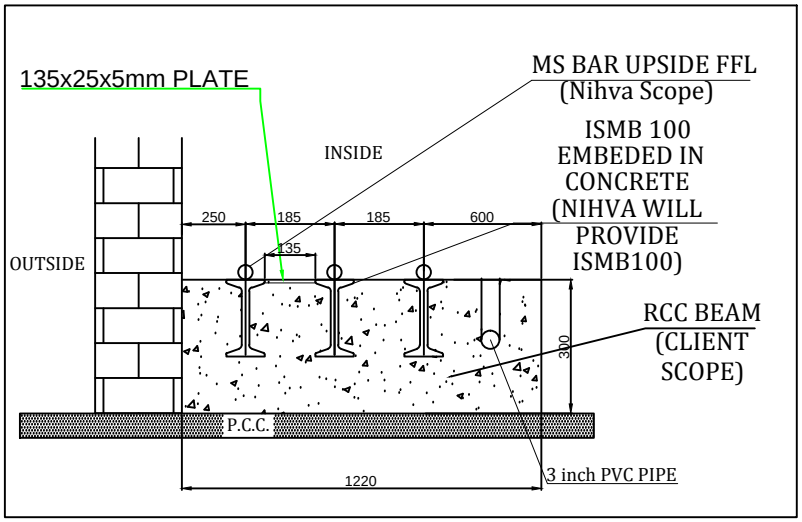

15m TELESCOPIC GATE FOUNDATION

This drawing & designing is the property of NIHVA TECHNOLOGIES. Not be sold or copy to any other concern.

TITLE

TELESCOPIC GATE FOUNDATION

CLIENT APPROVAL

ALL DIMENSION ARE IN mm

	SIGN	DATE
DRAWN	OMKAR	25/03/16
CHECK	ANIL	25/03/16
REV.	00	
APPRD.		
MFG		
Ref. No.		

NIHVA TECHNOLOGIES PVT. LTD.

NIHVA TECHNOLOGY PVT. LTD. PUNE
Tel : 020 66304033
Email:- info@nihva.com
Website:- www.nihva.com

CLIENT - TAIIN STEEL FAB & INFRA PVT.LTD.

PROJECT - HYOSUNG T&D

SITE -

DWG. NO. - NIHVA/15-16/242

SCALE: 01 | WT: | SHEET: 01 OF 01

If any queries contact : projects@nihva.com