

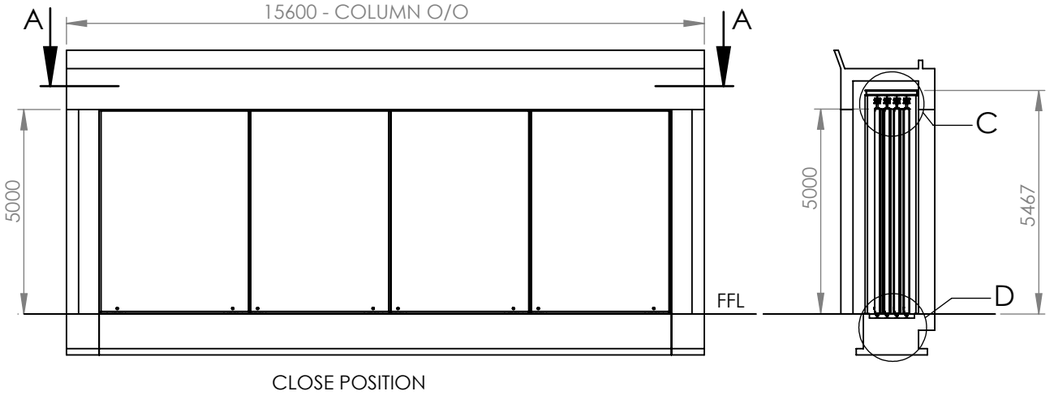



CLOSE POSITION

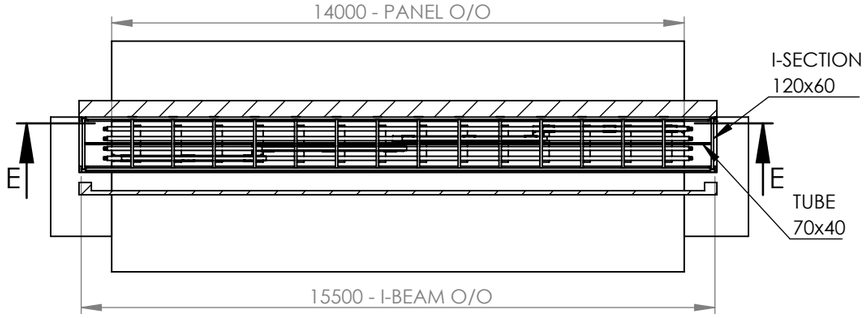


SECTION A-A

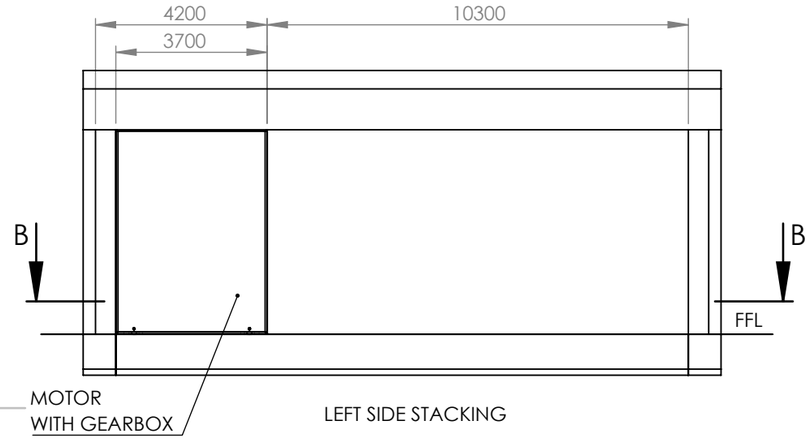


LEFT SIDE STACKING

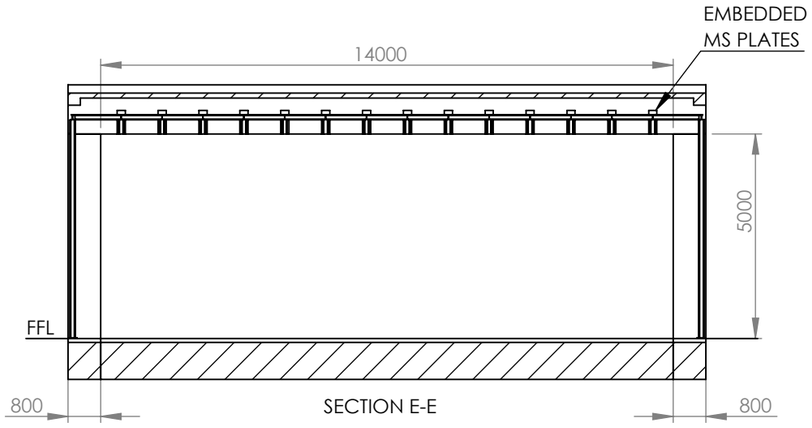


SECTION E-E

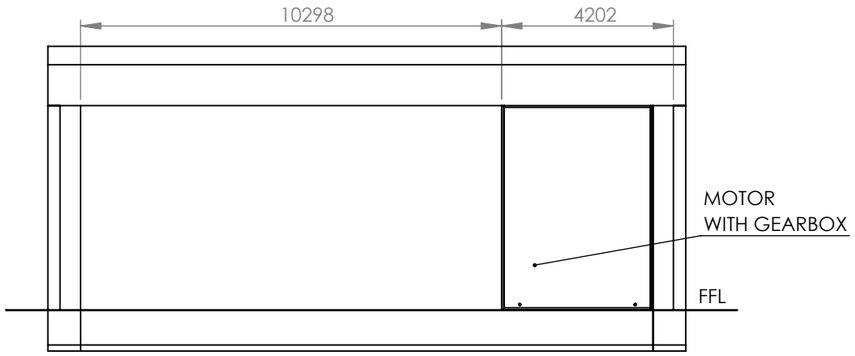


RIGHT SIDE STACKING

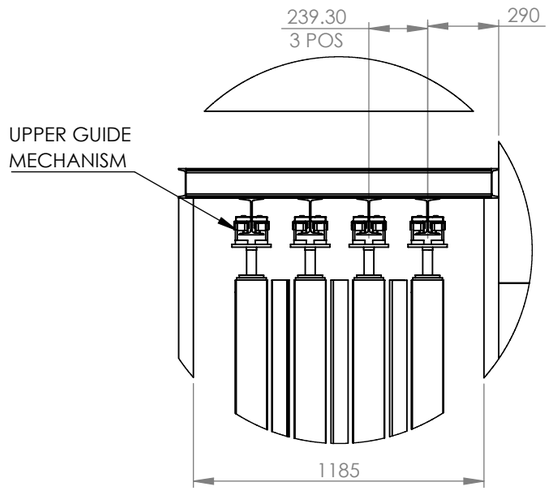


DETAIL C
SCALE 1 : 25

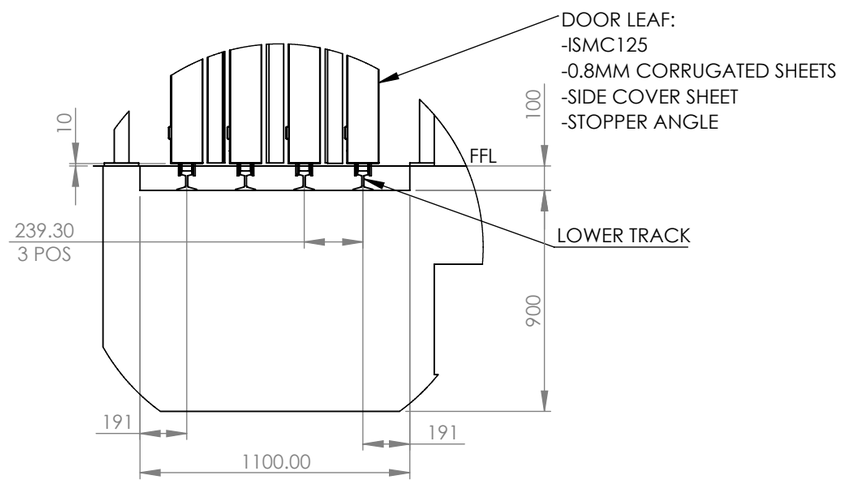

DETAIL D
SCALE 1 : 25

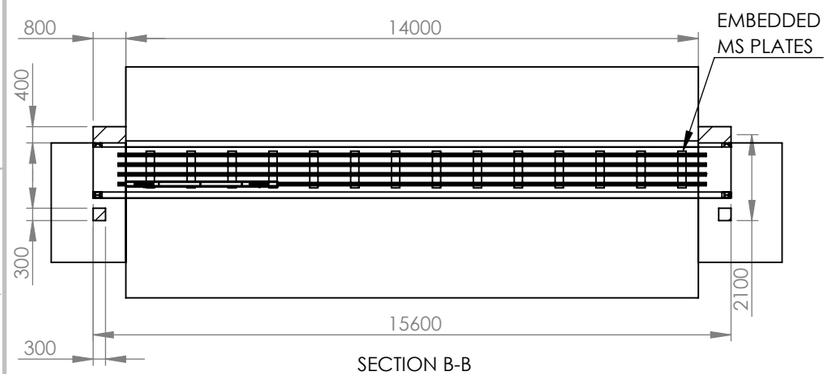

SECTION B-B

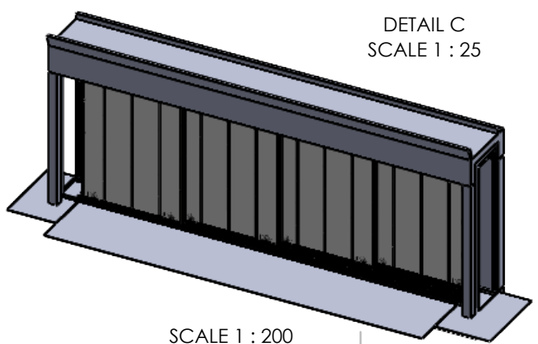

SCALE 1 : 200

TITLE : HANGING SLIDING DOOR

NIHVA Technologies Pvt. Ltd.

NIHVA TECHNOLOGIES PVT LTD

	NAME	SIGN	DATE
DRAWN	BHARATI SABALE		23-12-2024
CHK'D	SURAJ WARALE		23-12-2024
APPV'D	VIJAY T		23-12-2024

DIMENSIONS ARE IN MILLIMETERS

CLIENT NAME : ISRO

PRODUCT NAME : HANGING SLIDING DOOR

SITE LOCATION : ALUVA, KERALA

DWG NO. GA

A3

REVISION : 1

SCALE:

SHEET 1 OF 1