


Revision		Date	By
A	Corrected mullion hoist positions, floor pits altered	2022-09-02	EB

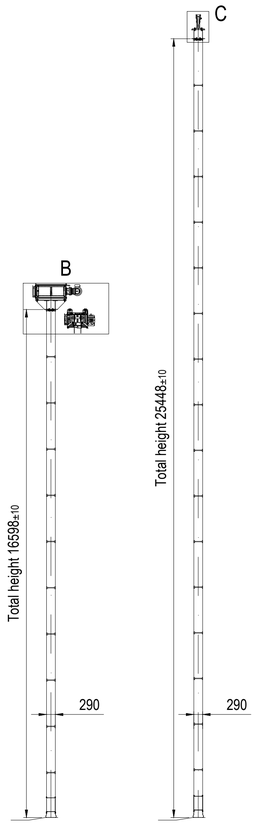


SECTION D-D SECTION E-E

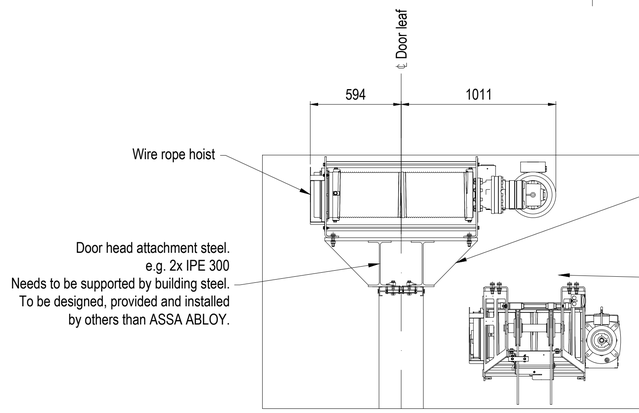


DETAIL B, SCALE (1:20)

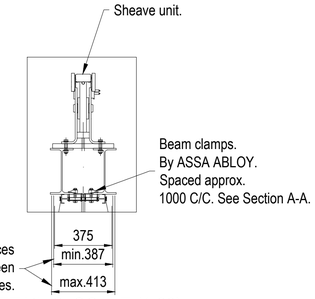


DETAIL C, SCALE (1:20)

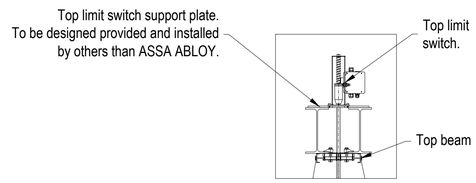

DETAIL D, SCALE (1:20)

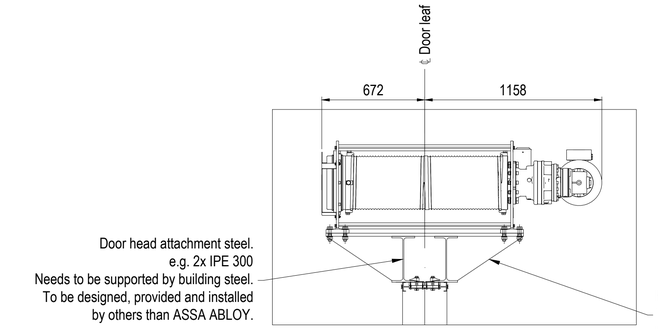


DETAIL E, SCALE (1:20)

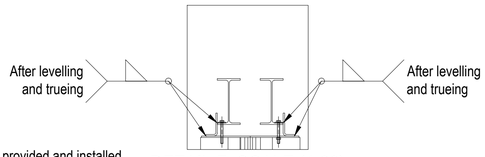


DETAIL F, SCALE (1:20)

D E F

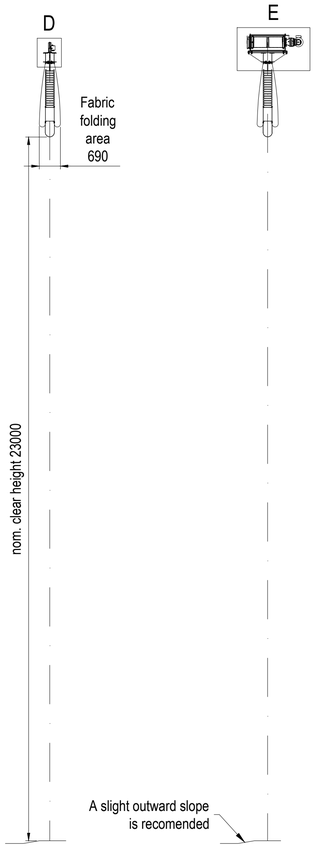


SECTION F-F


SECTION G-G

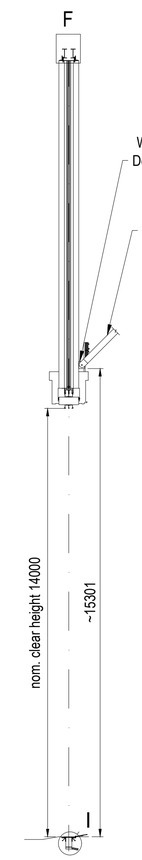


SECTION H-H

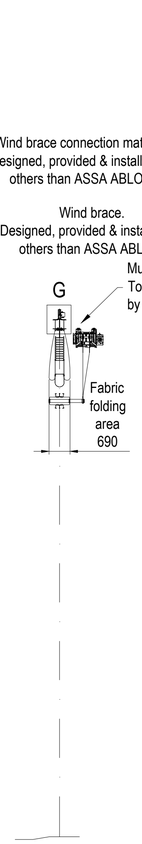


SECTION I-I

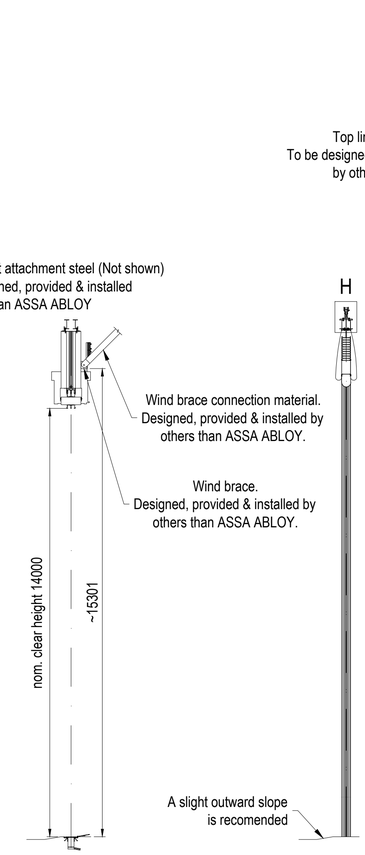


SECTION J-J SECTION K-K

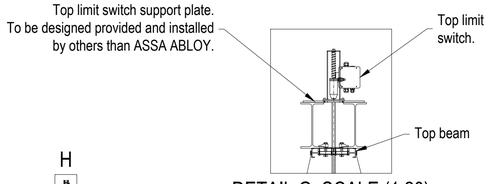

DETAIL G, SCALE (1:20)

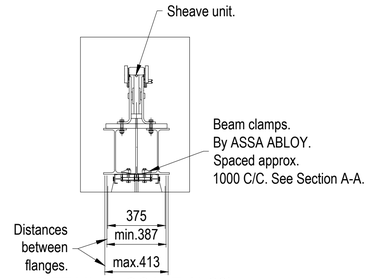

DETAIL H, SCALE (1:20)

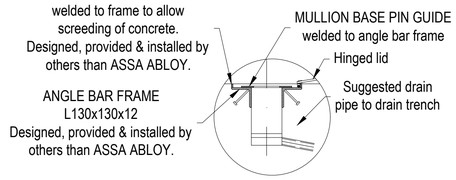

DETAIL I, SCALE (1:20)

DOOR IDENTITY NUMBER: 84800001

LOAD DIAGRAM & NOTES, ref. to drwng. no. 77446

INTERFACE, PLAN VIEWS ref. to drwng. no. 77444

INTERFACE, ELEVATION ref. to drwng. no. 77443

DESIGNED EB		SIZE A1	SCALE 1:100
CODE 84800	If not otherwise stated:		
ITEM NO	Tolerances ISO 2768-m EN ISO 13920-B		
DATE 2022-08-23	Cutting class ISO 9013-442		
	Weld class ISO 5817-C		
ASSA ABLOY	Surface finish Smooth raw surface		

GMR Aero Technic Hangar1

India

Megadoor 84000x23000/14000

Interface, sections

DRAWING NO 77445

REVISION A

PLOT DATE

This document is the property of ASSA ABLOY Entrance Systems AB and shall not be reproduced, transferred, disclosed or used in whole or in part for any purpose unless specifically authorized by the owner. It shall not be loaned to a third party or used for any other unauthorized purpose.