


SR.NO	DESCRIPTION	QTY
1	ISMC 200 X 75 X 3500L	2 NOS
2	ISMC 200 X 75 X 2988L	2 NOS
3	PROFILE 200 X 16 X 104L	4 NOS
4	R.TUBE 50 X 25 X 3THK X 1702L	10 NOS
5	R.TUBE 50 X 25 X 3THK X 545L	24 NOS
6	R.TUBE 50 X 25 X 3THK X 305L	6 NOS
7	R.TUBE 145 X 82 X 5.4 THK X 2988L	1 NO
8	FLAT 50 X 5 X 270L	6 NOS
9	CHEQ.SHEET 3000 X 5 X 3500L	1 NO
10	M10 X 25L WITH SPRING WASHER	12 NOS

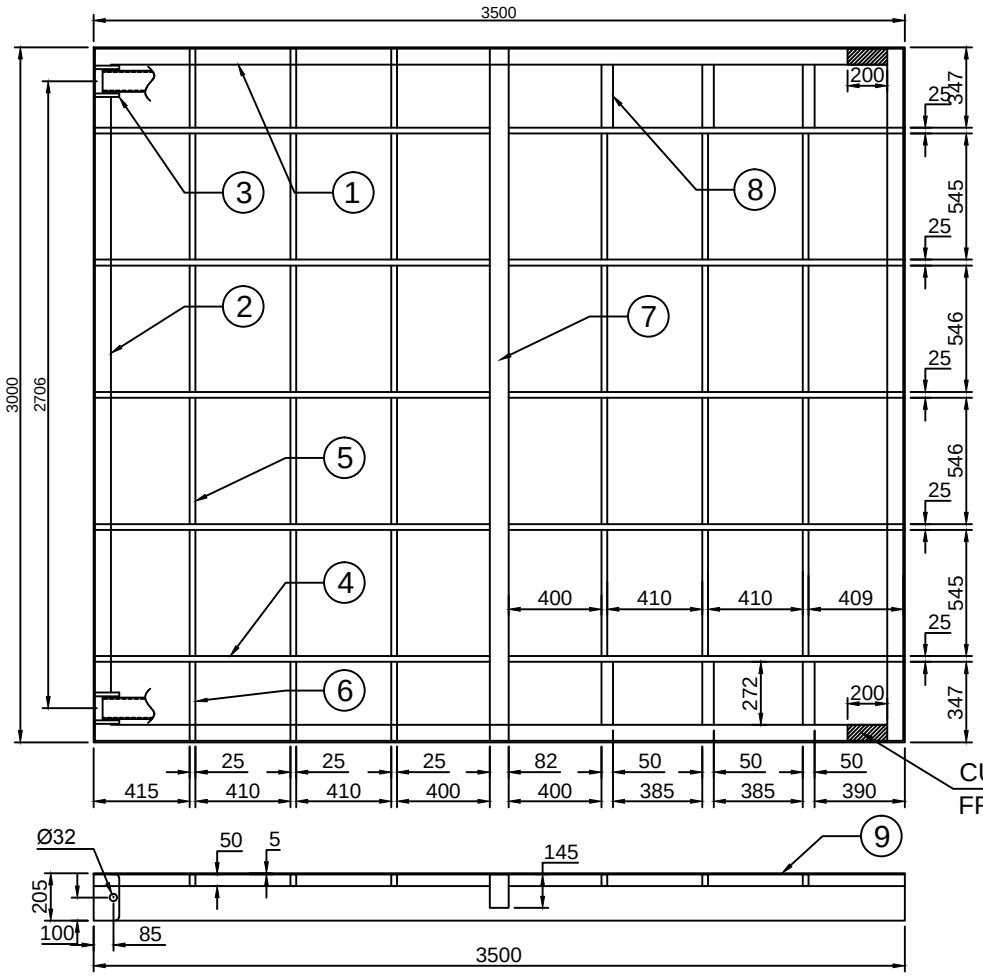

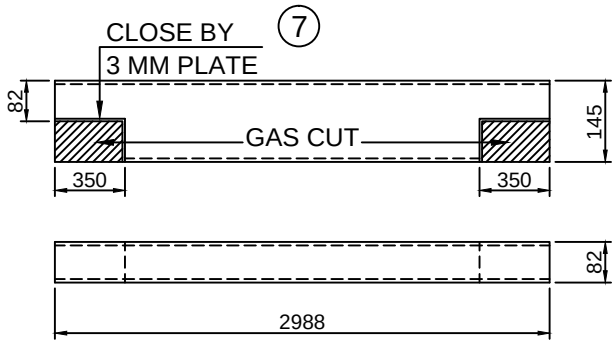

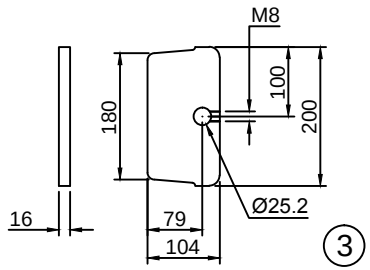

This drawing & design is the property of NIHVA TECHNOLOGIES. Not to be sold or copied to any other concern.

TITLE : -
TOP FRAME

NIHVA TECHNOLOGIES PVT. LTD.

NIHVA TECHNOLOGIES PVT. LTD. PUNE
Tel : 020 66304033
Email:- info@nihva.com
Website:- www.nihva.com

	SIGN	DATE
DRAWN	P.A	03.05.2019
CHECK		
REV.		
APPROVAL		

CLIENT -
PROJECT -
SITE -
DWG. NO. : NIHVA/19-20/VDR/006

If any queries contact : projects@nihva.com
SCALE: NTS | WT: | SHEET: 01 OF 01
ALL DIMENSION ARE IN mm