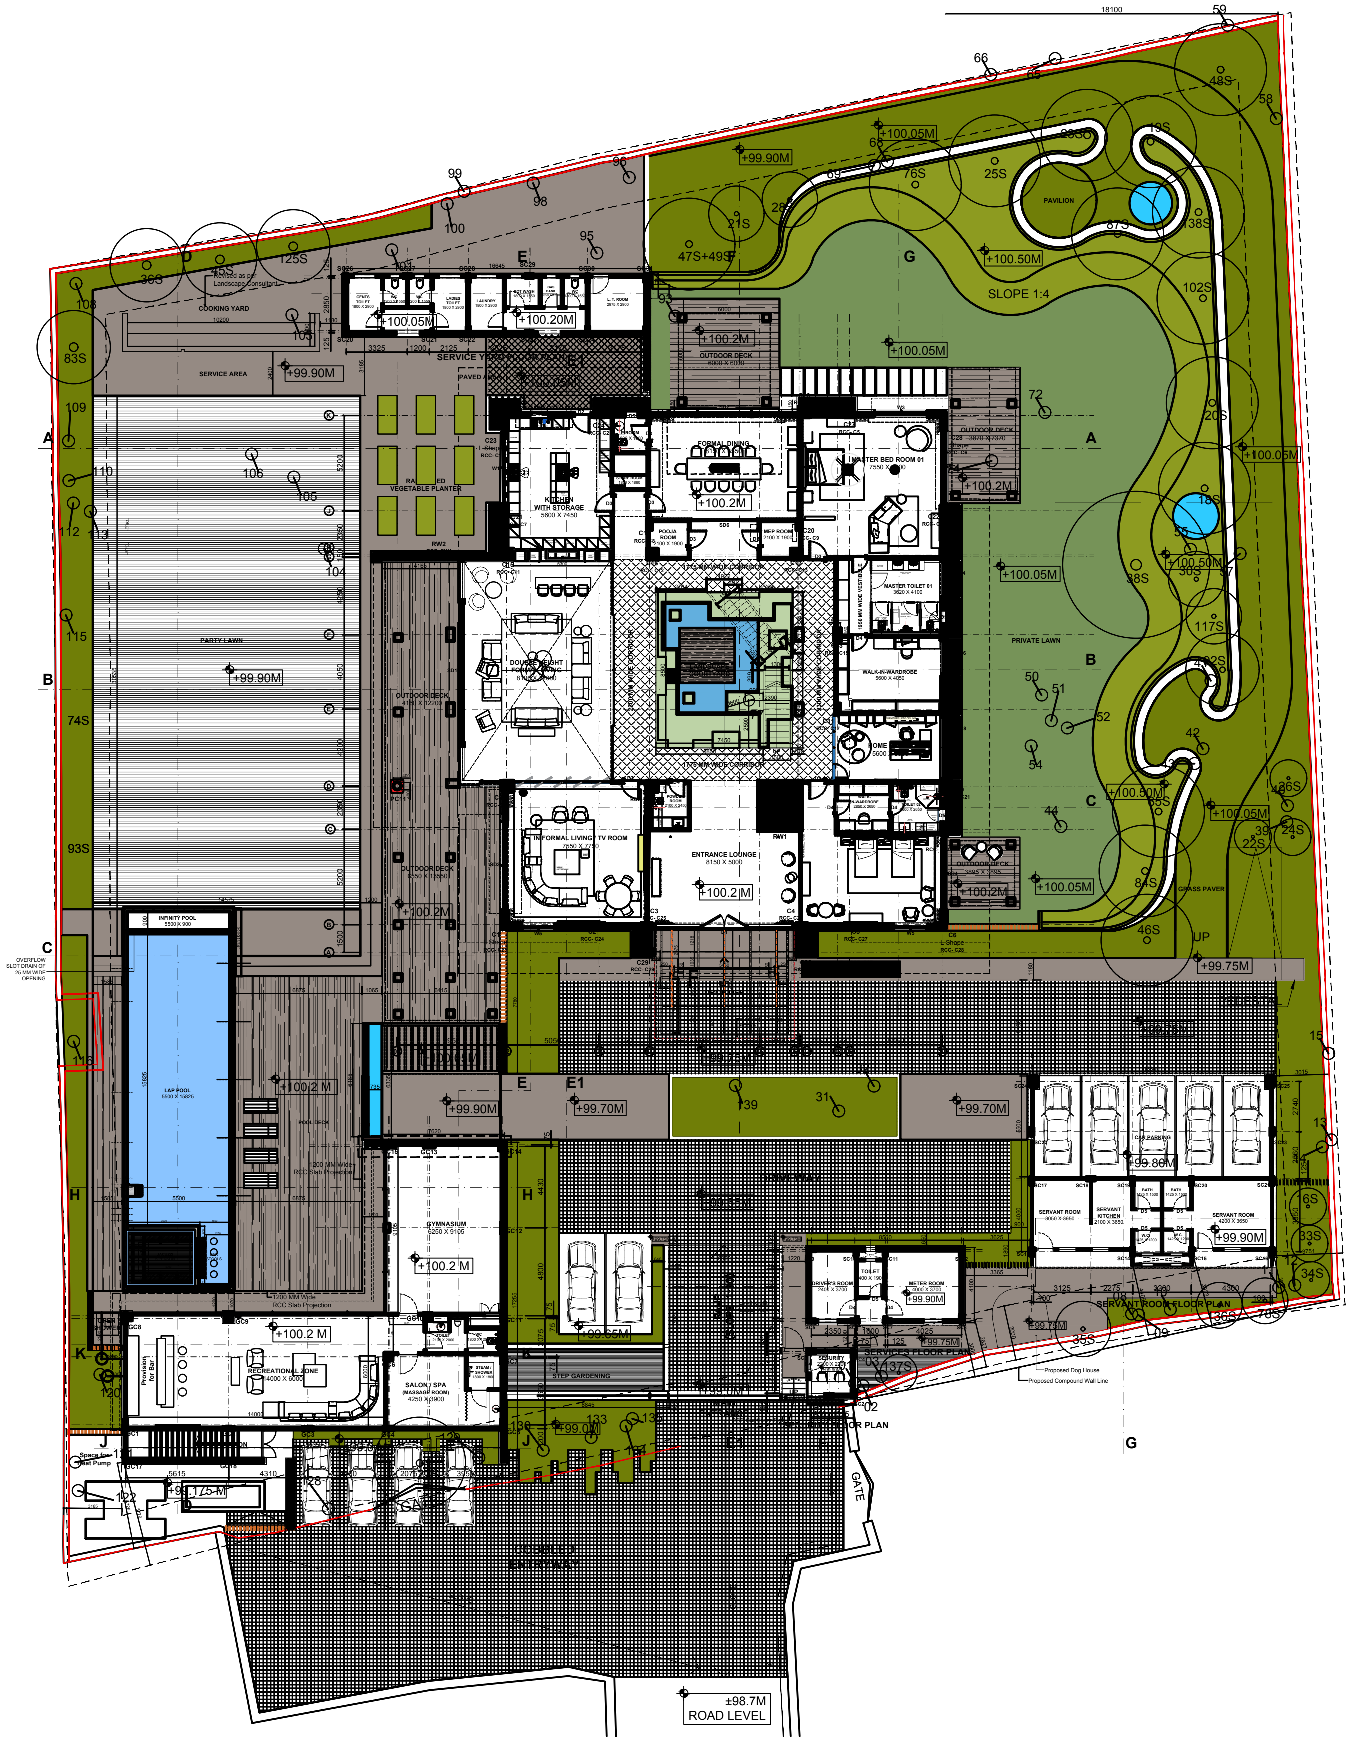
SERVICE YARD FLOOR PLAN
PAVED AREA
COOKING YARD
SERVICE AREA
LADIES TOILET
LAUNDRY
POT WASH
GAS BANK
L. T. ROOM
+100.05M
+100.20M
RAISED VEGETABLE PLANTER
KITCHEN WITH STORAGE 5600 X 7450
STORE ROOM
FORMAL DINING
+100.2M
POOJA ROOM 2100 X 1900
MEP ROOM 2100 X 1900
MASTER BED ROOM 01 7550 X 4500
OUTDOOR DECK 3870 X 7370
OUTDOOR DECK 6000 X 6000
MASTER TOILET 01 3620 X 4100
1950 MM WIDE VESTIBULE
WALK-IN-WARDROBE 5600 X 4050
HOME
1775 MM WIDE CORRIDOR
LANDSCAPE COURTYARD
DOUBLE HEIGHT FORMAL LIVING 8100 X 12050
OUTDOOR DECK 4160 X 12200
OUTDOOR DECK 6550 X 13550
INFORMAL LIVING / TV ROOM 7550 X 7750
POWDER ROOM 2100 X 2450
ENTRANCE LOUNGE 8150 X 5000
WALK-IN-WARDROBE 2850 X 2650
TOILET 02 2500 X 2650
OUTDOOR DECK 3895 X 3895
PARTY LAWN
+99.90M
PRIVATE LAWN
PAVILION
SLOPE 1:4
GRASS PAVER
+100.05M
+100.50M
+99.75M
INFINITY POOL
LAP POOL
1200 MM Wide RCC Slab Projection
+100.2 M
GYMNASIUM 6250 X 9105
RECREATIONAL ZONE 14000 X 6000
Provision for Bar
SALON / SPA (MASSAGE ROOM) 4250 X 3900
STEAM / SHOWER 1800 X 1800
OPEN SHOWER
Space for Heat Pump
STEP GARDENING
+99.70M
+99.65M
+99.80M
CAR PARKING
SERVANT ROOM
SERVANT KITCHEN
SERVANT ROOM FLOOR PLAN
DRIVER'S ROOM 2400 X 3700
TOILET
METER ROOM 4000 X 3700
SECURITY 2200 X 2200
SERVICES FLOOR PLAN
+99.75M
GATE
COBBLED ENTRYWAY
Proposed Dog House
Proposed Compound Wall Line
OVERFLOW SLOT DRAIN OF 25 MM WIDE OPENING
±98.7M ROAD LEVEL
A
B
C
H
J
K
E
E1
G
18100