



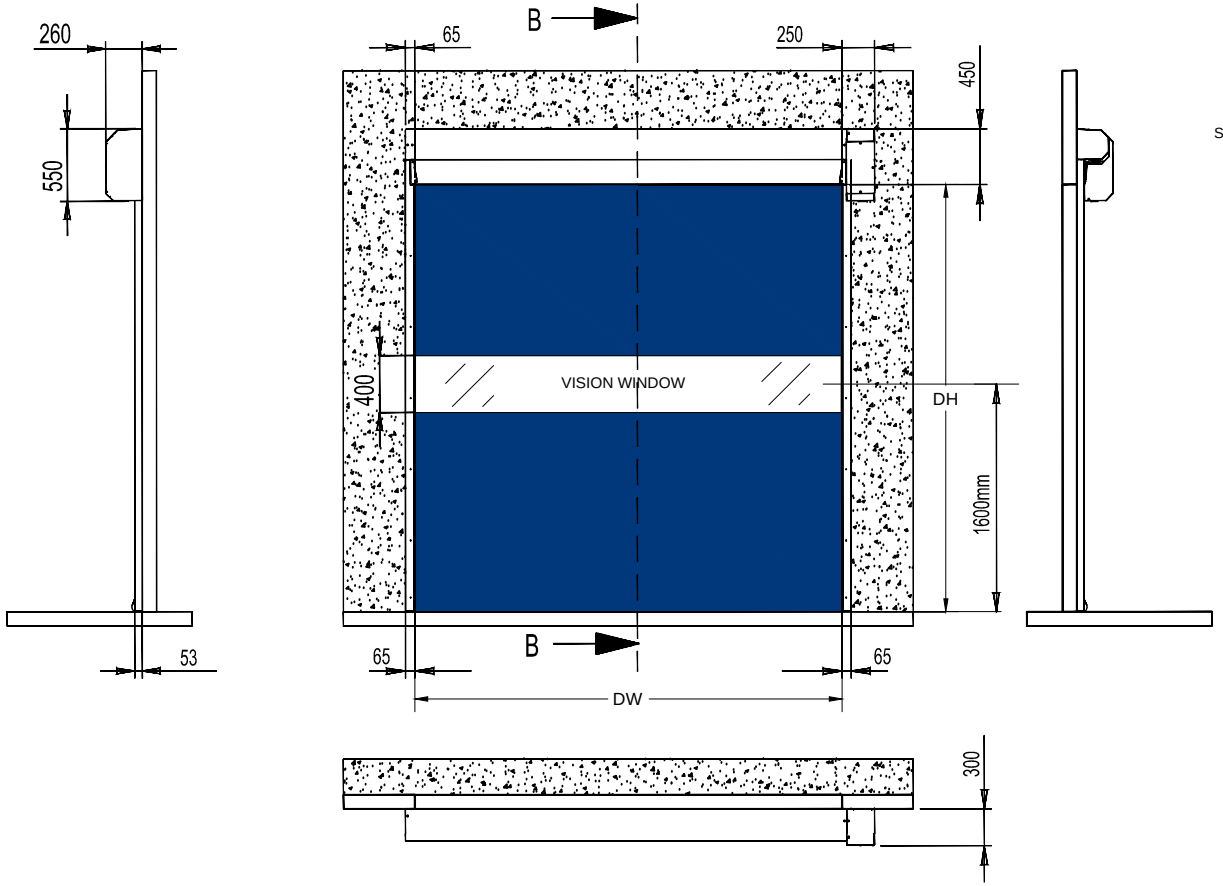

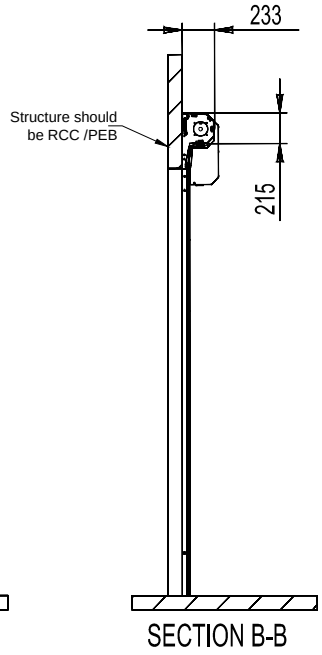

DOOR DIMENSION					
SR NO	DW	DH	MOTOR LOCATION		QUANTITY
			RIGHT	LEFT	
1	2000	2200			01

Note-
1. All Civil work will be in clients scope.
2. Client has to choose motor side (Right/left) according to the site conditions. Standard door comes with Right side Motor mounting.
3. All Construction in stainless steel AISI304

This drawing & designing is the property of NIHVA TECHNOLOGIES. Not to be sold or copied to any other concern.

TITLE
HIGH SPEED DOOR
HS9020GHY.

NIHVA
NIHVA TECHNOLOGIES PVT. LTD.

NIHVA TECHNOLOGIES
PVT. LTD. PUNE
Tel : 020 66304033
Email:- info@nihva.com
Website:- www.nihva.com

	NAME	SIGN	DATE
DRAWN	P.V.A		16.04.19
CHECK	V.M.T		16.04.19
APPROVAL			

CLIENT - EMCURE PHARMACEUTICALS PVT. LTD .
PROJECT - EMCURE PHARMACEUTICALS PVT. LTD .
SITE - Pune
If any queries contact : design@nihva.com
DWG. NO. : NIHVA/19-20/0005
REV- 00
ALL DIMENSION ARE IN mm
SCALE: NTS
WT:
SHEET: 01 OF 01