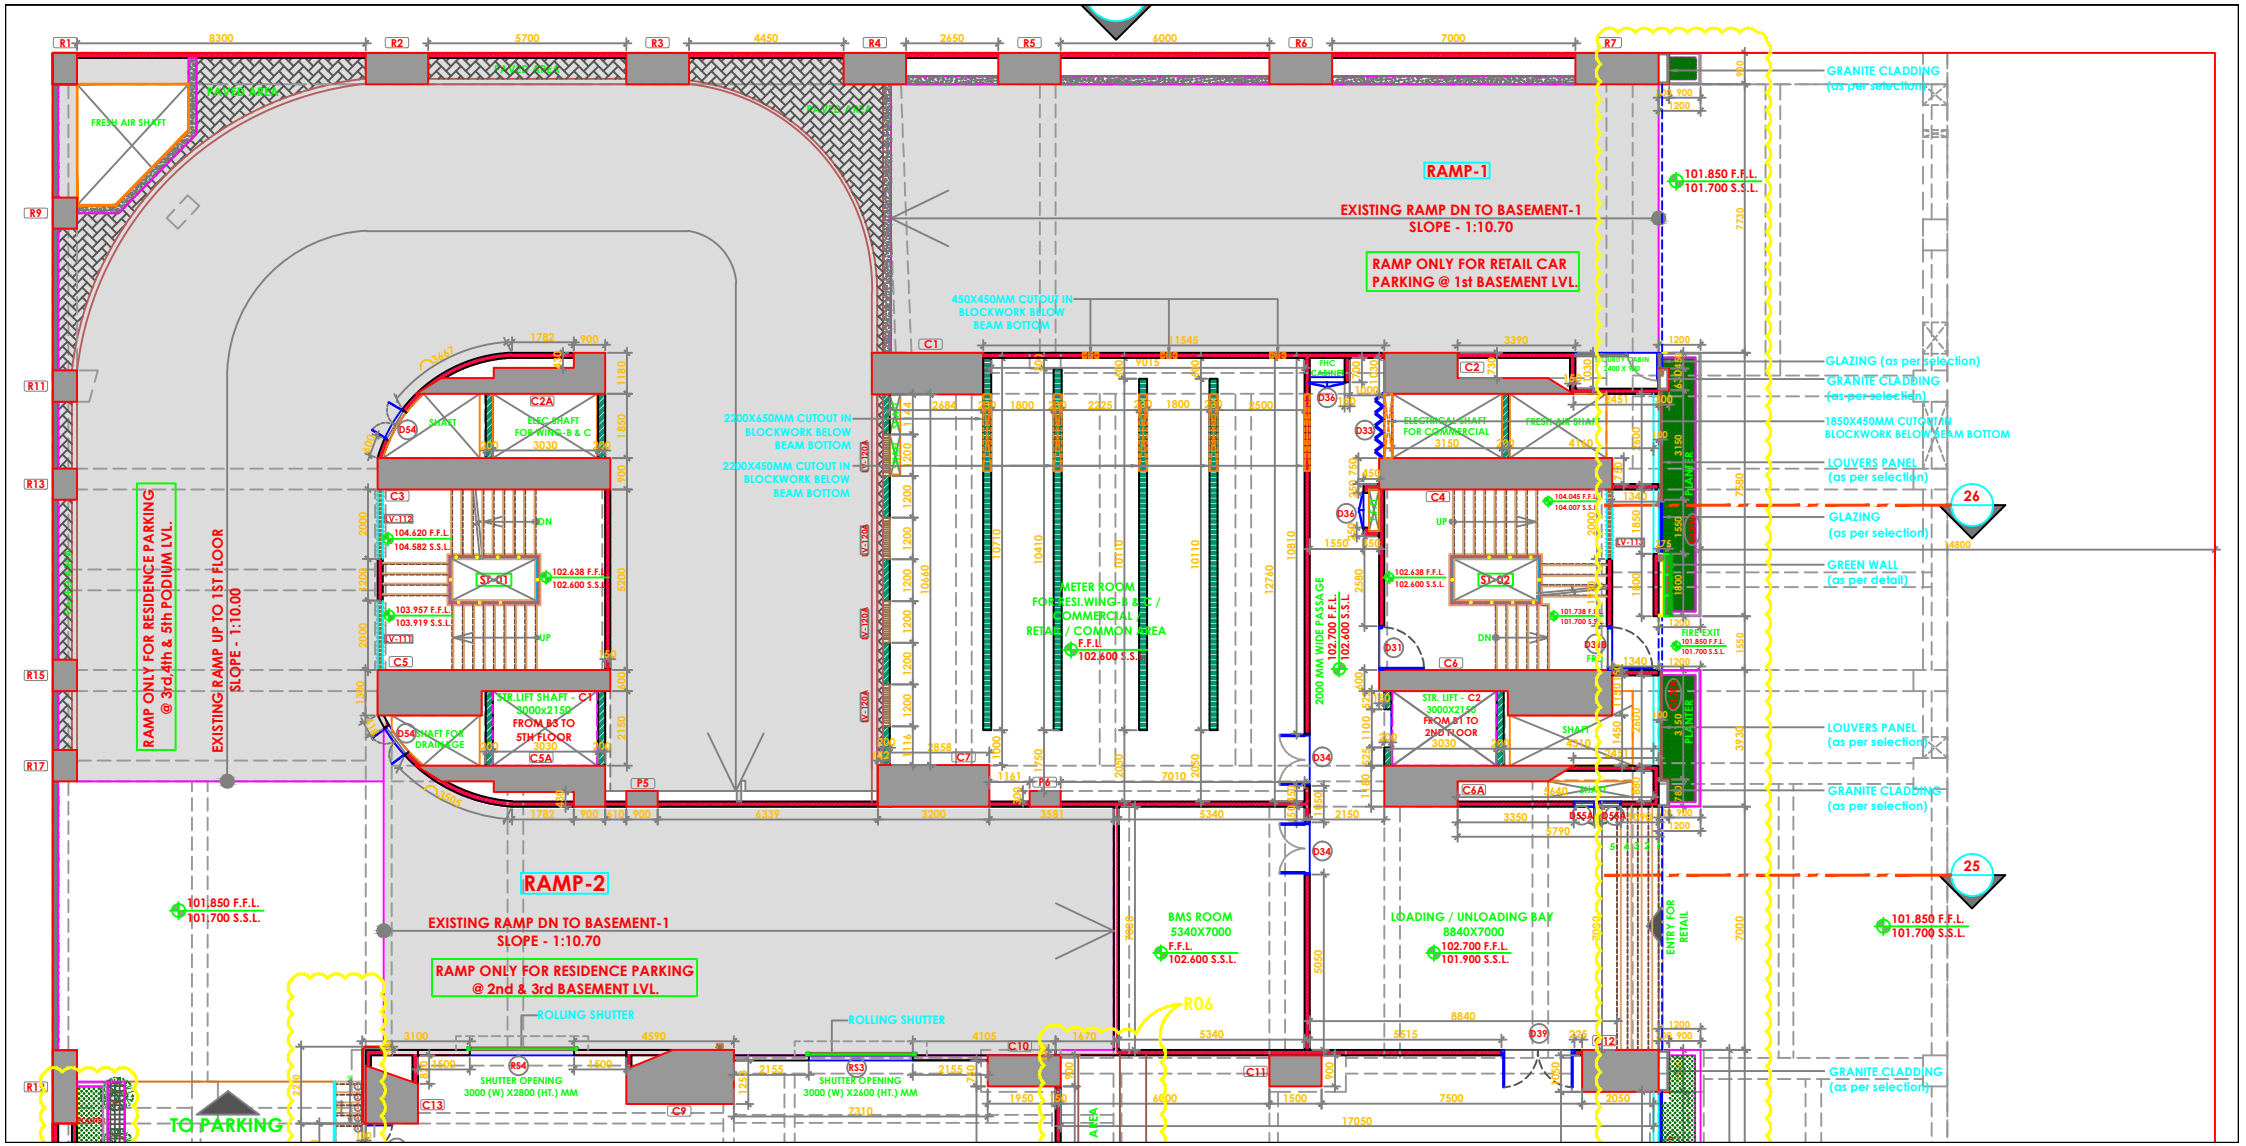

RAMP-1
EXISTING RAMP DN TO BASEMENT-1
SLOPE - 1:10.70
RAMP ONLY FOR RETAIL CAR PARKING @ 1st BASEMENT LVL.
RAMP-2
EXISTING RAMP DN TO BASEMENT-1
SLOPE - 1:10.70
RAMP ONLY FOR RESIDENCE PARKING @ 2nd & 3rd BASEMENT LVL.
RAMP ONLY FOR RESIDENCE PARKING @ 3rd,4th & 5th PODIUM LVL.
EXISTING RAMP UP TO 1ST FLOOR
SLOPE - 1:10.00
TO PARKING
METER ROOM FOR RESI.WING-B &C / COMMERCIAL RETAIL / COMMON AREA
BMS ROOM 5340X7000
LOADING / UNLOADING BAY 8840X7000
ENTRY FOR RETAIL
FRESH AIR SHAFT
GRANITE CLADDING (as per selection)
GLAZING (as per selection)
LOUVERS PANEL (as per selection)
GREEN WALL (as per detail)
ROLLING SHUTTER
SHUTTER OPENING 3000 (W) X2800 (HT.) MM
SHUTTER OPENING 3000 (W) X2600 (HT.) MM
2000 MM WIDE PASSAGE
101.850 F.F.L.
101.700 S.S.L.