
## LOCATION AREA :- SEZ 6 - SECOND FLOOR- EXIT

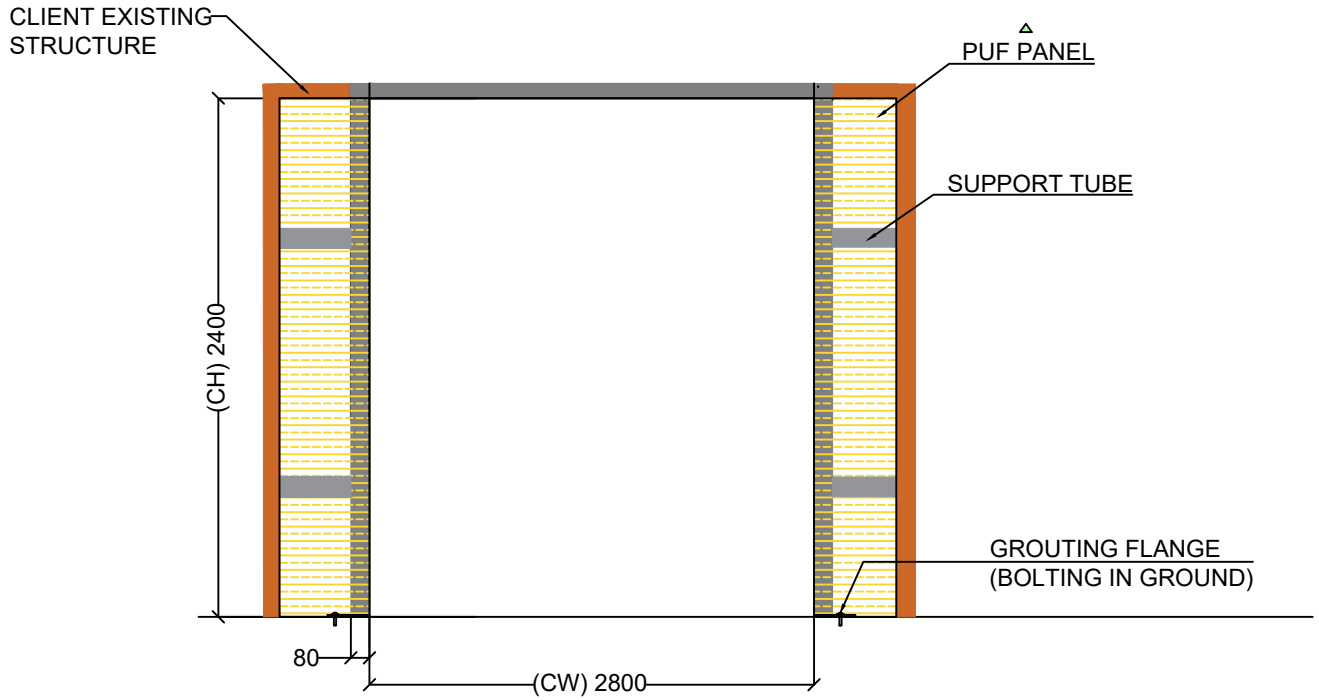


### M.S. STRUCTURE DETAILS

| Clear Width (CW) | Clear Height (CH) | QTY |
|---|---|---|
| **2800** | **2400** | 02 |

NOTE :-

1. ALL DIMENSIONS ARE IN MM
2. THIS DRAWING IS SOLELY MEANT TO BE UNDERSTOOD.

| Sr.No | DESCRIPTION | REV.NO | DRAWN | DATE |
|---|---|---|---|---|
| 1. | PUF PANEL ADD | REV.01 | S.J. | 02.12.2024 |
| 2. | | | | |

This drawing & design is the property of NIHVA TECHNOLOGIES. Not to be sold or copied to any other concern.

| | NAME | SIGN | DATE |
|---|---|---|---|
| DRAWN | S.J | | 14.11.2024 |
| CHECK | S.W. | | 14.11.2024 |
| APPRD. | V.T | | 14.11.2024 |

If any queries contact : projectsupport@nihva.com

ALL DIMENSION ARE IN mm

TITLE:- HIGH SPEED DOOR STRUCTURE DRAWING

NIHVA TECHNOLOGIES PVT. LTD. PUNE
Tel : 020 66304033
Email:- info@nihva.com
Website:- www.nihva.com

CLIENT - SERUM INSTITUTE OF INDIA PVT.LTD

PROJECT - HIGH SPEED DOOR ST.

FORMAT NO - NIHVA-DD-F-03

DWG. NO. : NIHVA/24-25/SM/24100601 | REV- R01

SCALE: NTS | WT: | SHEET: