


# VERTICAL PROFILE FOR PANEL

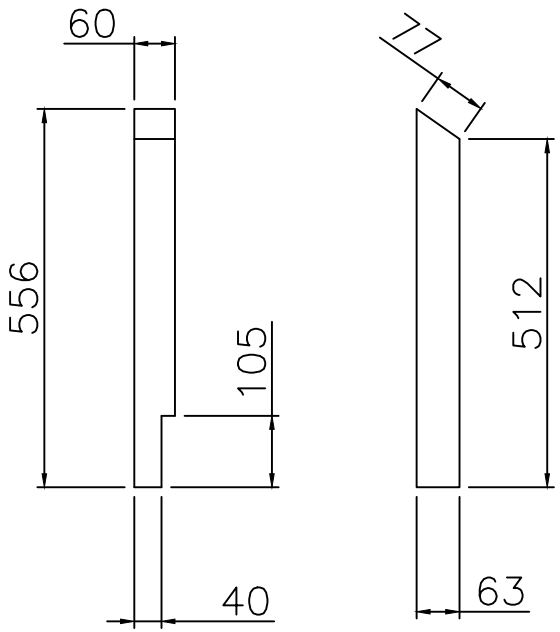


1 L.H. SIDE GNT- 6
QTY - 2 NOS

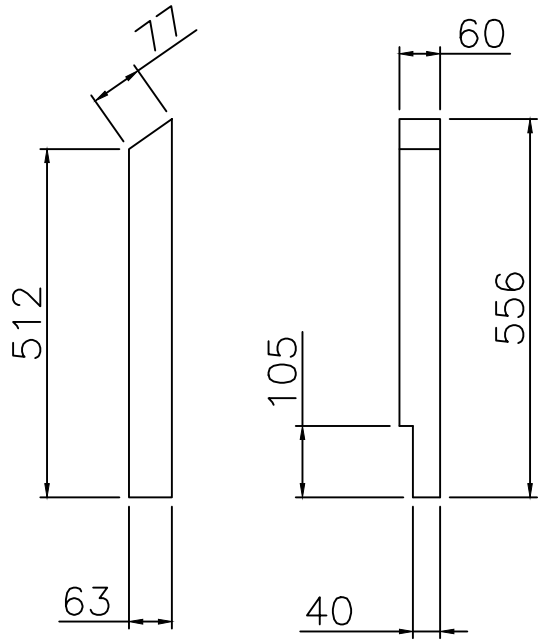


2 R.H. SIDE GNT- 6
QTY - 2 NOS

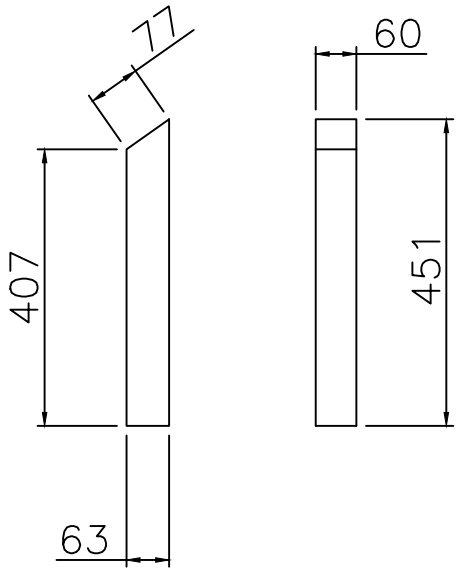


3 MIDDLE GNT- 6
QTY - 6 NOS

| REV. | DESCRIPTION. | REVISED BY | SIGN | DATE |
|---|---|---|---|---|
| 000 | RELEASED DWG FOR MANUFACTURING | N.K. | | 25.02.23 |
| | | | | |
| | | | | |

This drawing & design is the property of NIHVA TECHNOLOGIES. Not to be sold or copied to any other concern.

TITLE
VERTICAL PROFILE FOR PANEL

NIHVA
NIHVA TECHNOLOGIES PVT. LTD.

| | NAME | SIGN | DATE |
|---|---|---|---|
| DRAWN | N.K. | | 25.02.23 |
| CHECK | P.M. | | 25.02.23 |
| APPRD. | V.T. | | 25.02.23 |

CLIENT - MEHTA HOUSE - 1
LOCATION -
PRODUCT - RETRACTABLE ROOF

If any queries contact : projectsautomation@nihva.com

NIHVA\22-23\02XX | REV- 0

ALL DIMENSION ARE IN mm | SCALE: NTS | SHEET: 01 OF 01