




TOP PLAN OF AUXILIARY GIRDER

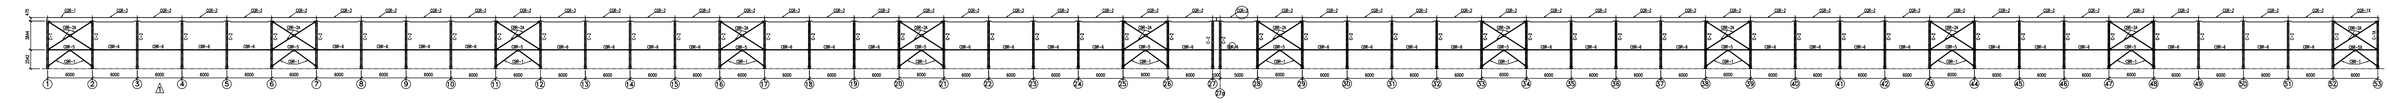


SIDE ELEVATION CRANE LEG ON ROW E

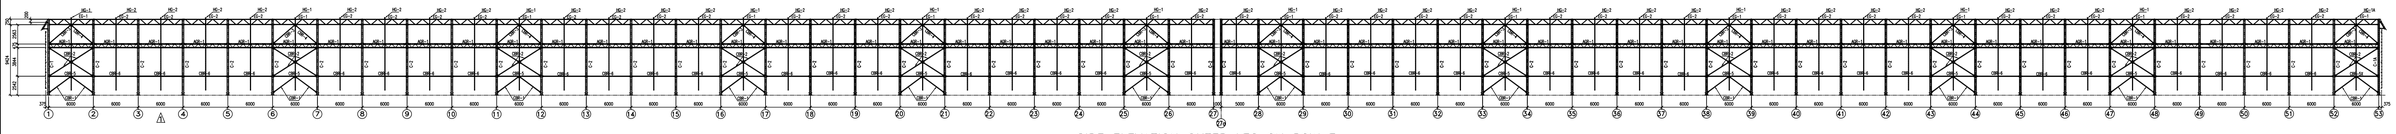


SIDE ELEVATION OUTER LEG ON ROW E

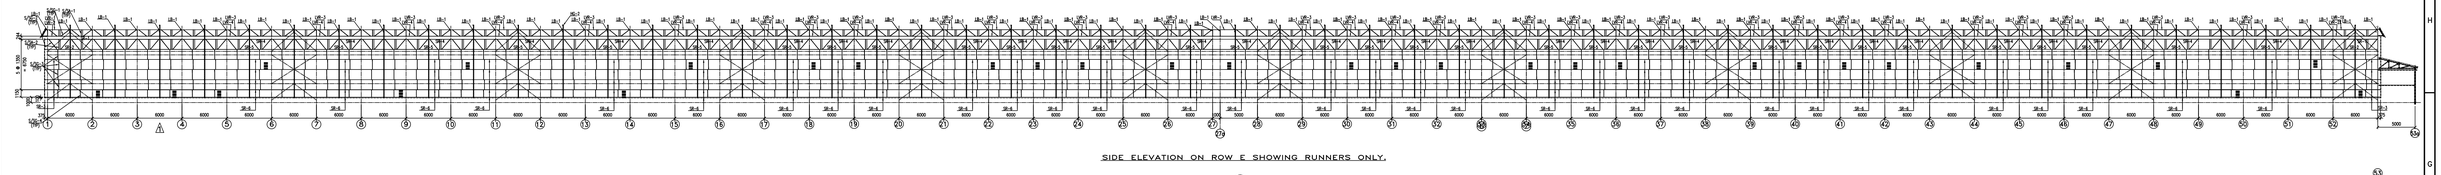


SIDE ELEVATION ON ROW E SHOWING RUNNERS ONLY.

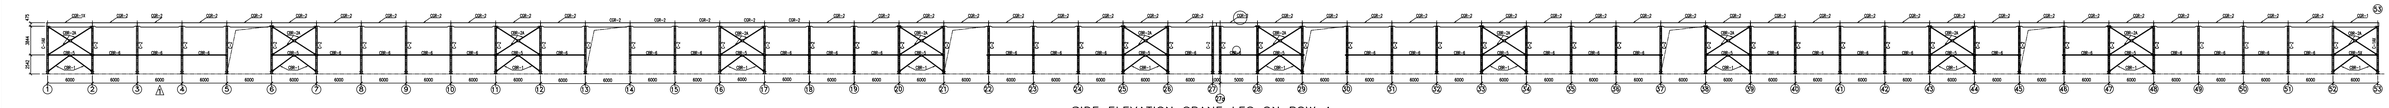


SIDE ELEVATION CRANE LEG ON ROW A

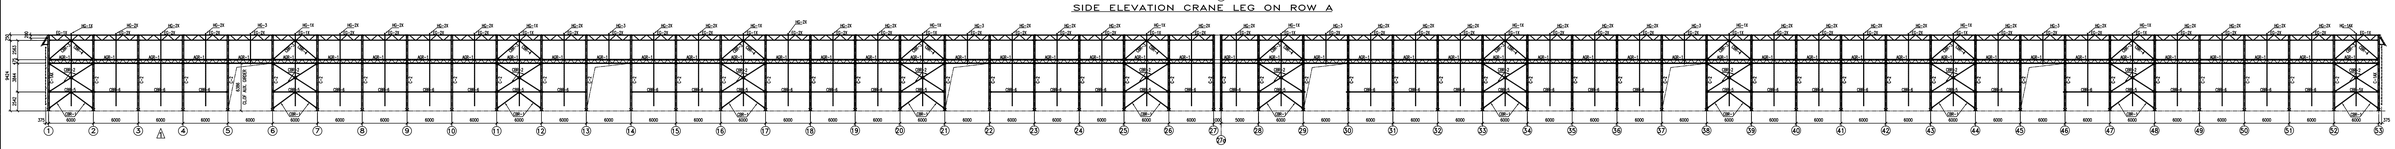

SIDE ELEVATION OUTER LEG ON ROW A

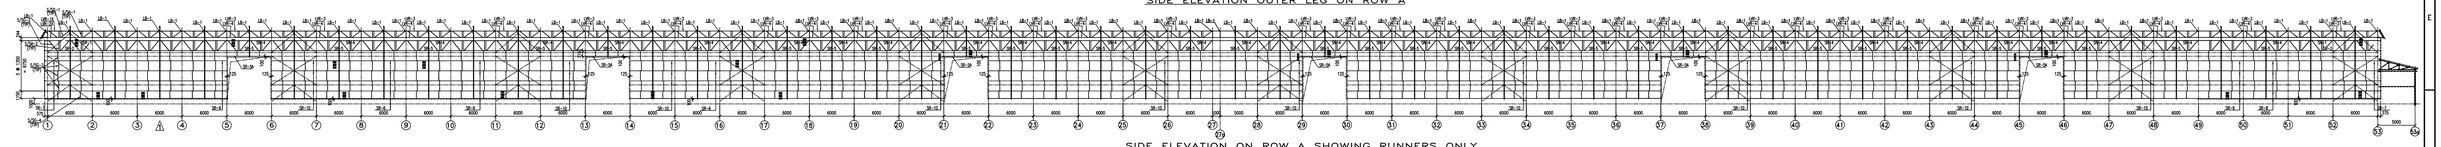

SIDE ELEVATION ON ROW A SHOWING RUNNERS ONLY

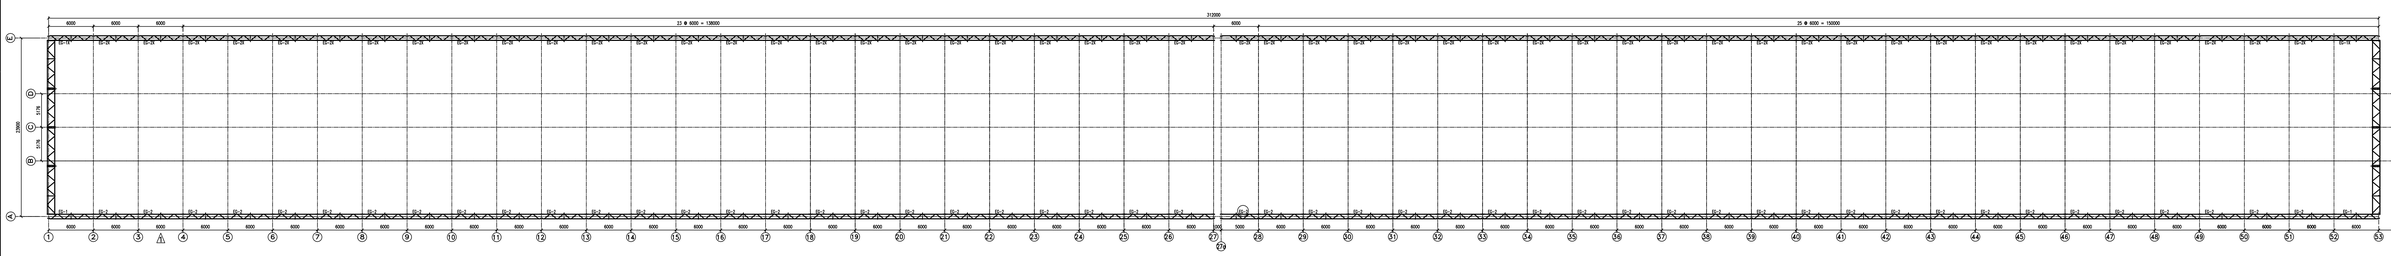

PLAN AT WIND GIRDERS,EAVES GIRDER AT DIFFERENT LVLS

SHEETING ARRGT. SHOWN HERE ARE INDICATIVE FOR EXTENT & TYPE ONLY. INDIVISUAL SHEET SIZES TO BE FINALIZED DURING SHEETING DETAILING.
FOR SIDE & GABLES TRANSLUCENT SHEETS AFTER EVERY 5 PRECOATED SHEETS WILL BE PROVIDED IN SAME VERTICAL PLANE.

NOTES:-
1. ALL DIMENSIONS ARE IN mm.
2. FOR DETAIL COLUMNS, COL. BRCGS. ETC. REFER REVELANT STRUCTURAL FABRICATION DRGS

REV.	REVISION DETAILS	NO.OF REV. MARKS	DRAWN	CHECKED	REVIEWED	APPROVED	DATE
1	REVISED AS PER OUTOTEC COMMENTS DT. 20.08.08 & MKD		D.BERA	AL.		AM.	21.08.08

SL.NO.	DRG. PRPD. BY	DESCRIPTION	DRAWING NO.	SHT	REV
		REFERENCE DRAWINGS			

	DESIGNED	DRAWN	CHECKED	REVIEWED	APPROVED
DATE		01.07.08	02.07.08	04.07.08	04.07.08 04.07.08
SIGN.					
NAME		D BERA	N.K	S.D	AL A.M

1. DO NOT SCALE, IF ANY DOUBT PLEASE ASK.
2. REVISION MARKS ARE INSCRIBED IN △

THIS DRAWING IS MBE'S PROPERTY AND MUST NOT BE USED EXCEPT IN CONNECTION WITH MBE'S WORK. REPRODUCTION, USE OR DISCLOSURE OF THE CONTENTS OF THIS DRAWING TO THIRD PARTY/IES WITHOUT EXPRESS / WRITTEN PERMISSION OF MBE IS STRICTLY PROHIBITED.

CLIENT	VEDANTA ALUMINA LTD, JHARSUGUDA, INDIA
PROJECT	THREE UNITS OF GREEN ANODE PLANT
TITLE	PETCOKE STORAGE SHED G.A. & MARKING OF COLS.,COLS. BRCGS. ETC. ON GRID A & E

PROJECTS DIVISION — McNally Bharat ENGINEERING COMPANY LIMITED, 4, MANGOE LANE, KOLKATA, INDIA

MBE ~~PROPOSAL~~/SO NO. A 08901

SCALE 1 : 20 | MBE DRAWING NUMBER 1-B014-404-05-001 | SHT NO. 1 OF | REV. 1

CAD FILE : I-B014-404-05-001_SHT-#1

SHT-AO

ST-C-001 (REV-1) 01-10.01.2001