




FRONT VIEW

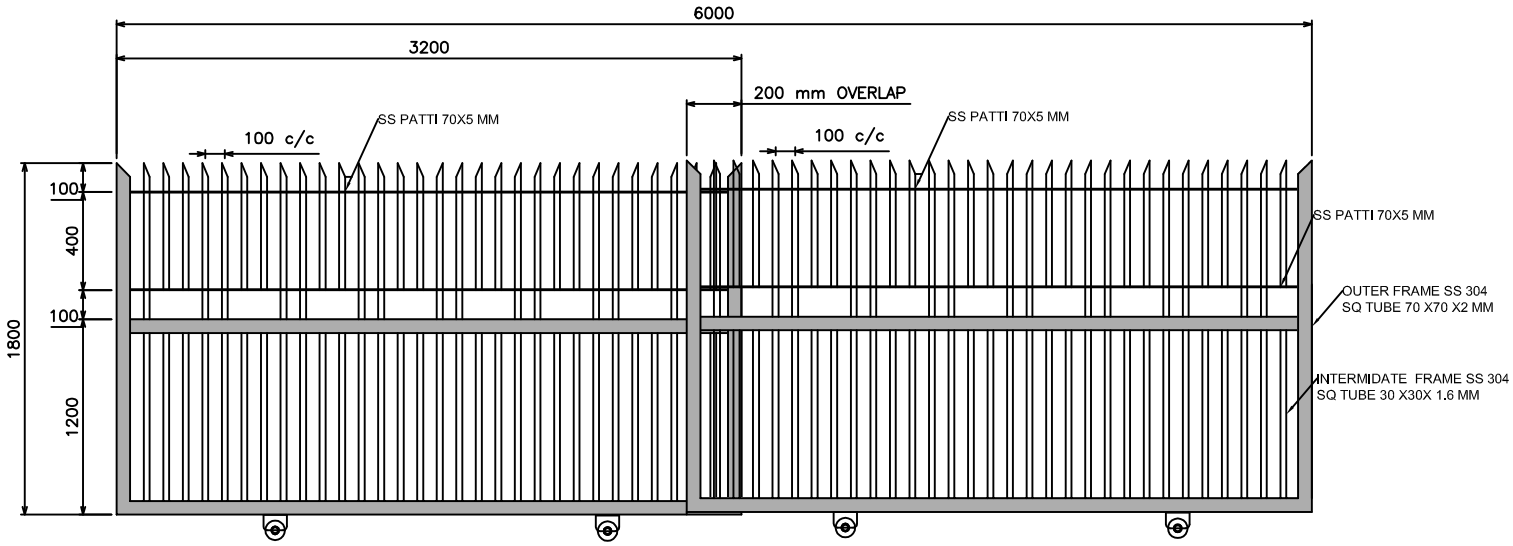

TOP VIEW

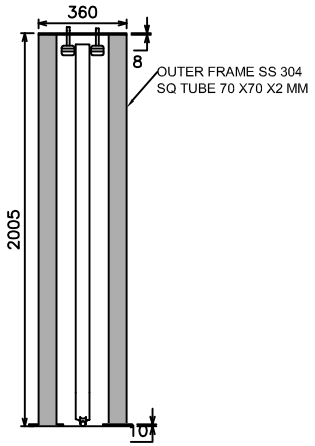


"C" COLUMN

SLIDING GATE SIZE = 6000(W) X 1800(H), QTY = 1 nos.
.OUTER FRAME = 70 X 70 X 2 mm
INNER FRAME = 30 X 30 X 1.6 mm.
GAP B/W FRAME = 100 c/c.
MATERIAL = SS 304
C' COLUMN VERTICAL SUPPORT = 4 NOS.
ALL DIMENSION ARE IN MM.

CLIENT APPORVAL :-

CLIENT - NITEEN PARULKAR ARCHITECTS

PROJECT - ATUL PROJECT

SITE - ANDHARI, MUMBAI

Drawing No - NVA/TSL GATE/ATUL/MUMBAI/1014-15

NIHVA
NIHVA TECHNOLOGIES PVT. LTD.
Tel : 020 66304033
Email:- info@nihva.com
Website:- www.nihva.com