


KEY PLAN

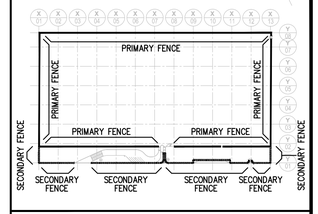

NOTE :

ALL M.S. SECTIONS THICKNESS & GUAGE MUST BE AS PER APPROVED SAMPLE.

REV.	DATE	DESCRIPTION	DRWN	CHKD
0	02.12.2016	FOR CONSTRUCTION	V. B.	M. D.

PROJECT TITLE:

NEW ORAL SOLID DOSE FACILITY
Bangalore

FOR CONSTRUCTION

DESIGN AND BUILT:

SHIMIZU CORPORATION


Head Office : Seavans South,No.2-3,Shibaura,1-chome, Minato-ku,Tokyo,Japan
TEL : 03-5441-1111
FAX : 03-5441-0302

DRAWING TITLE:

BOUNDRY WALL WHOLE PLAN


SCALE:	DATE:	DRAWN BY:	CHECKED BY:
1:1000	02.12.2016	VISHAL B.	AKASH K.

PROJECT :	DRAWING NO.	REV.
GSK	GSK-S-BW-PL-00	0

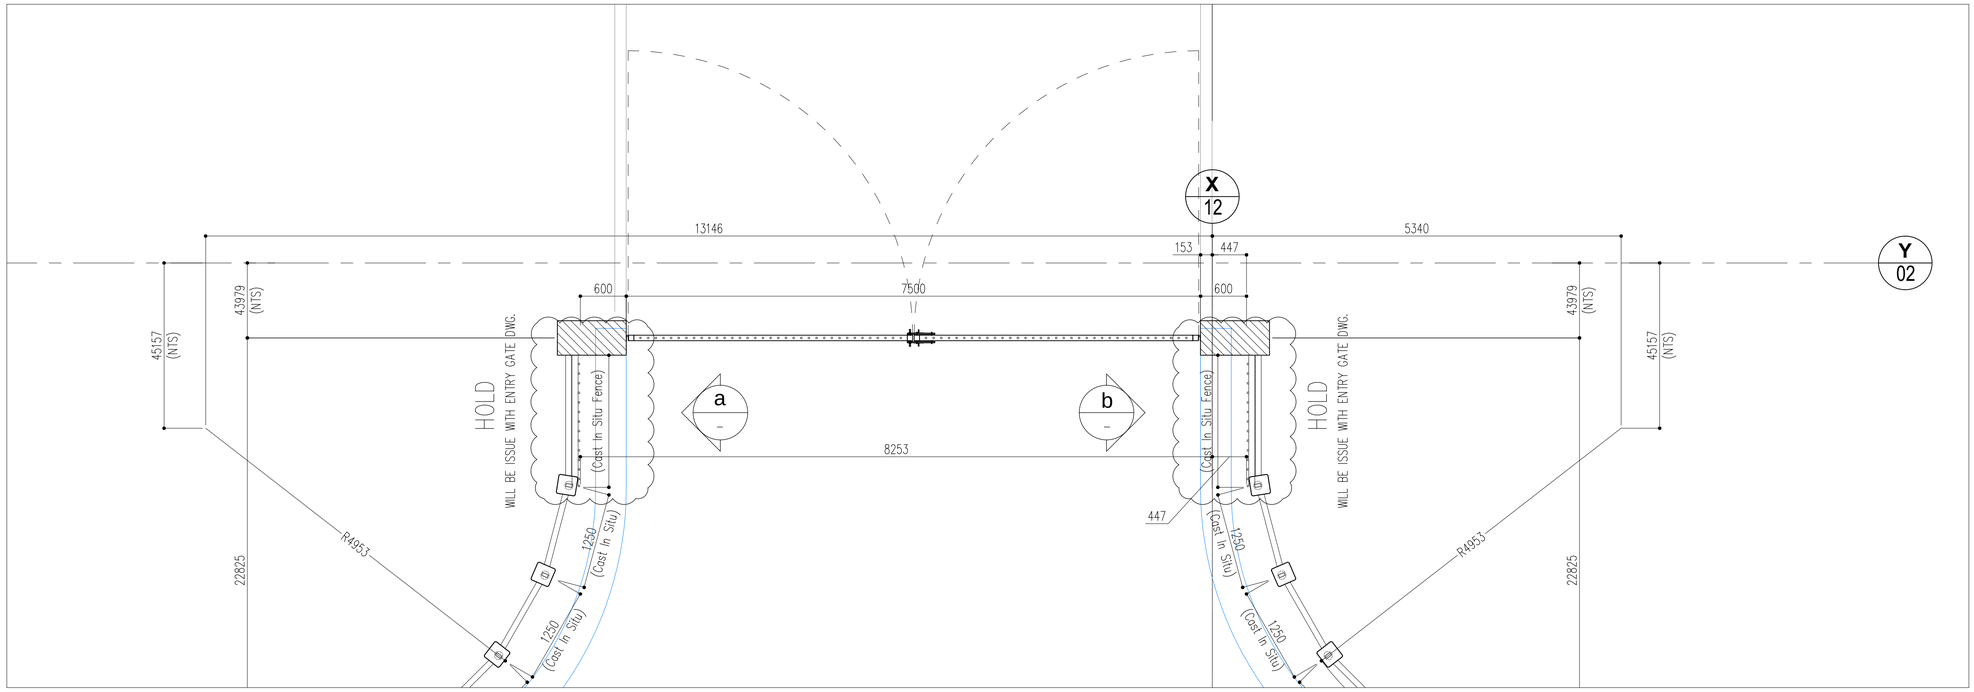

VEHICULAR ENTRY GATE SCHEME DESIGN PLAN


SCALE :

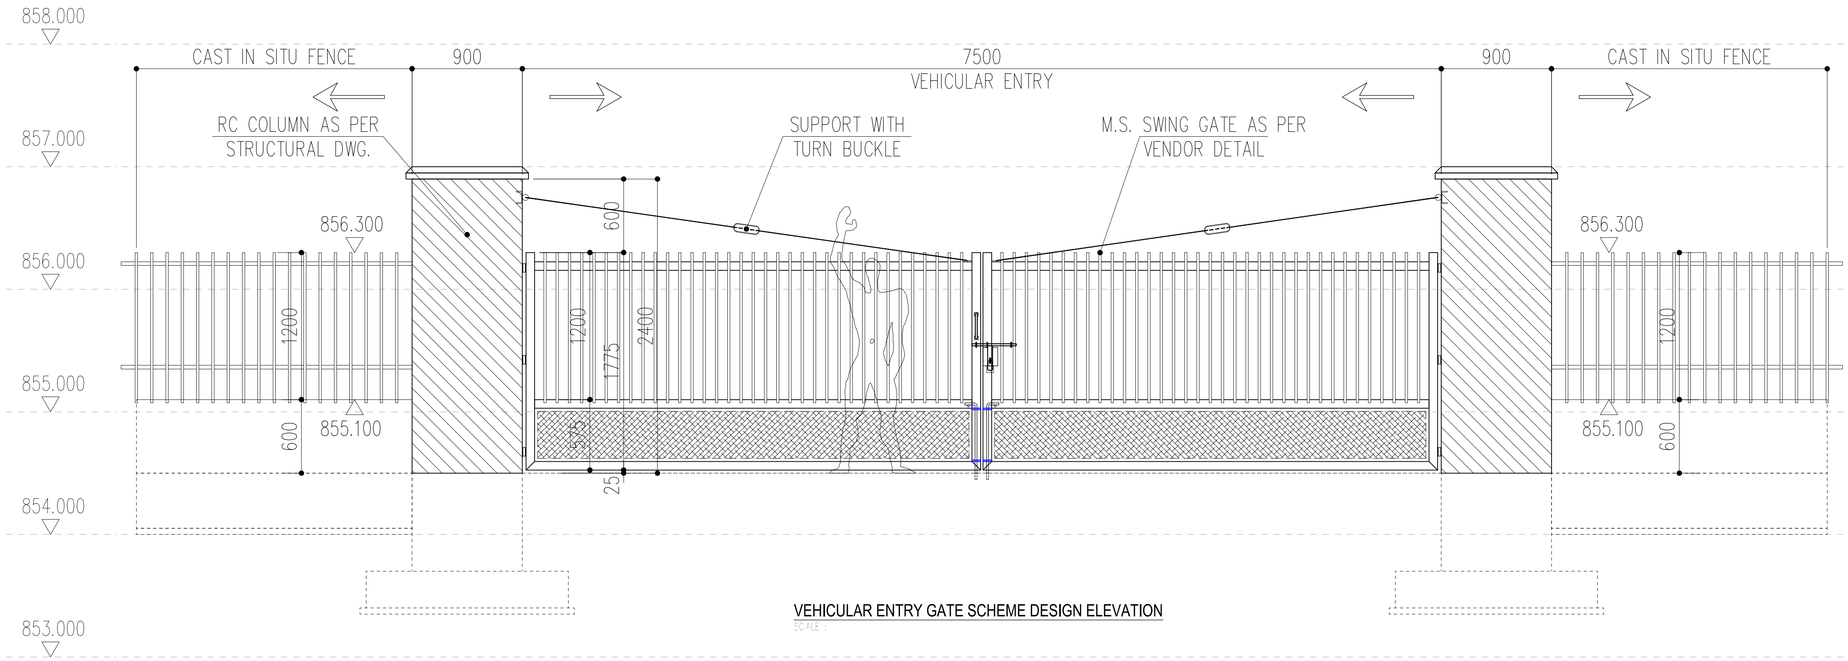

VEHICULAR ENTRY GATE SCHEME DESIGN ELEVATION

SCALE :

KEY PLAN

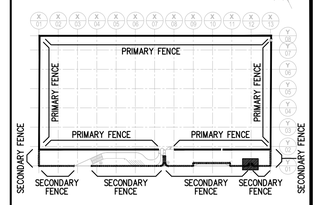

NOTE :

ALL M.S. SECTIONS THICKNESS & GUAGE MUST BE AS PER APPROVED SAMPLE.

REV.	DATE	DESCRIPTION	DRWN	CHKD
0	14.02.2017	FOR CONSTRUCTION	V. B.	M. D.

PROJECT TITLE:

NEW ORAL SOLID DOSE FACILITY
Bangalore

FOR CONSTRUCTION

DESIGN AND BUILT:

SHIMIZU CORPORATION


Head Office : Seaward South,No.2-3,Shibaura,1-chome, Minato-ku,Tokyo,Japan TEL : 03-5441-1111 FAX : 03-5441-0302

DRAWING TITLE:

VEHICULAR ENTRY GATE SCHEME DESIGN
(PLAN & ELEVATION)


SCALE:	DATE:	DRAWN BY:	CHECKED BY:
1:40	14.02.2017	VISHAL B.	AKASH K.

PROJECT :	DRAWING NO.	REV.
GSK	GSK-S-GD-VE-PL-01	0

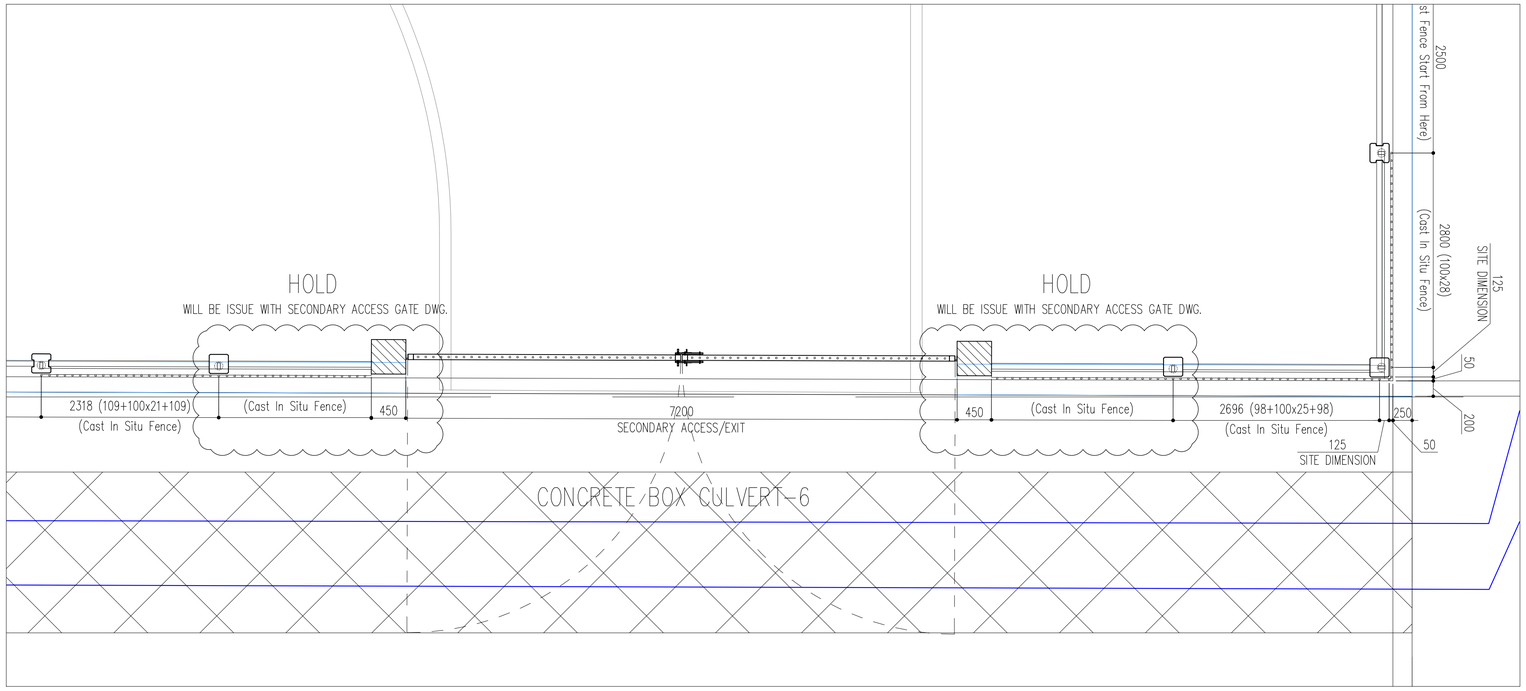

SECONDARY ACCESS / EXIT GATE SCHEME DESIGN PLAN


SCALE :

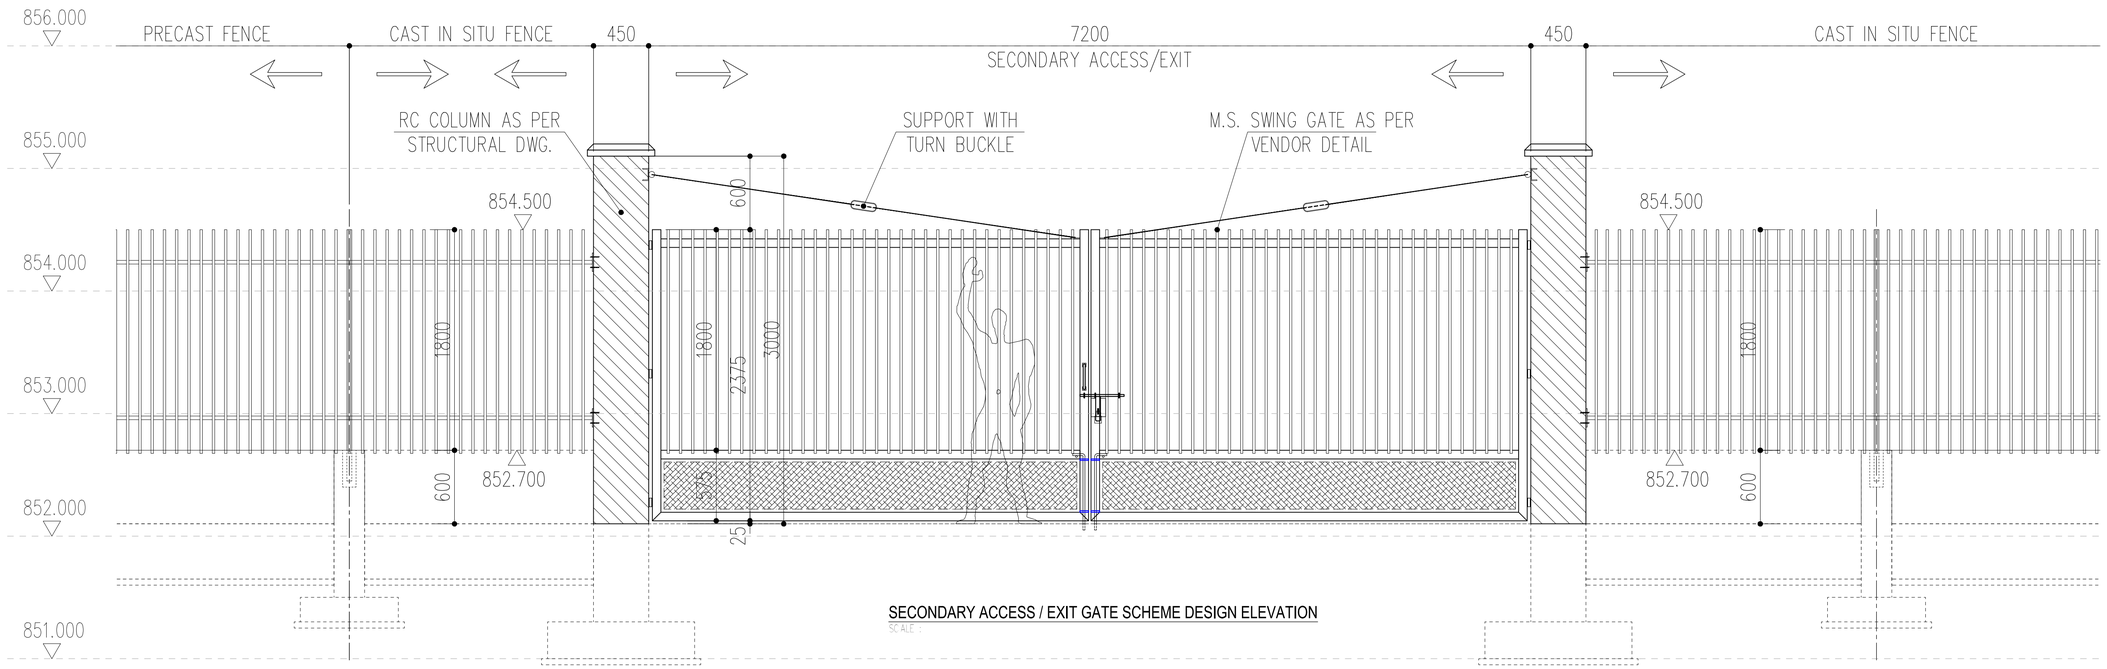

SECONDARY ACCESS / EXIT GATE SCHEME DESIGN ELEVATION

SCALE :

KEY PLAN

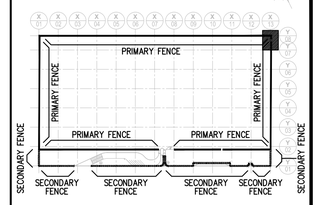

NOTE :

ALL M.S. SECTIONS THICKNESS & GUAGE MUST BE AS PER APPROVED SAMPLE.

REV.	DATE	DESCRIPTION	DRWN	CHKD
0	14.02.2017	FOR CONSTRUCTION	V. B.	M. D.

PROJECT TITLE:

NEW ORAL SOLID DOSE FACILITY
Bangalore

FOR CONSTRUCTION

DESIGN AND BUILT:

SHIMIZU CORPORATION


Head Office : Seavans South,No.2-3,Shibaura,1-chome, Minato-ku,Tokyo,Japan
TEL : 03-5441-1111
FAX : 03-5441-0302

DRAWING TITLE:

SECONDARY ACCESS/EXIT GATE SCHEME DESIGN
(PLAN & ELEVATION)


SCALE:	DATE:	DRAWN BY:	CHECKED BY:
1:40	14.02.2017	VISHAL B.	AKASH K.

PROJECT :	DRAWING NO.	REV.
GSK	GSK-S-GD-SAE-PL-01	0

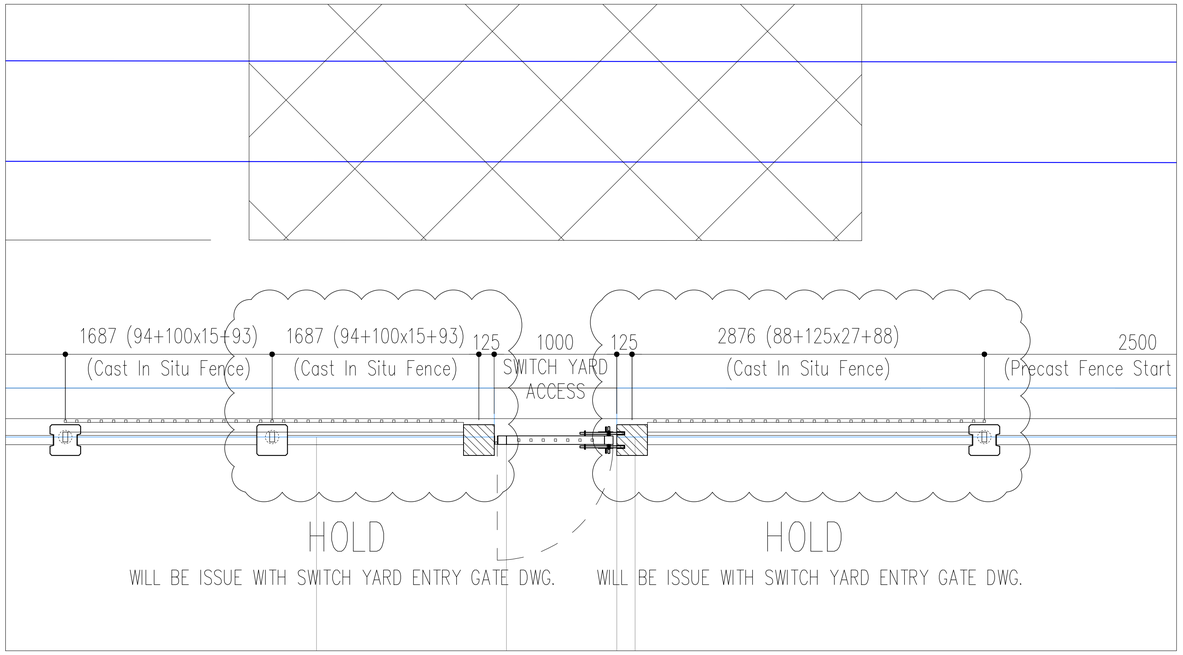

SWITCH YARD ACCESS GATE SCHEME DESIGN PLAN

SCALE :

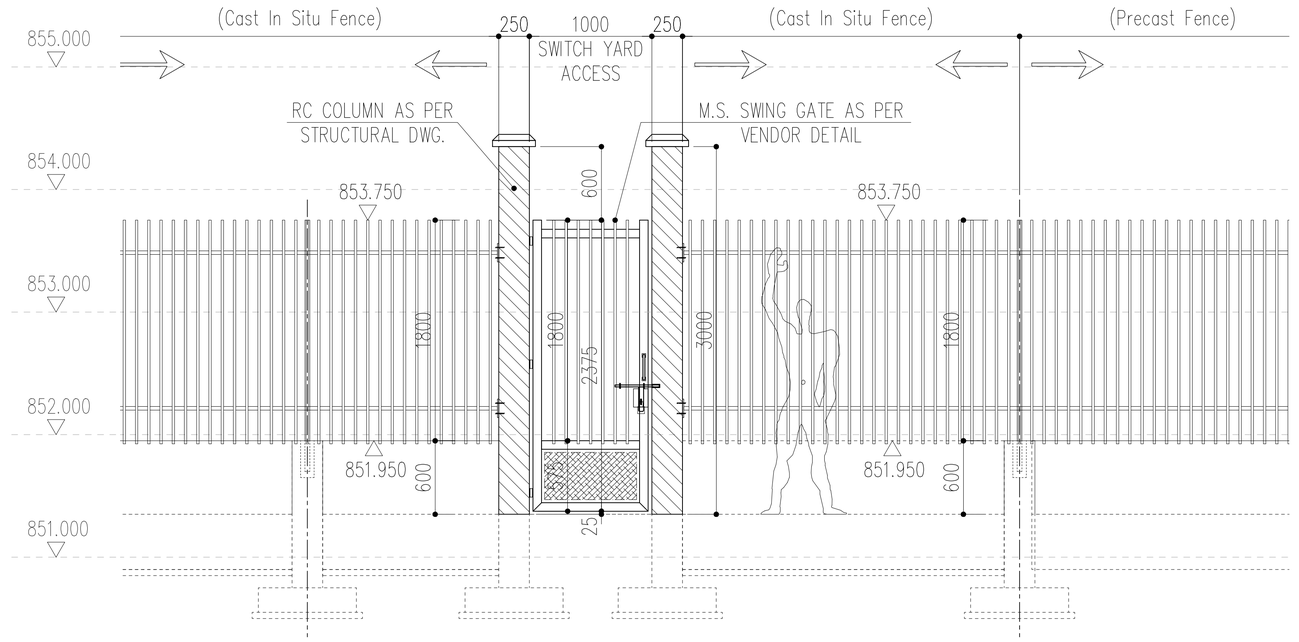


SWITCH YARD ACCESS GATE SCHEME DESIGN ELEVATION

SCALE :

KEY PLAN

NOT TO SCALE

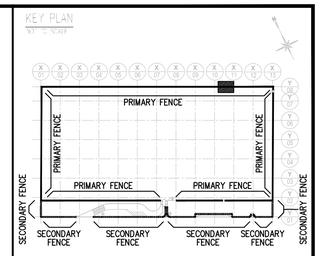

NOTE :

ALL M.S. SECTIONS THICKNESS & GUAGE MUST BE AS PER APPROVED SAMPLE.

REV.	DATE	DESCRIPTION	DRWN	CHKD
0	14.02.2017	FOR CONSTRUCTION	V. B.	M. D.

PROJECT TITLE:

NEW ORAL SOLID DOSE FACILITY
Bangalore

FOR CONSTRUCTION

DESIGN AND BUILT:

SHIMIZU CORPORATION


Head Office : Seawans South,No.2-3,Shibaura,1-chome, Minato-ku,Tokyo,Japan
TEL : 03-5441-1111
FAX : 03-5441-0302

DRAWING TITLE:

SWITCH YARD ACCESS GATE SCHEME DESIGN
(PLAN & ELEVATION)

SCALE:	DATE:	DRAWN BY:	CHECKED BY:
1:40	14.02.2017	VISHAL B.	AKASH K.

PROJECT :	DRAWING NO.	REV.
GSK	GSK-S-GD-SYA-PL-01	0

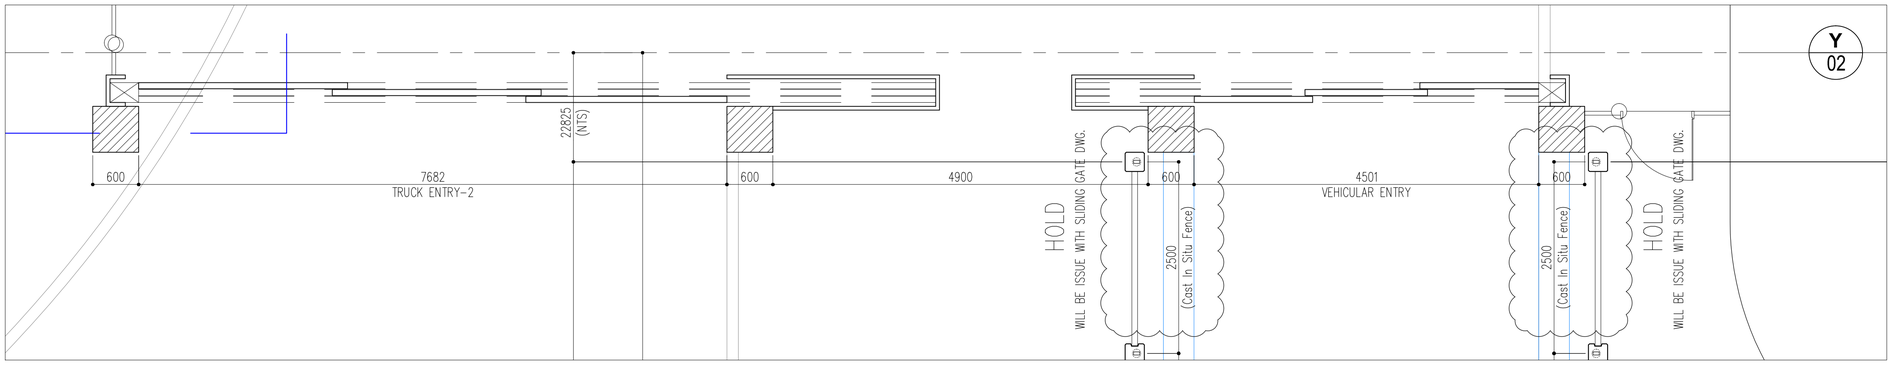


TRUCK ENTRY GATE-2 SCHEME DESIGN PLAN

SCALE :


MAIN ENTRY GATE SCHEME DESIGN PLAN

SCALE :

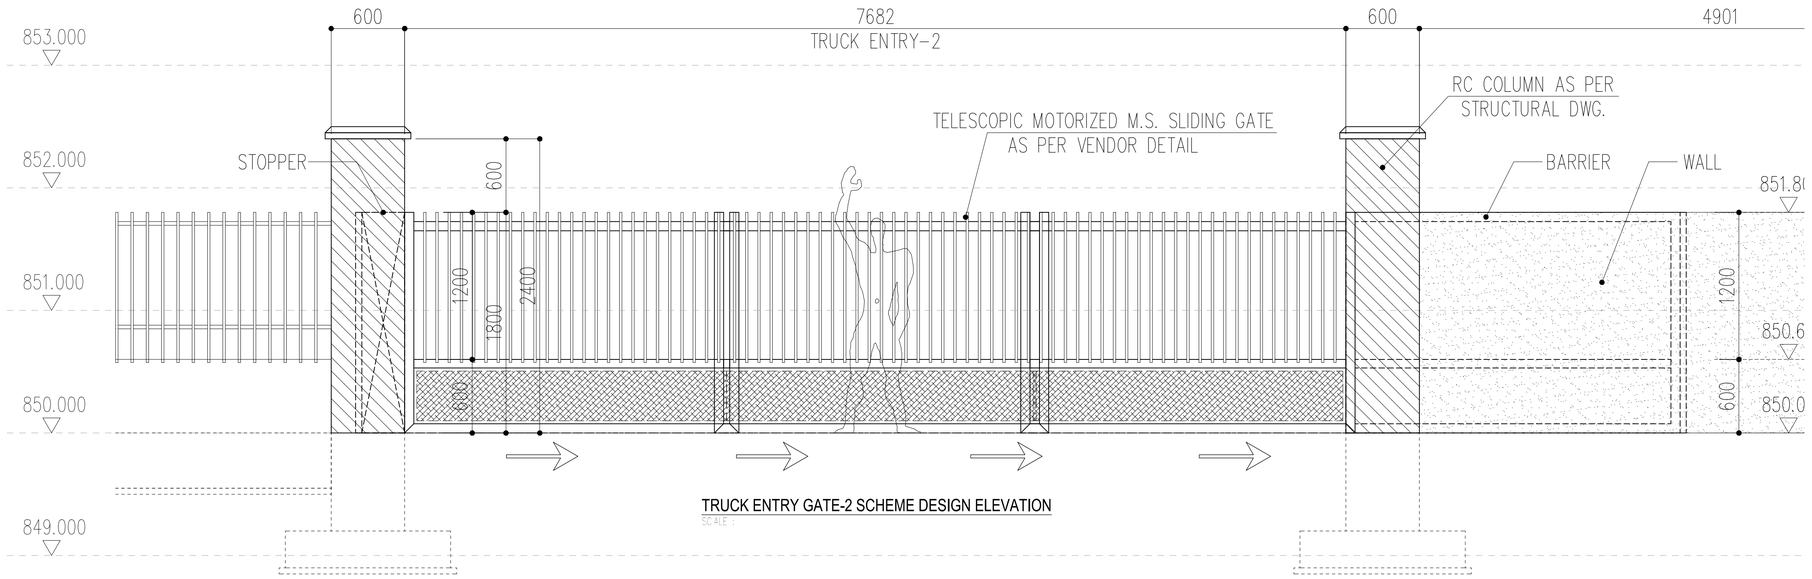

TRUCK ENTRY GATE-2 SCHEME DESIGN ELEVATION

SCALE :

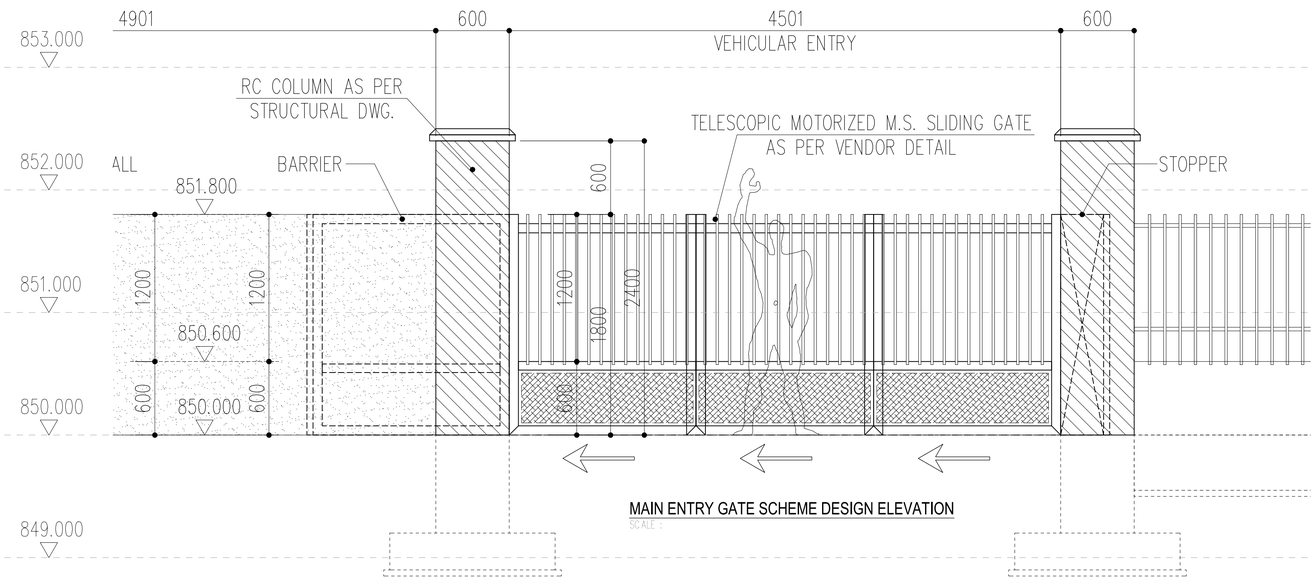


MAIN ENTRY GATE SCHEME DESIGN ELEVATION

SCALE :



TELESCOPIC MOTORIZED SLIDING GATE IMAGE FOR RERERENCE ONLY

KEY PLAN

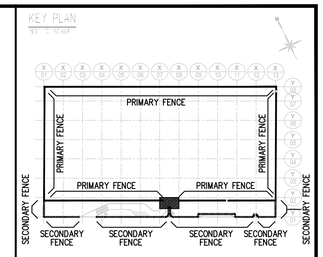

NOTE :

ALL M.S. SECTIONS THICKNESS & GUAGE MUST BE AS PER APPROVED SAMPLE.

REV.	DATE	DESCRIPTION	DRWN	CHKD
0	14.02.2017	FOR CONSTRUCTION	V. B.	M. D.

PROJECT TITLE:

NEW ORAL SOLID DOSE FACILITY
Bangalore

FOR CONSTRUCTION

DESIGN AND BUILT:

SHIMIZU CORPORATION

SHIMZ


Head Office : Seawans South,No.2-3,Shibaura,1-chome, Minato-ku,Tokyo,Japan TEL : 03-5441-1111 FAX : 03-5441-0302

DRAWING TITLE:

TRUCK ENTRY-2 & MAIN ENTRY GATE SCHEME DESIGN
(PLAN & ELEVATION)


SCALE:	DATE:	DRAWN BY:	CHECKED BY:
1:40	14.02.2017	VISHAL B.	AKASH K.

PROJECT :	DRAWING NO.	REV.
GSK	GSK-S-GD-ME-PL-01	0

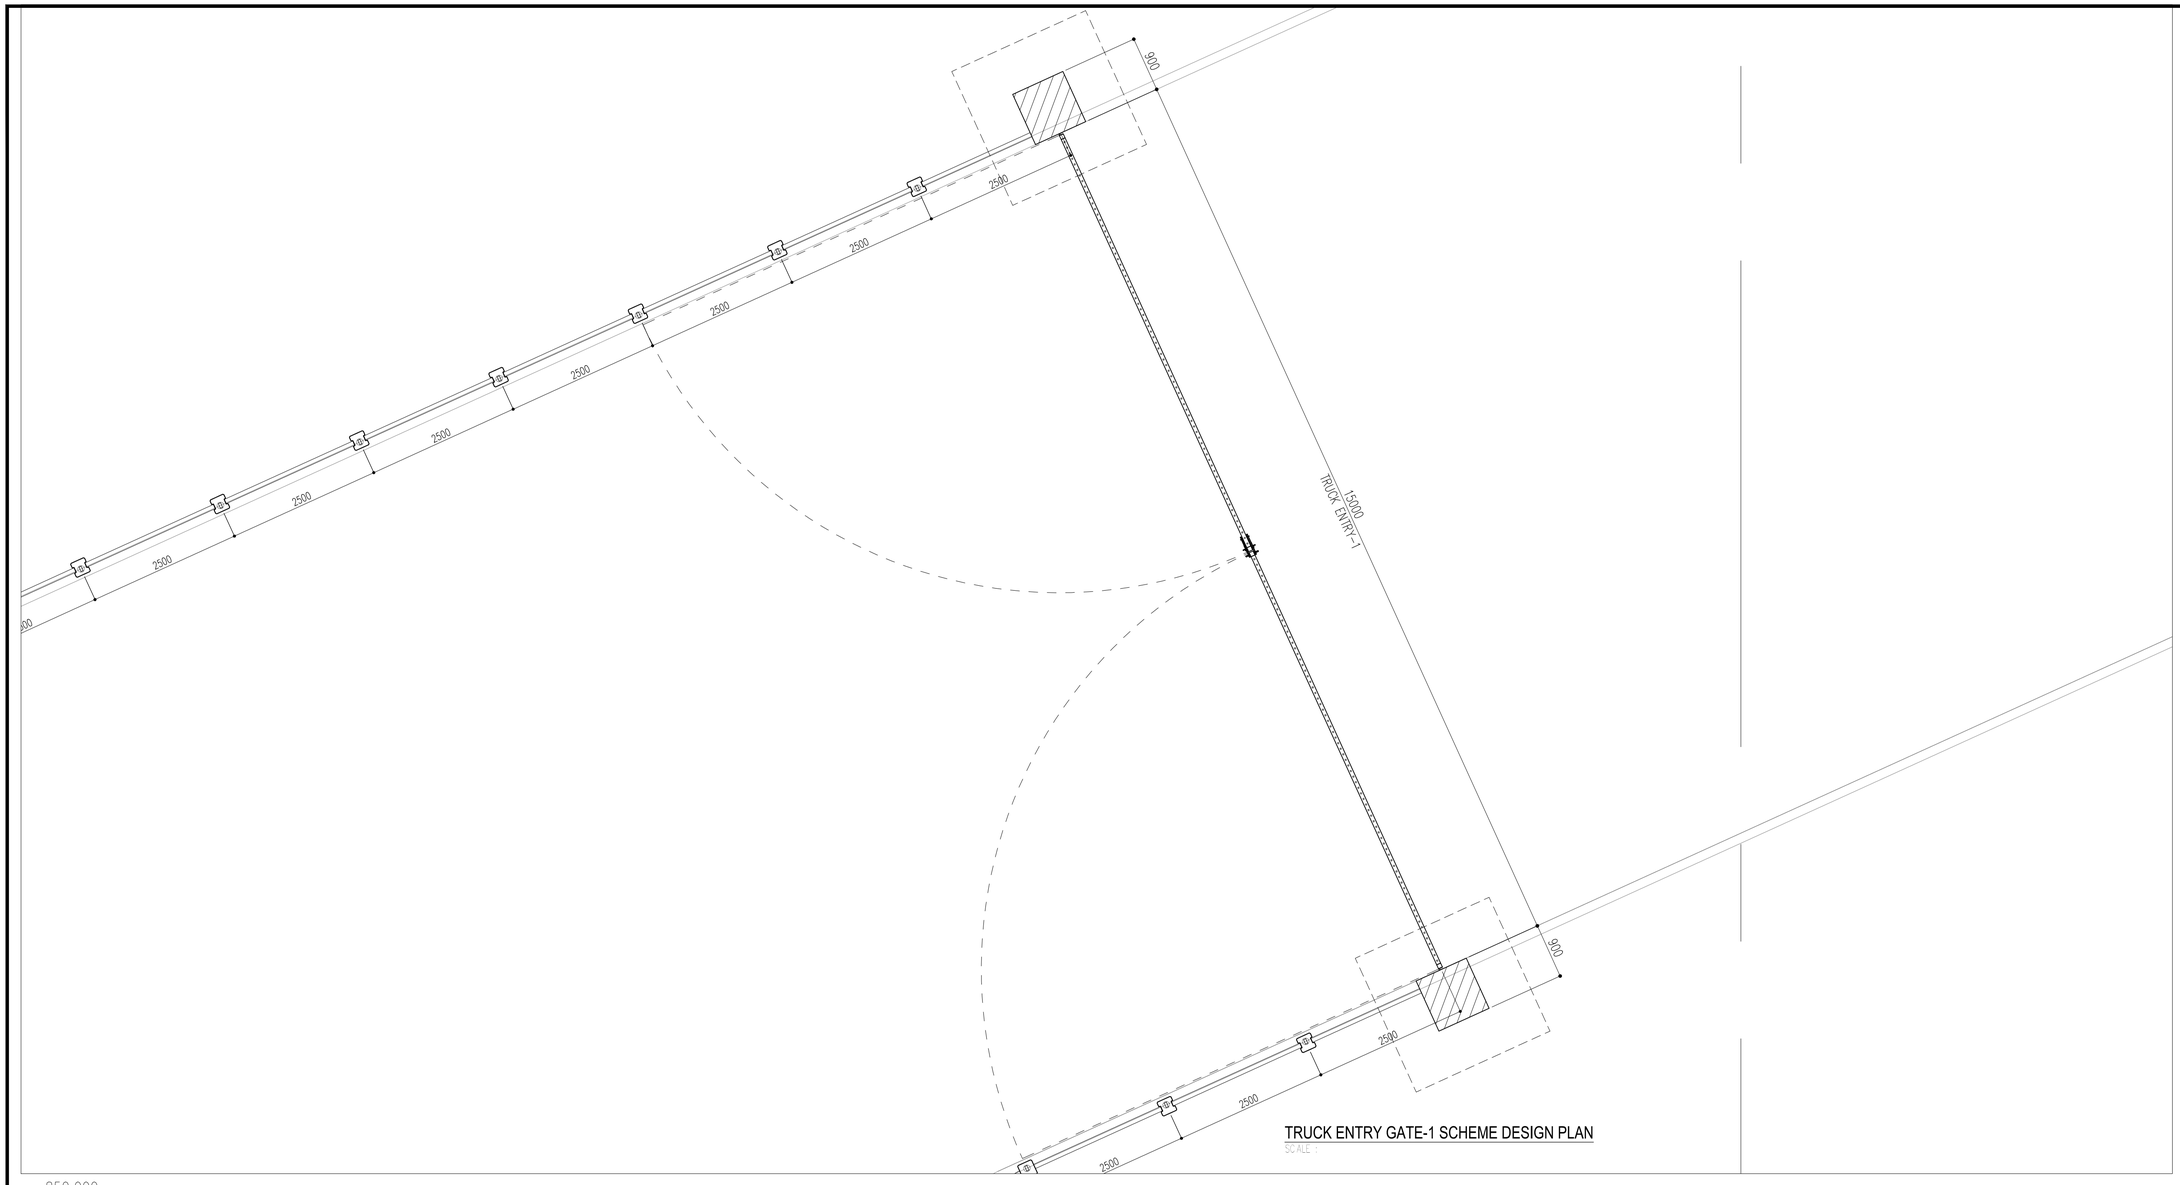

TRUCK ENTRY GATE-1 SCHEME DESIGN PLAN

SCALE :

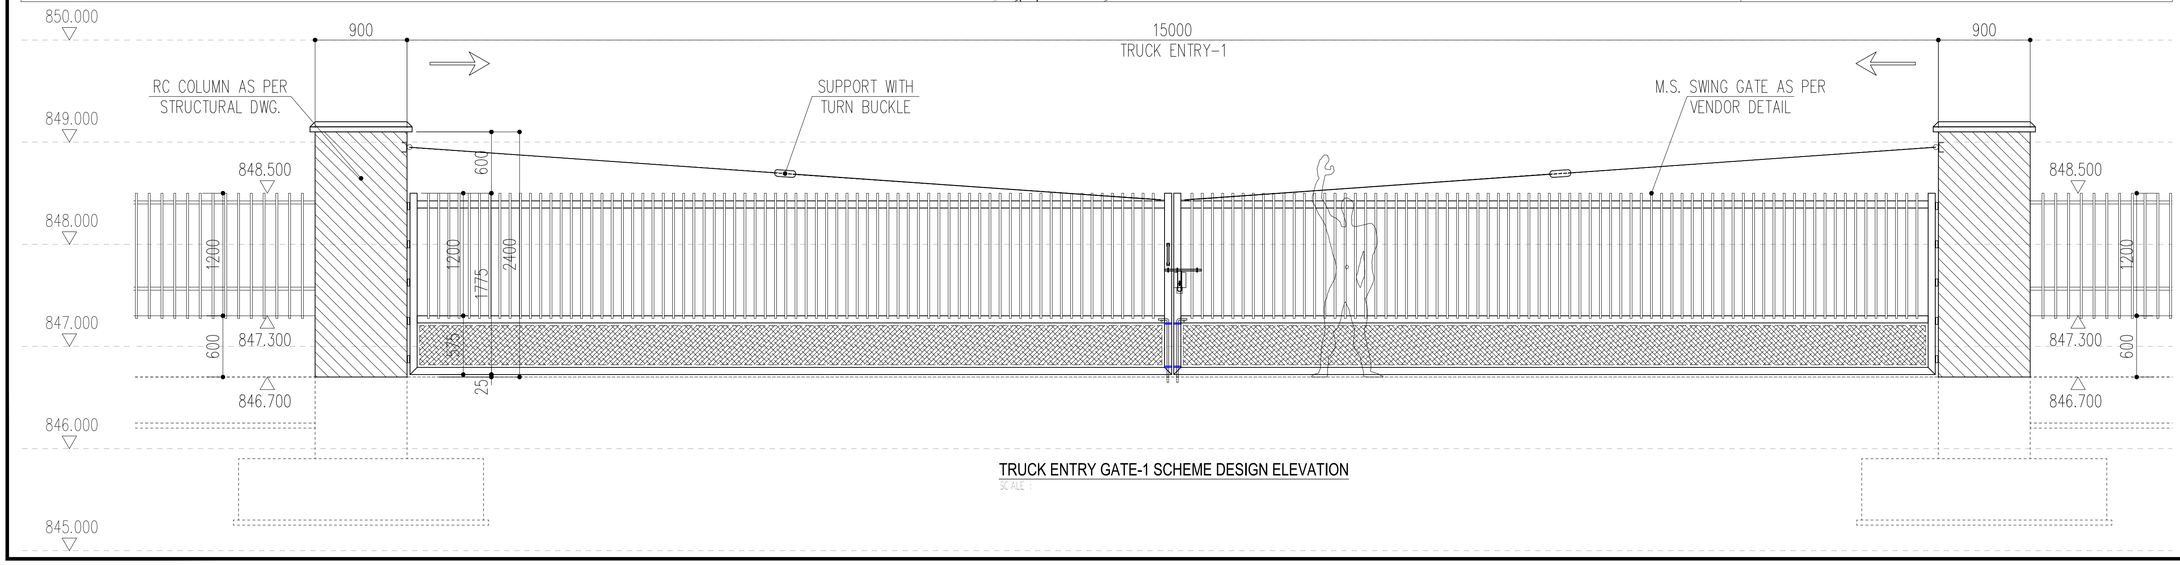


TRUCK ENTRY GATE-1 SCHEME DESIGN ELEVATION

SCALE :

KEY PLAN

NTS

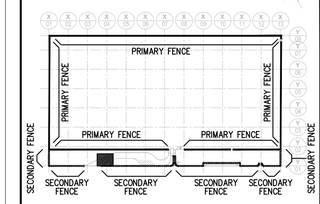

NOTE :

ALL M.S. SECTIONS THICKNESS & GUAGE MUST BE AS PER APPROVED SAMPLE.

REV.	DATE	DESCRIPTION	DRWN	CHKD
0	14.02.2017	FOR CONSTRUCTION	V. B.	M. D.

PROJECT TITLE:

NEW ORAL SOLID DOSE FACILITY
Bangalore

FOR CONSTRUCTION

DESIGN AND BUILT:

SHIMIZU CORPORATION

Head Office : Seawans South,No.2-3,Shibaura,1-chome, Minato-ku,Tokyo,Japan
TEL : 03-5441-1111
FAX : 03-5441-0302

DRAWING TITLE:

TRUCK ENTRY-1 GATE SCHEME DESIGN
(PLAN & ELEVATION)

SCALE:	DATE:	DRAWN BY:	CHECKED BY:
1:40	14.02.2017	VISHAL B.	AKASH K.

PROJECT :	DRAWING NO.	REV.
GSK	GSK-S-GD-TE-PL-01	0